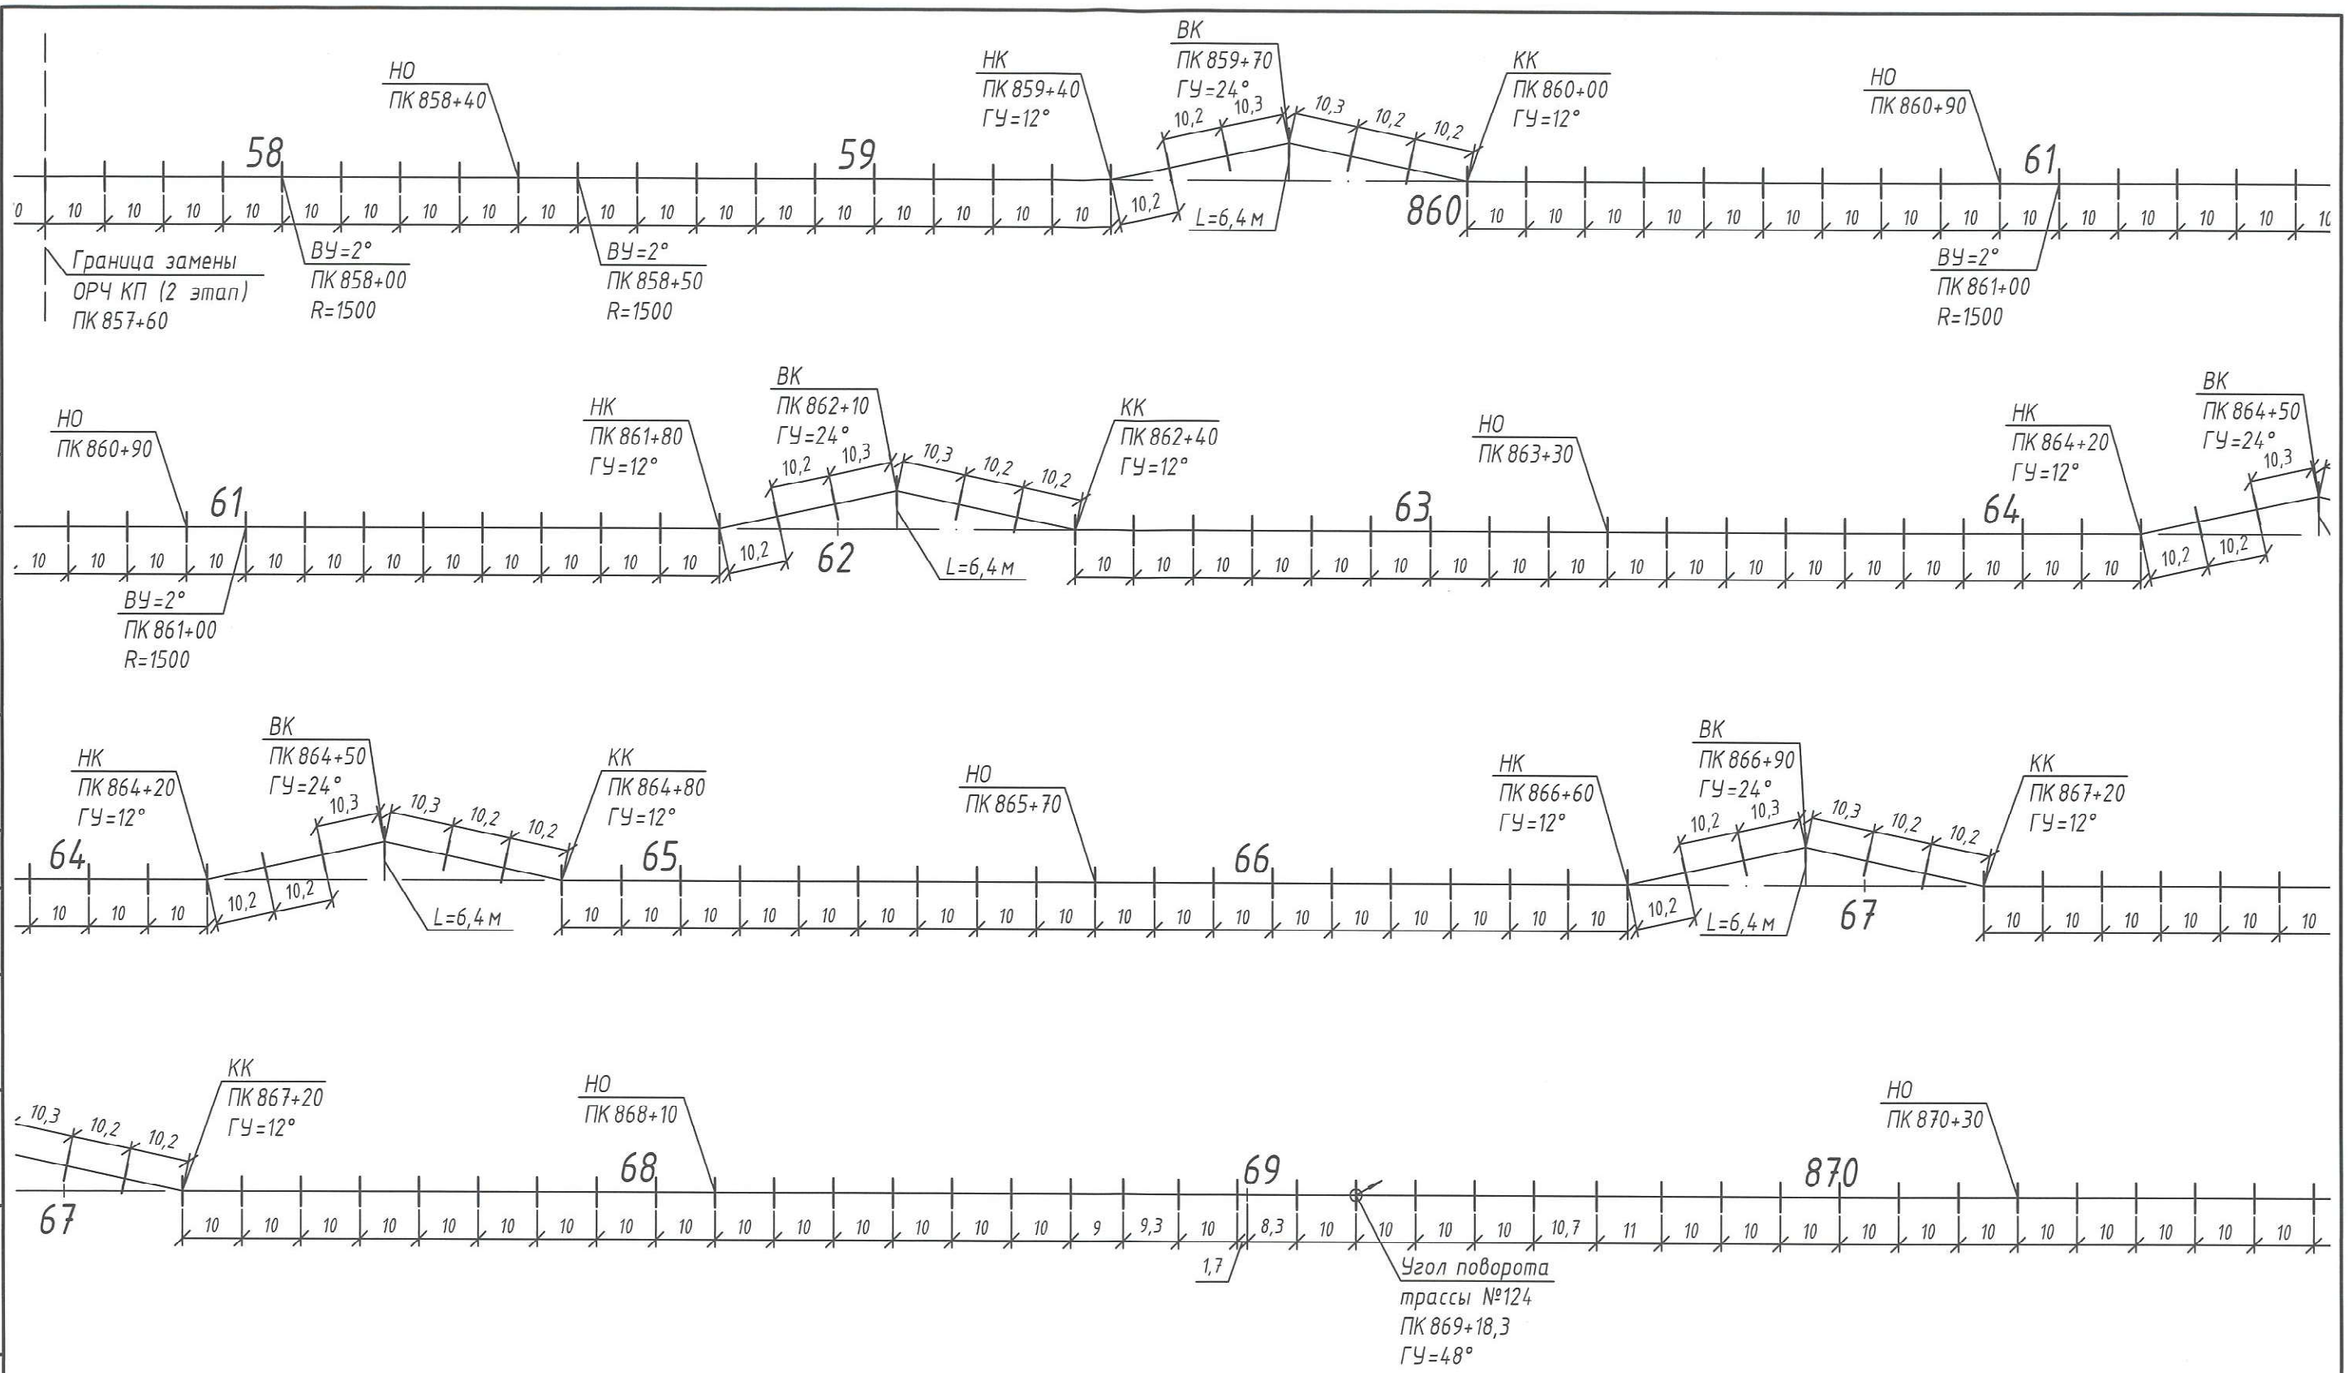


Условные обозначения:

- угол поворота трассы с указанием направления поворота;
- опора;

ГУ - горизонтальный угол;
ВУ - вертикальный угол;
НО - неподвижная опора:
L - расстояние между осью трассы и вершиной компенсатора.

1. Схема трассы метанолопровода составлена на основании проектной документации шифр И-1729-... и исполнительной документации.
2. Границы ручьев и рек указаны приблизительно по Г.В.В. 10% обеспеченности.
3. Пикет углов поворота трассы и компенсаторов определен по геометрической вершине угла.


Изм.	Кол.уч.	Лист	N док.	Подпись	Дата	III-Д-101/3103-КМ.Л2	
Гех.директор - рук.проектов		Летр			01.22	Техническое перевооружение ОРЧ конденсатопровода Моссояха-Дудинка, инв. №140001	
Нормоконт.		Лалетин			02.22	Техническое перевооружение опорно-ригельной части	Стадия: Р; Лист: 1; Листов: 24
Разраб.		Чернова			02.22	Схема трассы конденсатопровода на участке 88 км (ПК 857+60) до 127 км (ПК 251+38) до задвижки №497 (этап 2)	АО "НТГ" ПО 1

Согласовано

Нач. УМГ	Ивлев	
Гл.инж. УМГ	Фишман	

Инв.N подл. | Подпись и дата | Взам.инв.N

Формат А3

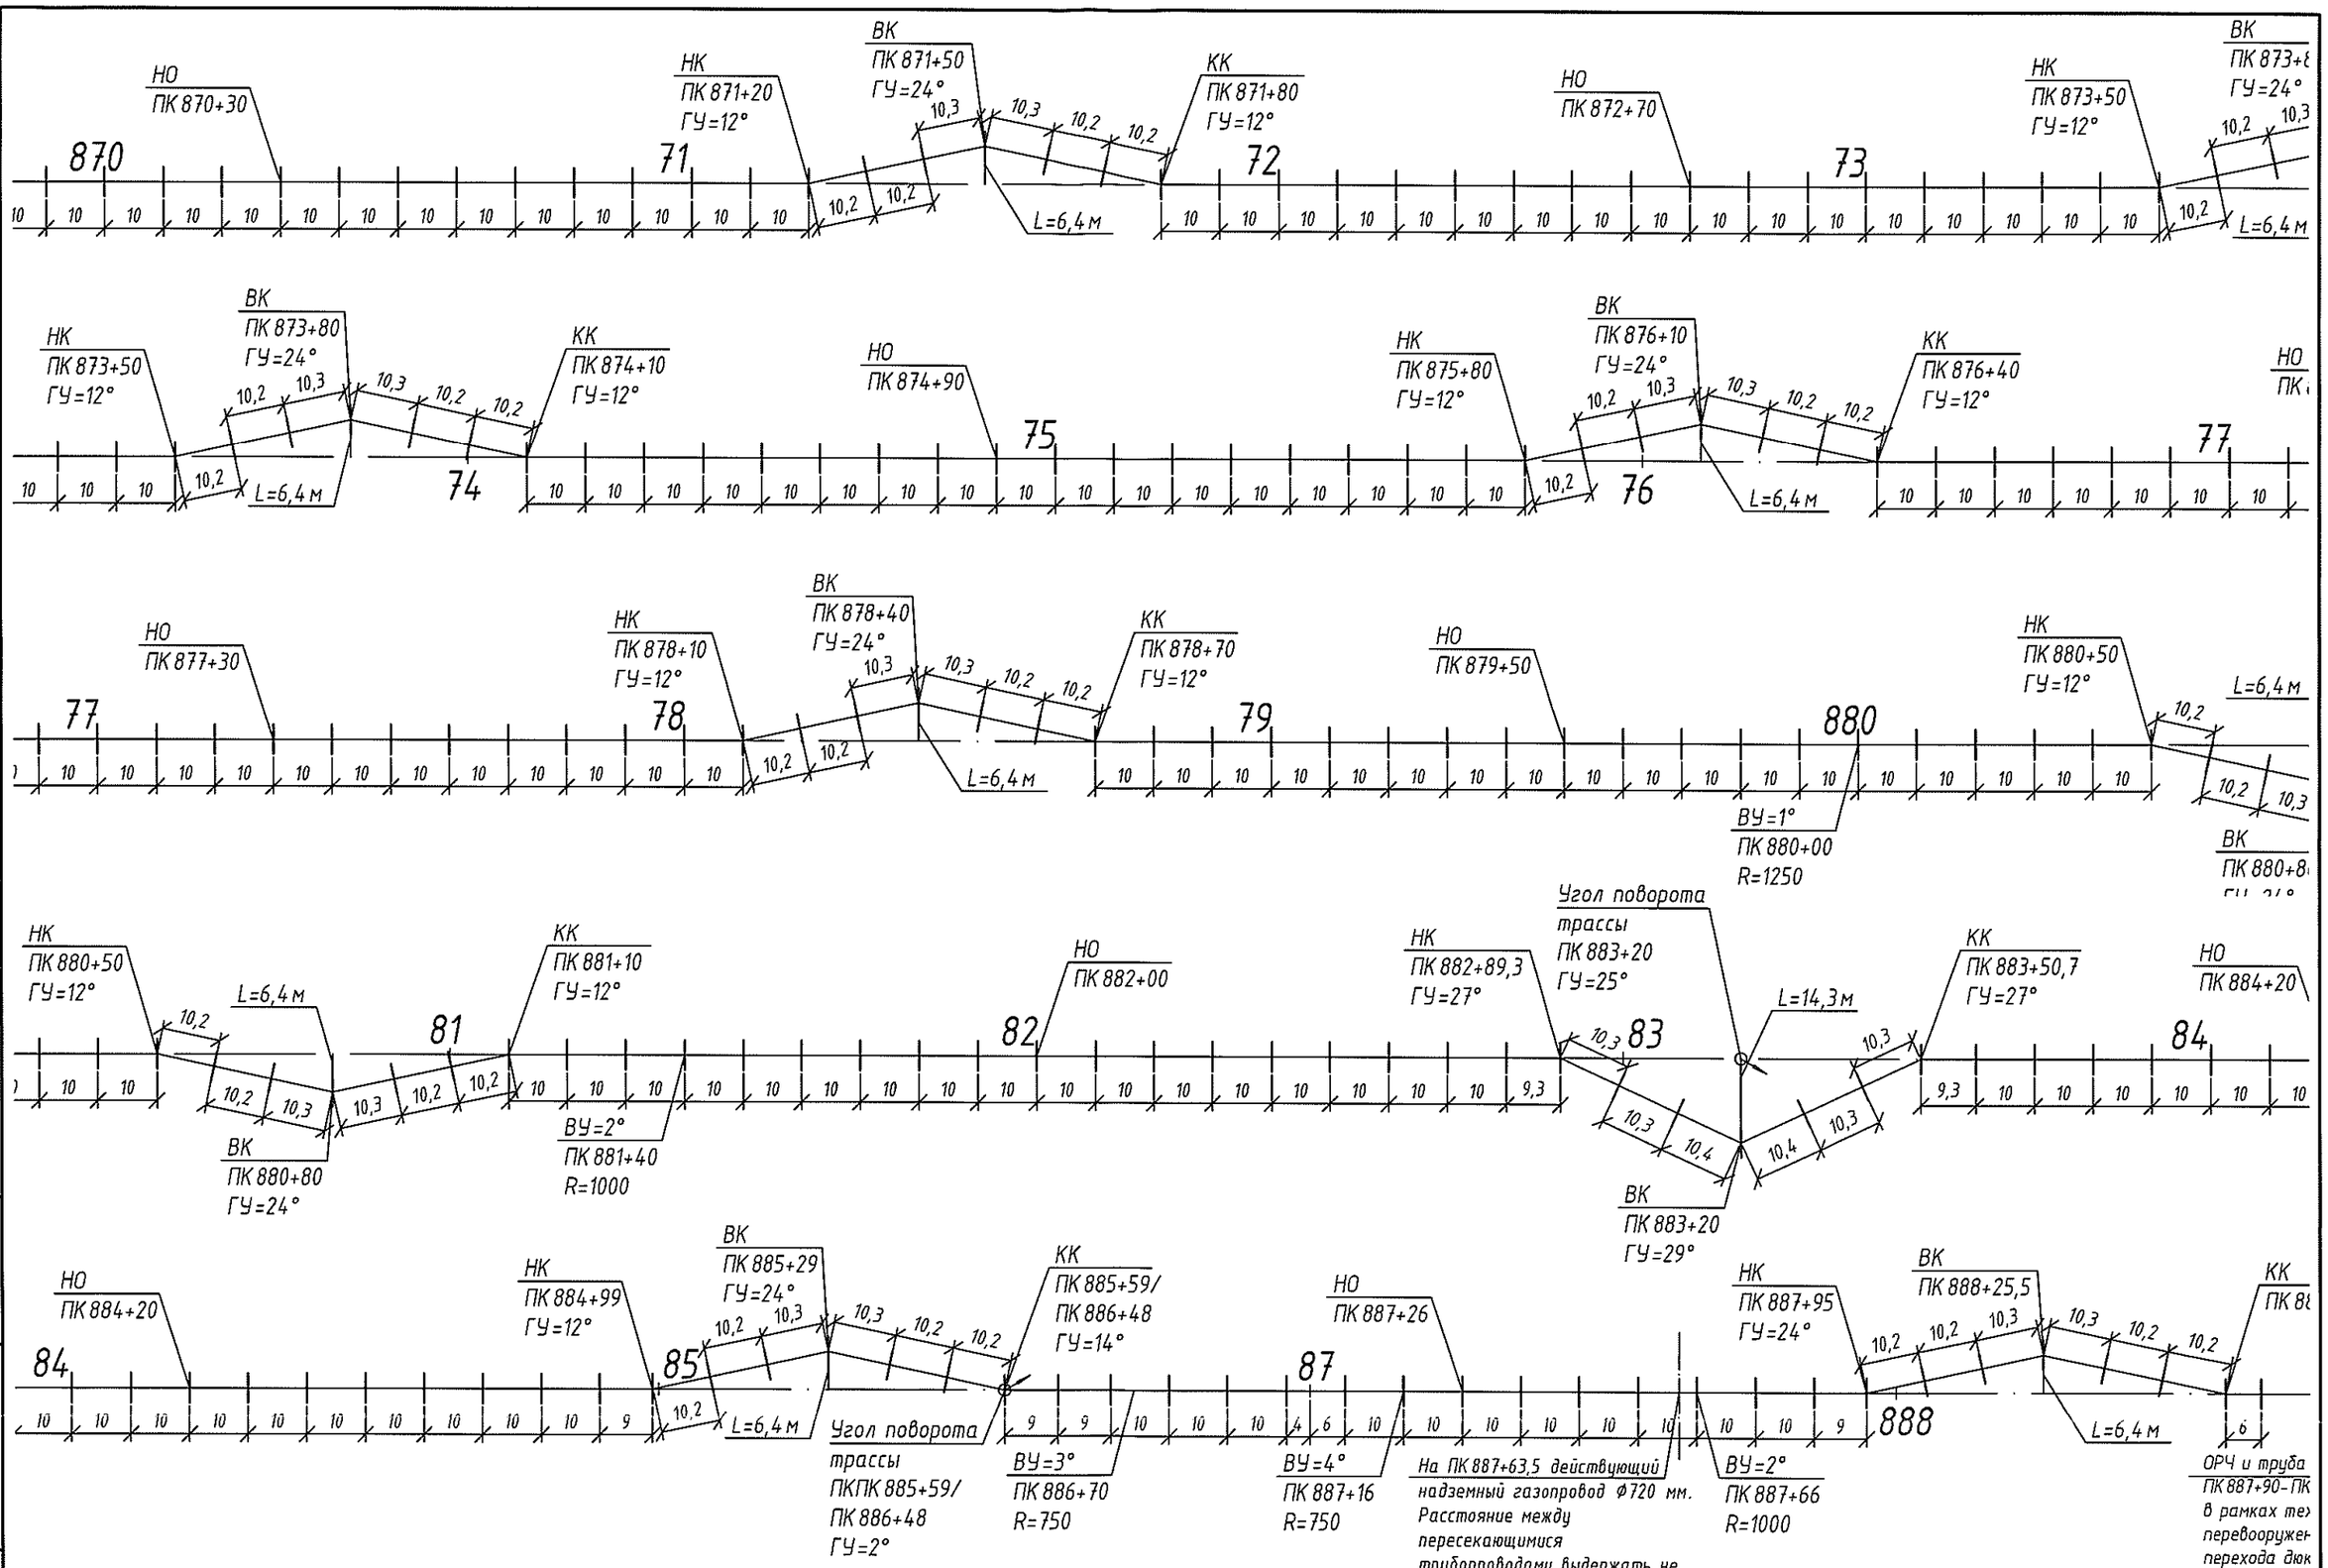

Согласовано


Взам.инв.N


Подпись и дата

Инв.N подл.

Изм.	Кол.уч.	Лист	N док.	Подпись	Дата	III-Д-101/3103-КМ.Л2	Лист 2

Формат А3

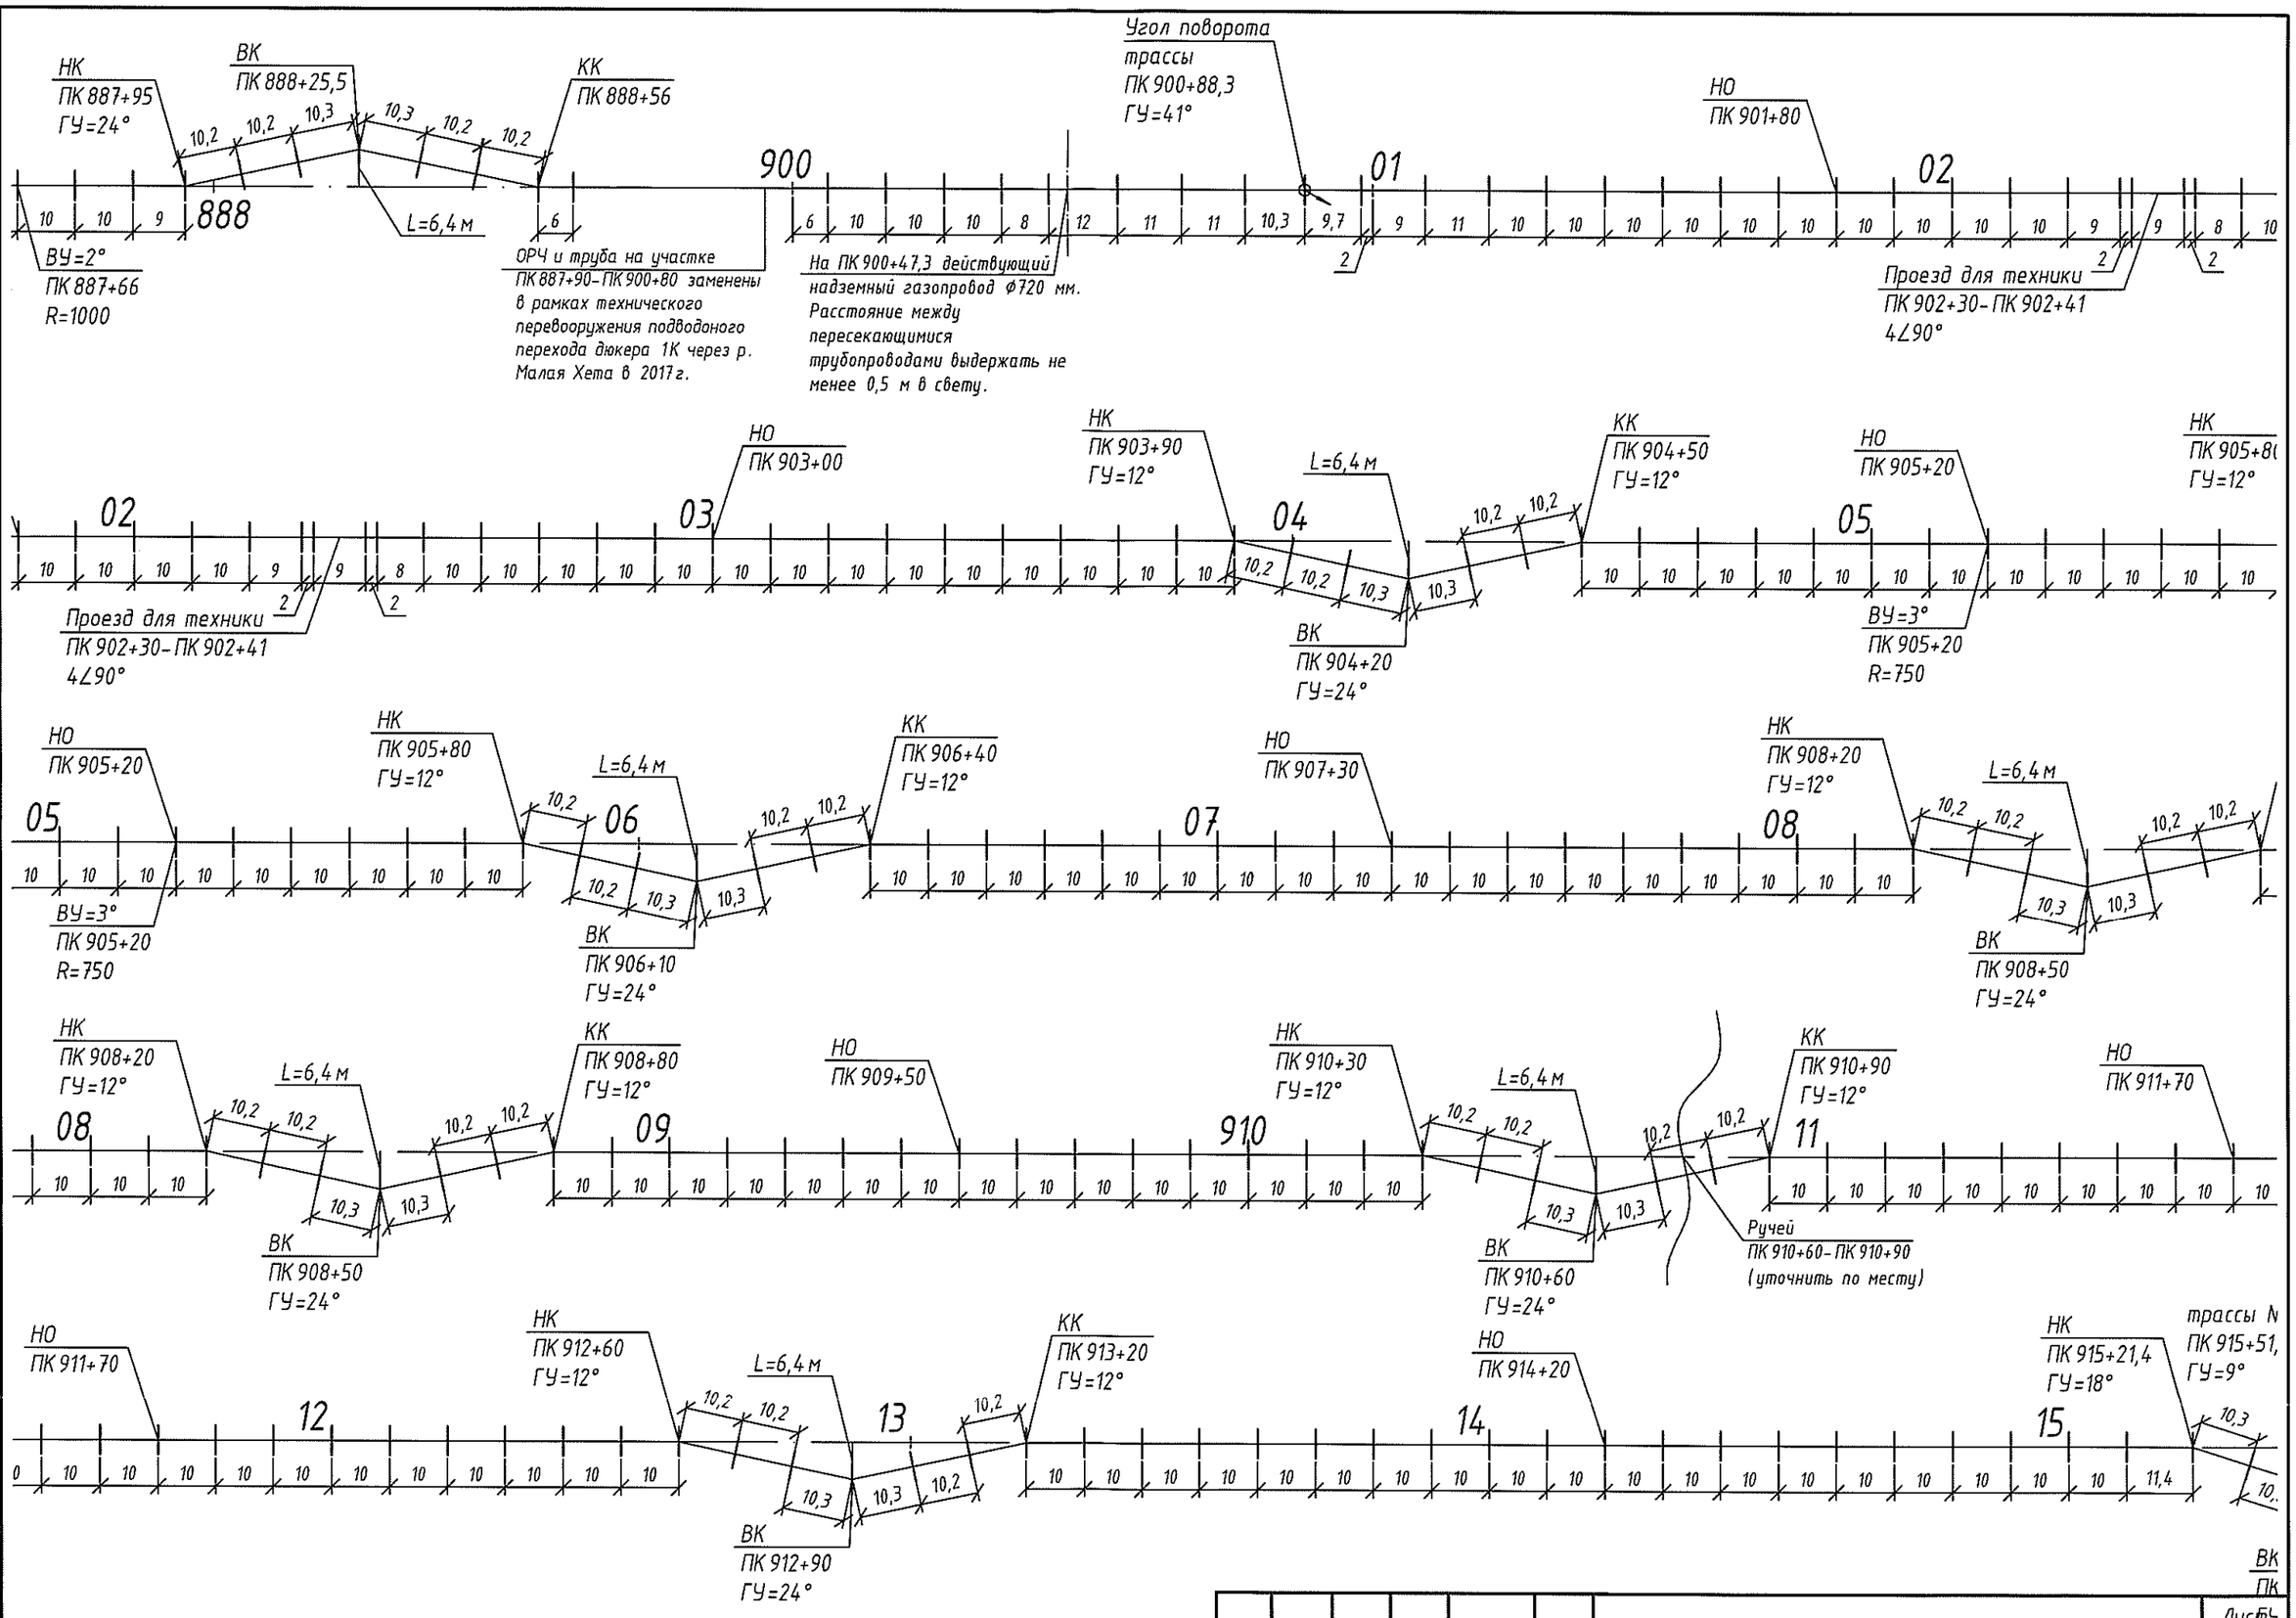
НК
ПК 887+95
ГУ=24°
ВК
ПК 888+25,5
КК
ПК 888+56
10,2 10,2 10,3 10,3 10,2 10,2
10 10 9
888
L=6,4 м
6
ВУ=2°
ПК 887+66
R=1000
ОРЧ и труба на участке ПК 887+90–ПК 900+80 заменены в рамках технического перевооружения подводного перехода дюкера 1К через р. Малая Хета в 2017 г.
900
6 10 10 10 8 12 11 11 10,3 9,7
На ПК 900+47,3 действующий надземный газопровод ф720 мм. Расстояние между пересекающимися трубопроводами выдержать не менее 0,5 м в свету.
Угол поворота трассы
ПК 900+88,3
ГУ=41°
01
2
9 11 10 10 10 10 10 10 10 10 10 10 9 9 8 10
НО
ПК 901+80
02
2
2
Проезд для техники
ПК 902+30–ПК 902+41
4∠90°
02
10 10 10 10 9 9 8 10 10 10 10 10 10 10 10 10 10

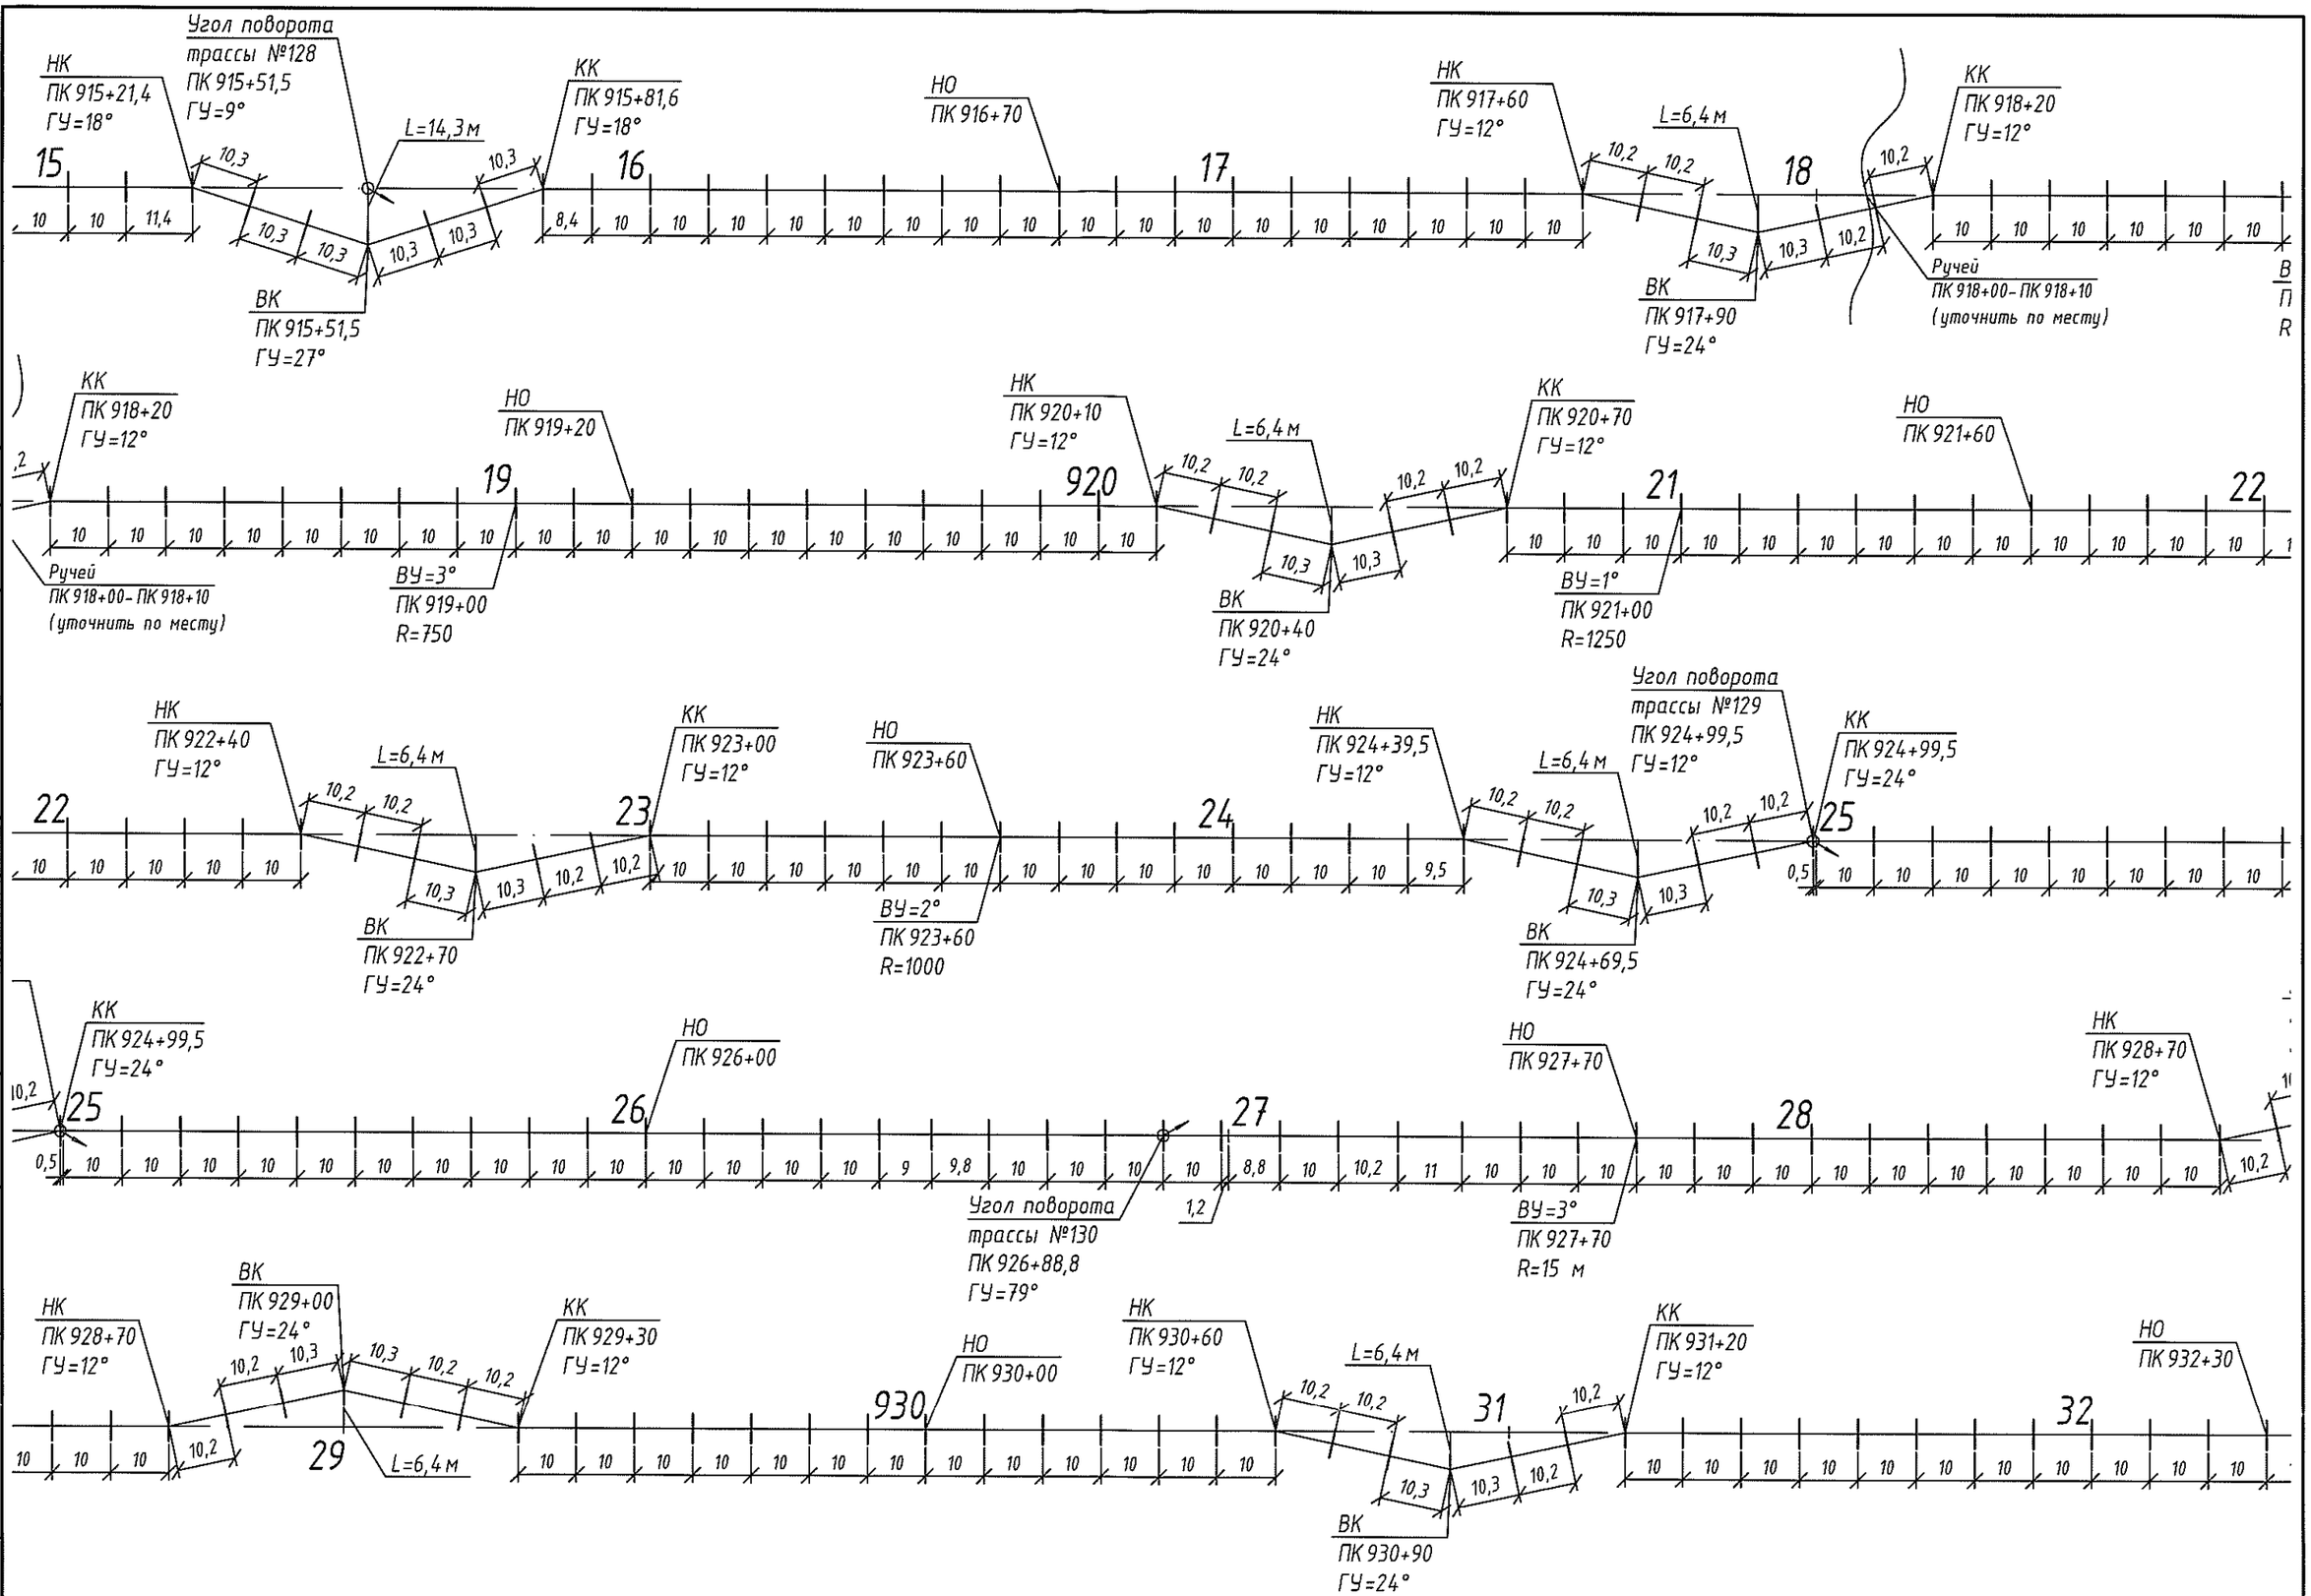

Согласовано

Взам.инв.N

Подпись и дата


Инв.N подл.

Изм.	Кол.уч.	Лист	N док.	Подпись	Дата

III-Д-101/3103-КМ.Л2

Лист 4

Формат А3

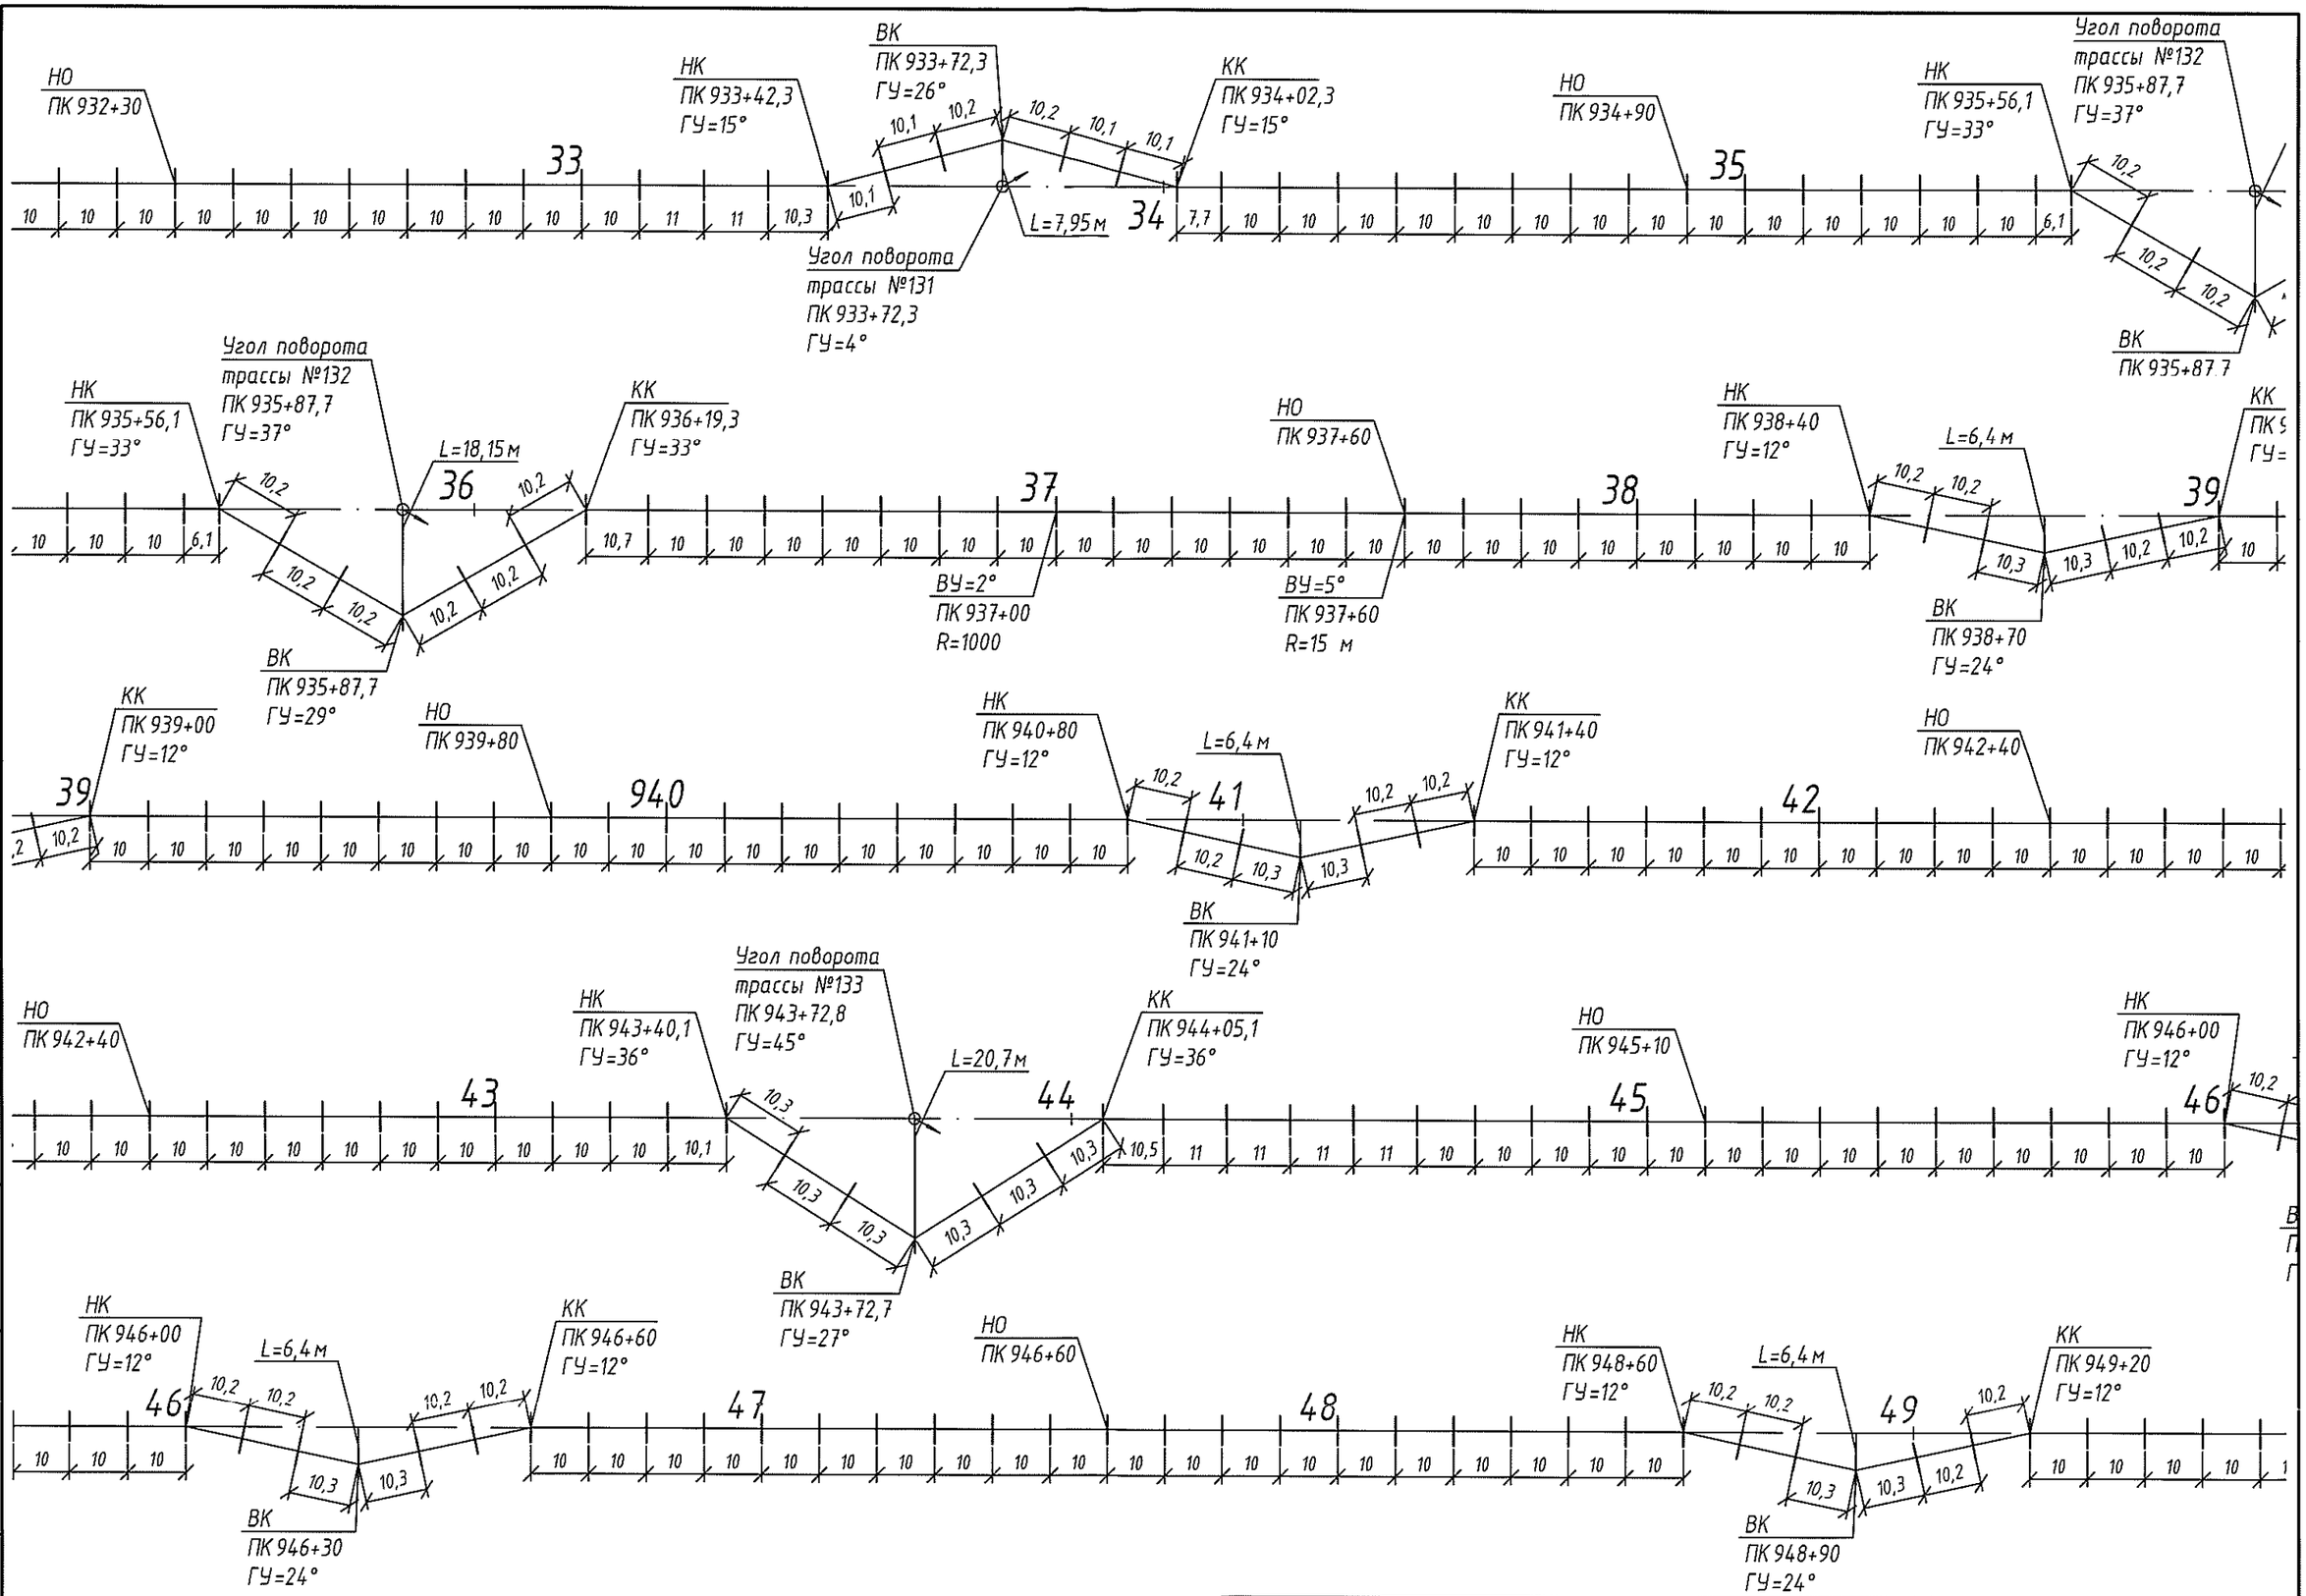

Согласовано

Взам.инв.N

Подпись и дата


Инв.N подл.

Изм.	Кол.уч.	Лист	N док.	Подпись	Дата

III-Д-101/3103-КМ.Л2

Лист 5

Формат А3

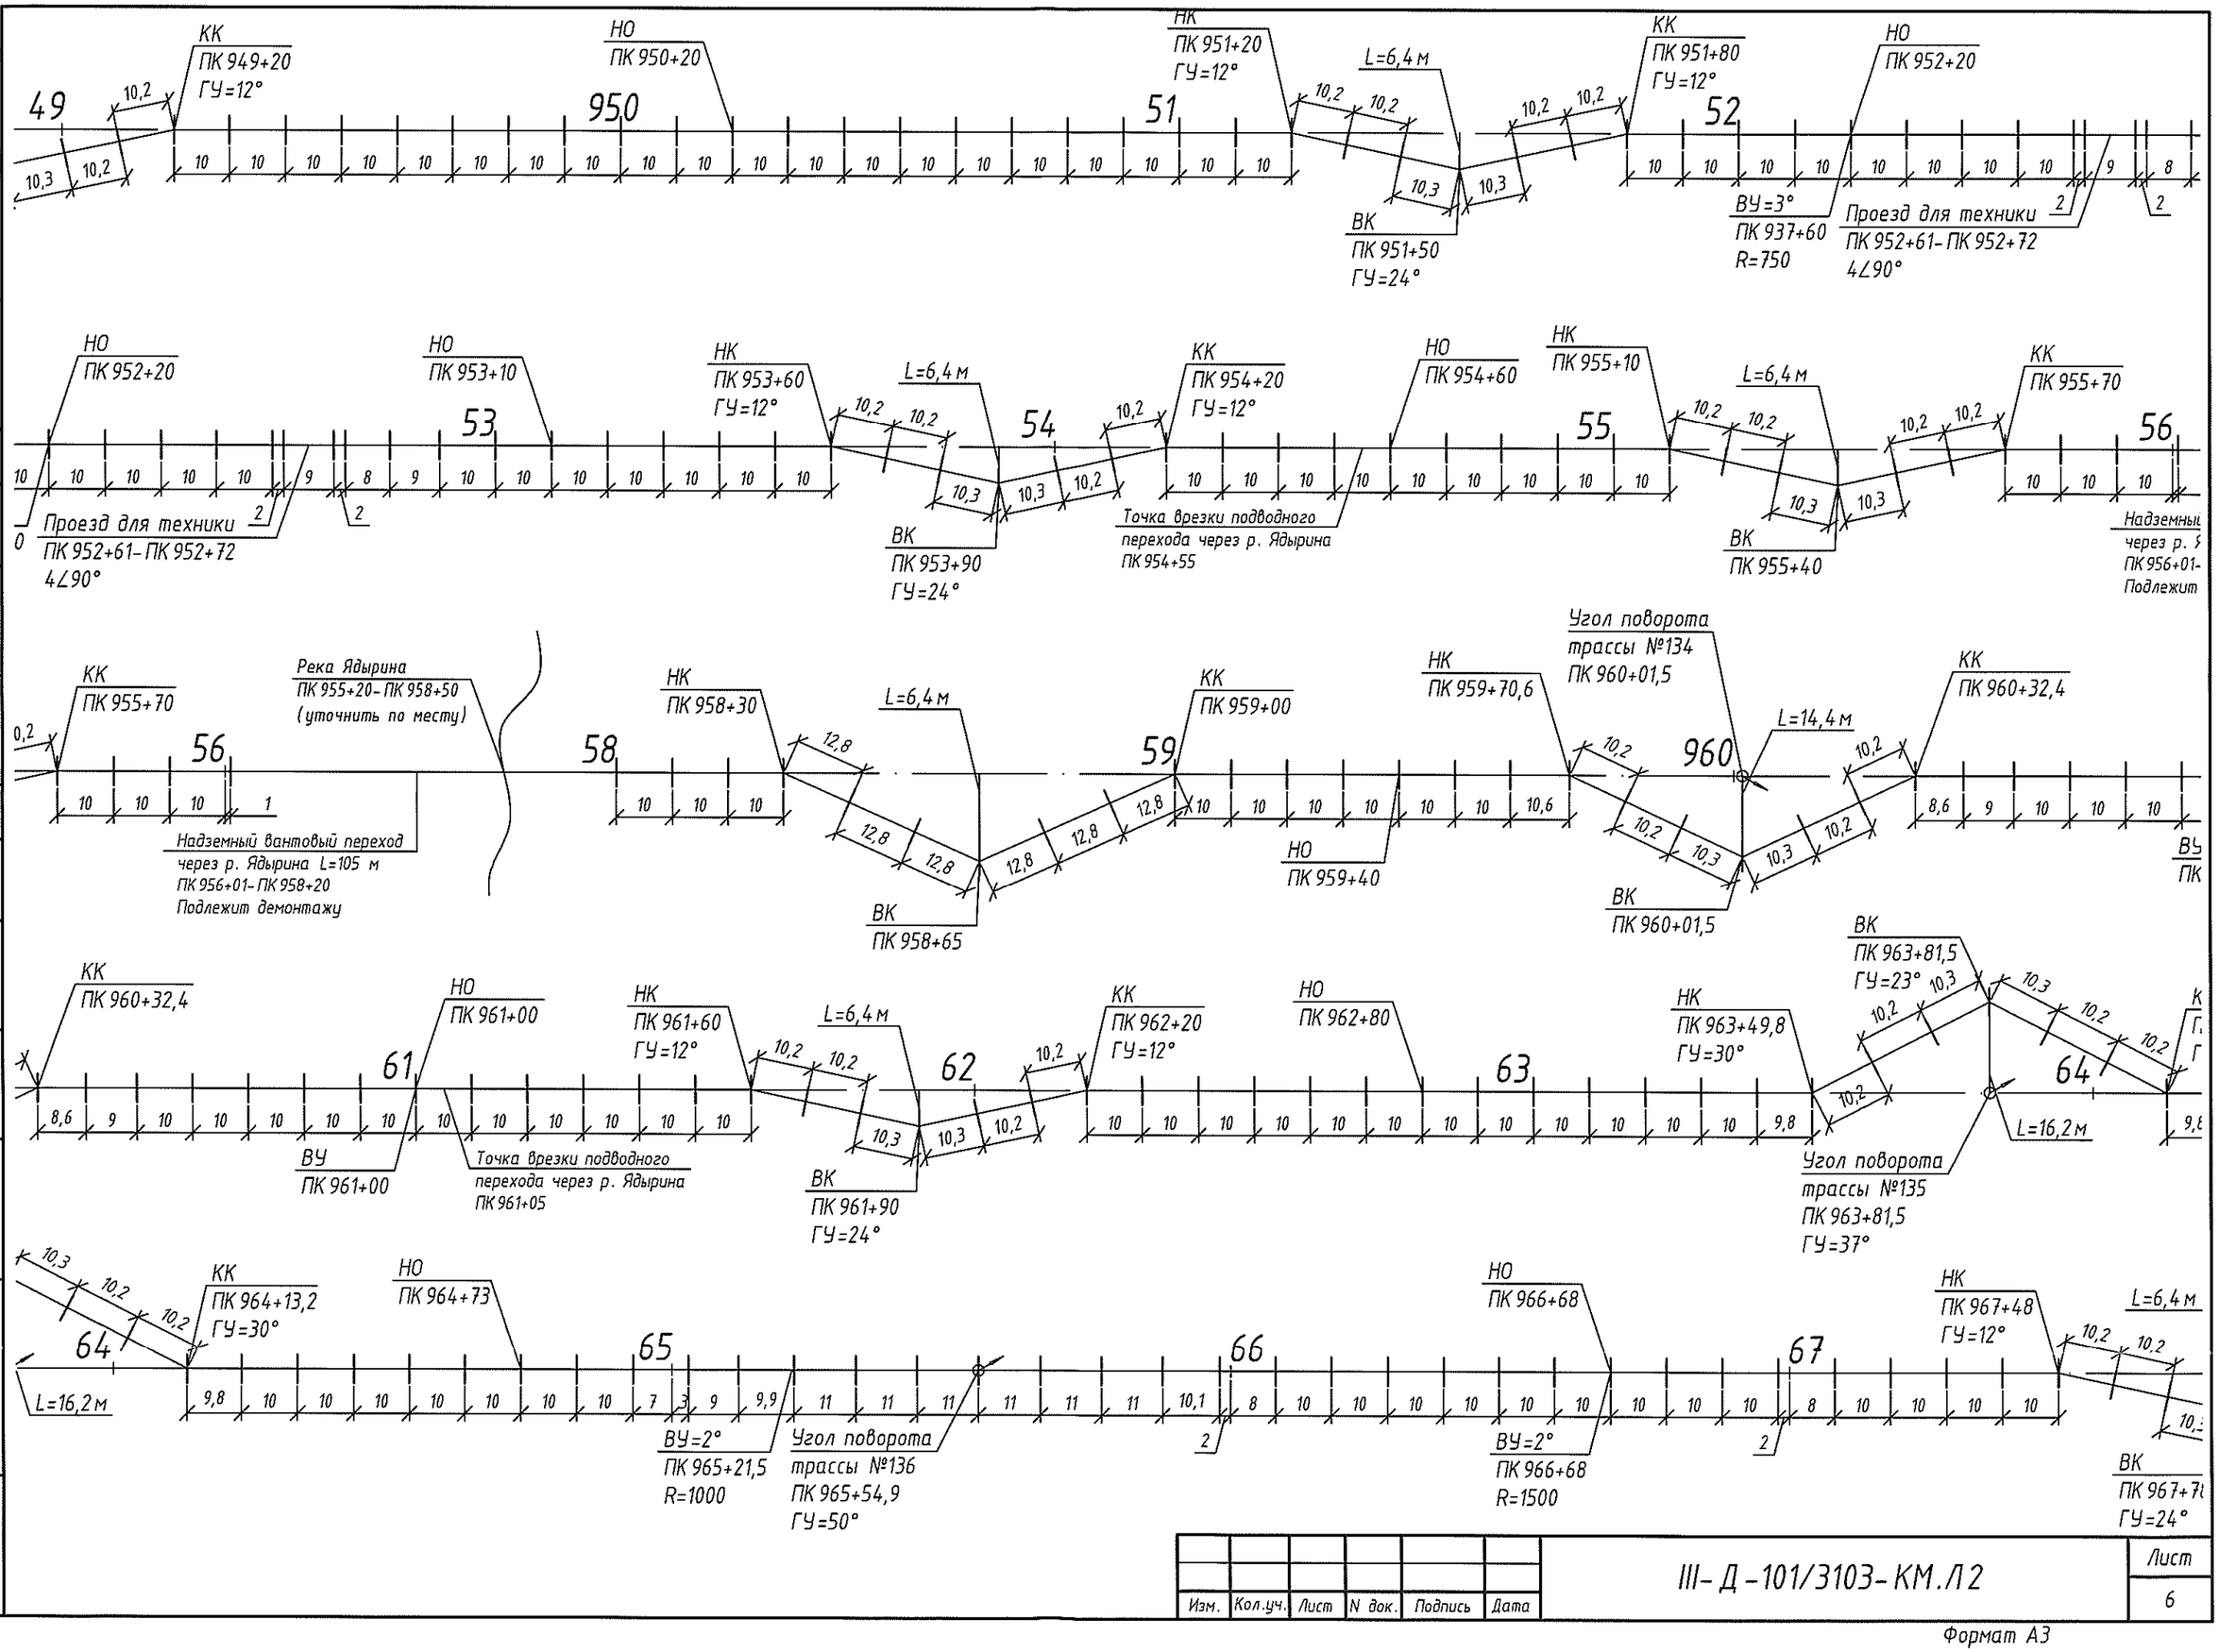

Согласовано

Взам.инв.N

Подпись и дата


Инв.N подл.

Изм.	Кол.уч.	Лист	N док.	Подпись	Дата

III–Д–101/3103–КМ.Л2

Лист 6

Формат А3

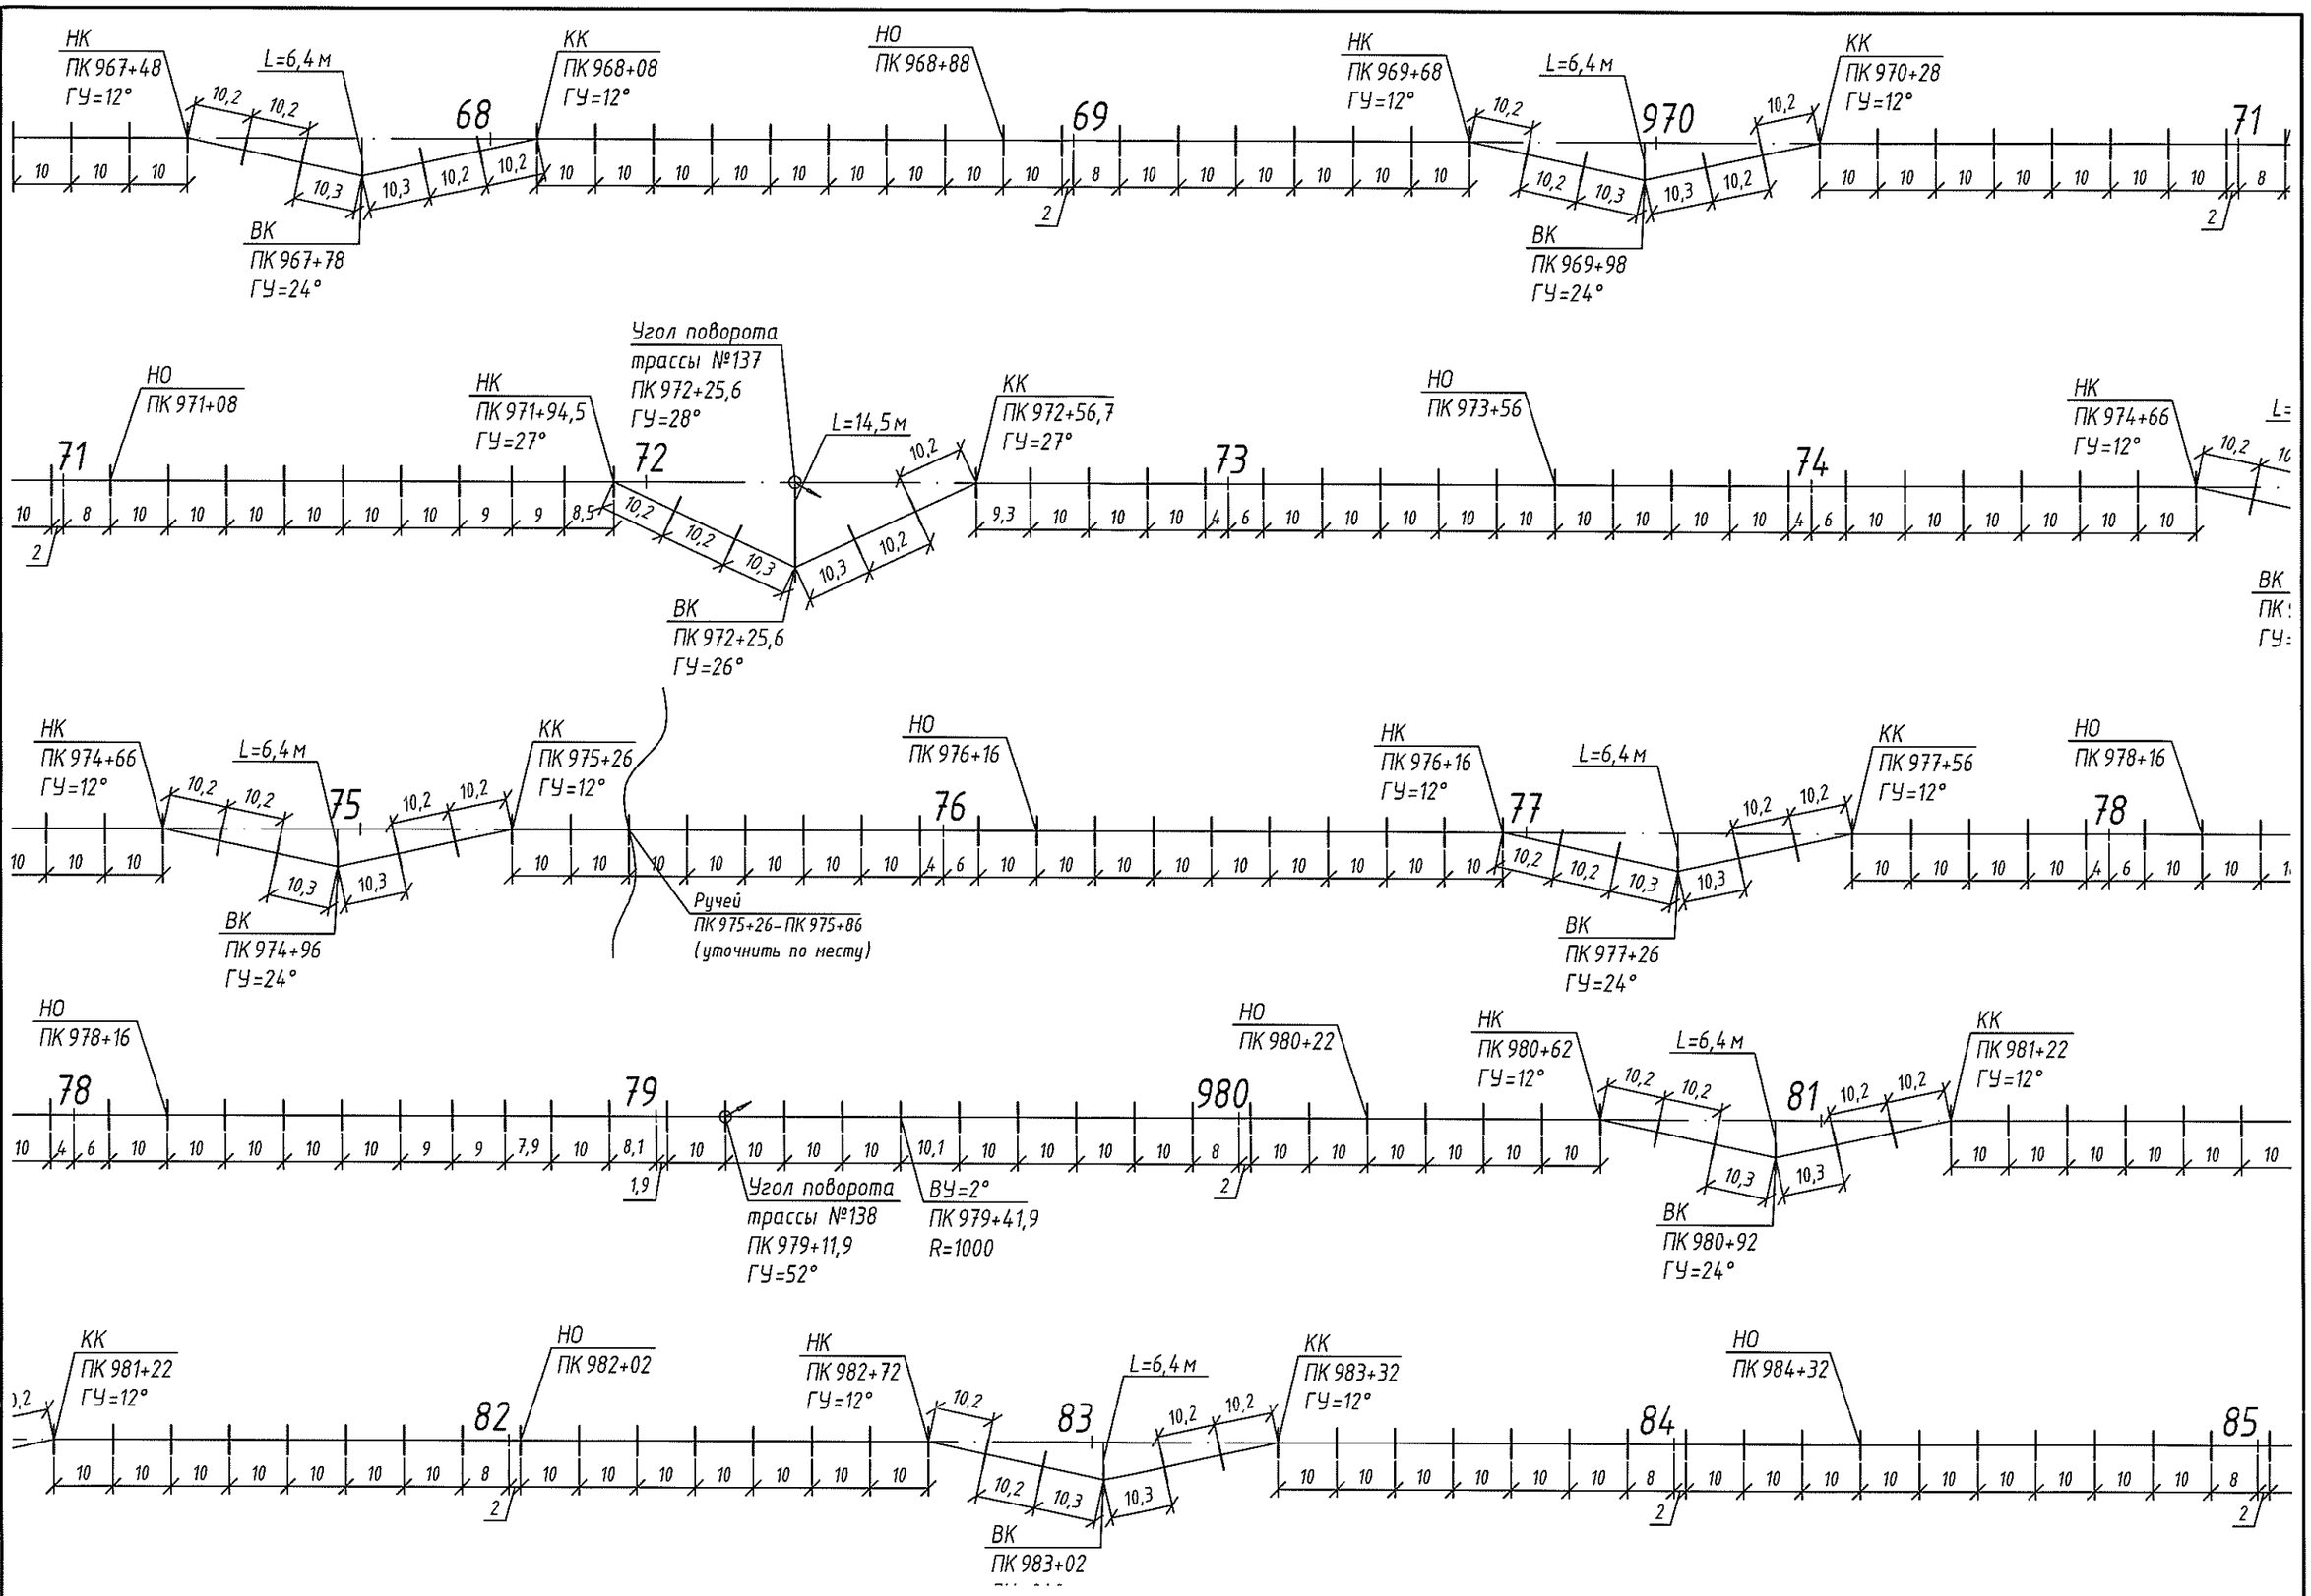

Согласовано

Взам.инв.N

Подпись и дата


Инв.N подл.

Изм.	Кол.уч.	Лист	N док.	Подпись	Дата

III-Д-101/3103-КМ.Л2

Лист 7

Формат А3

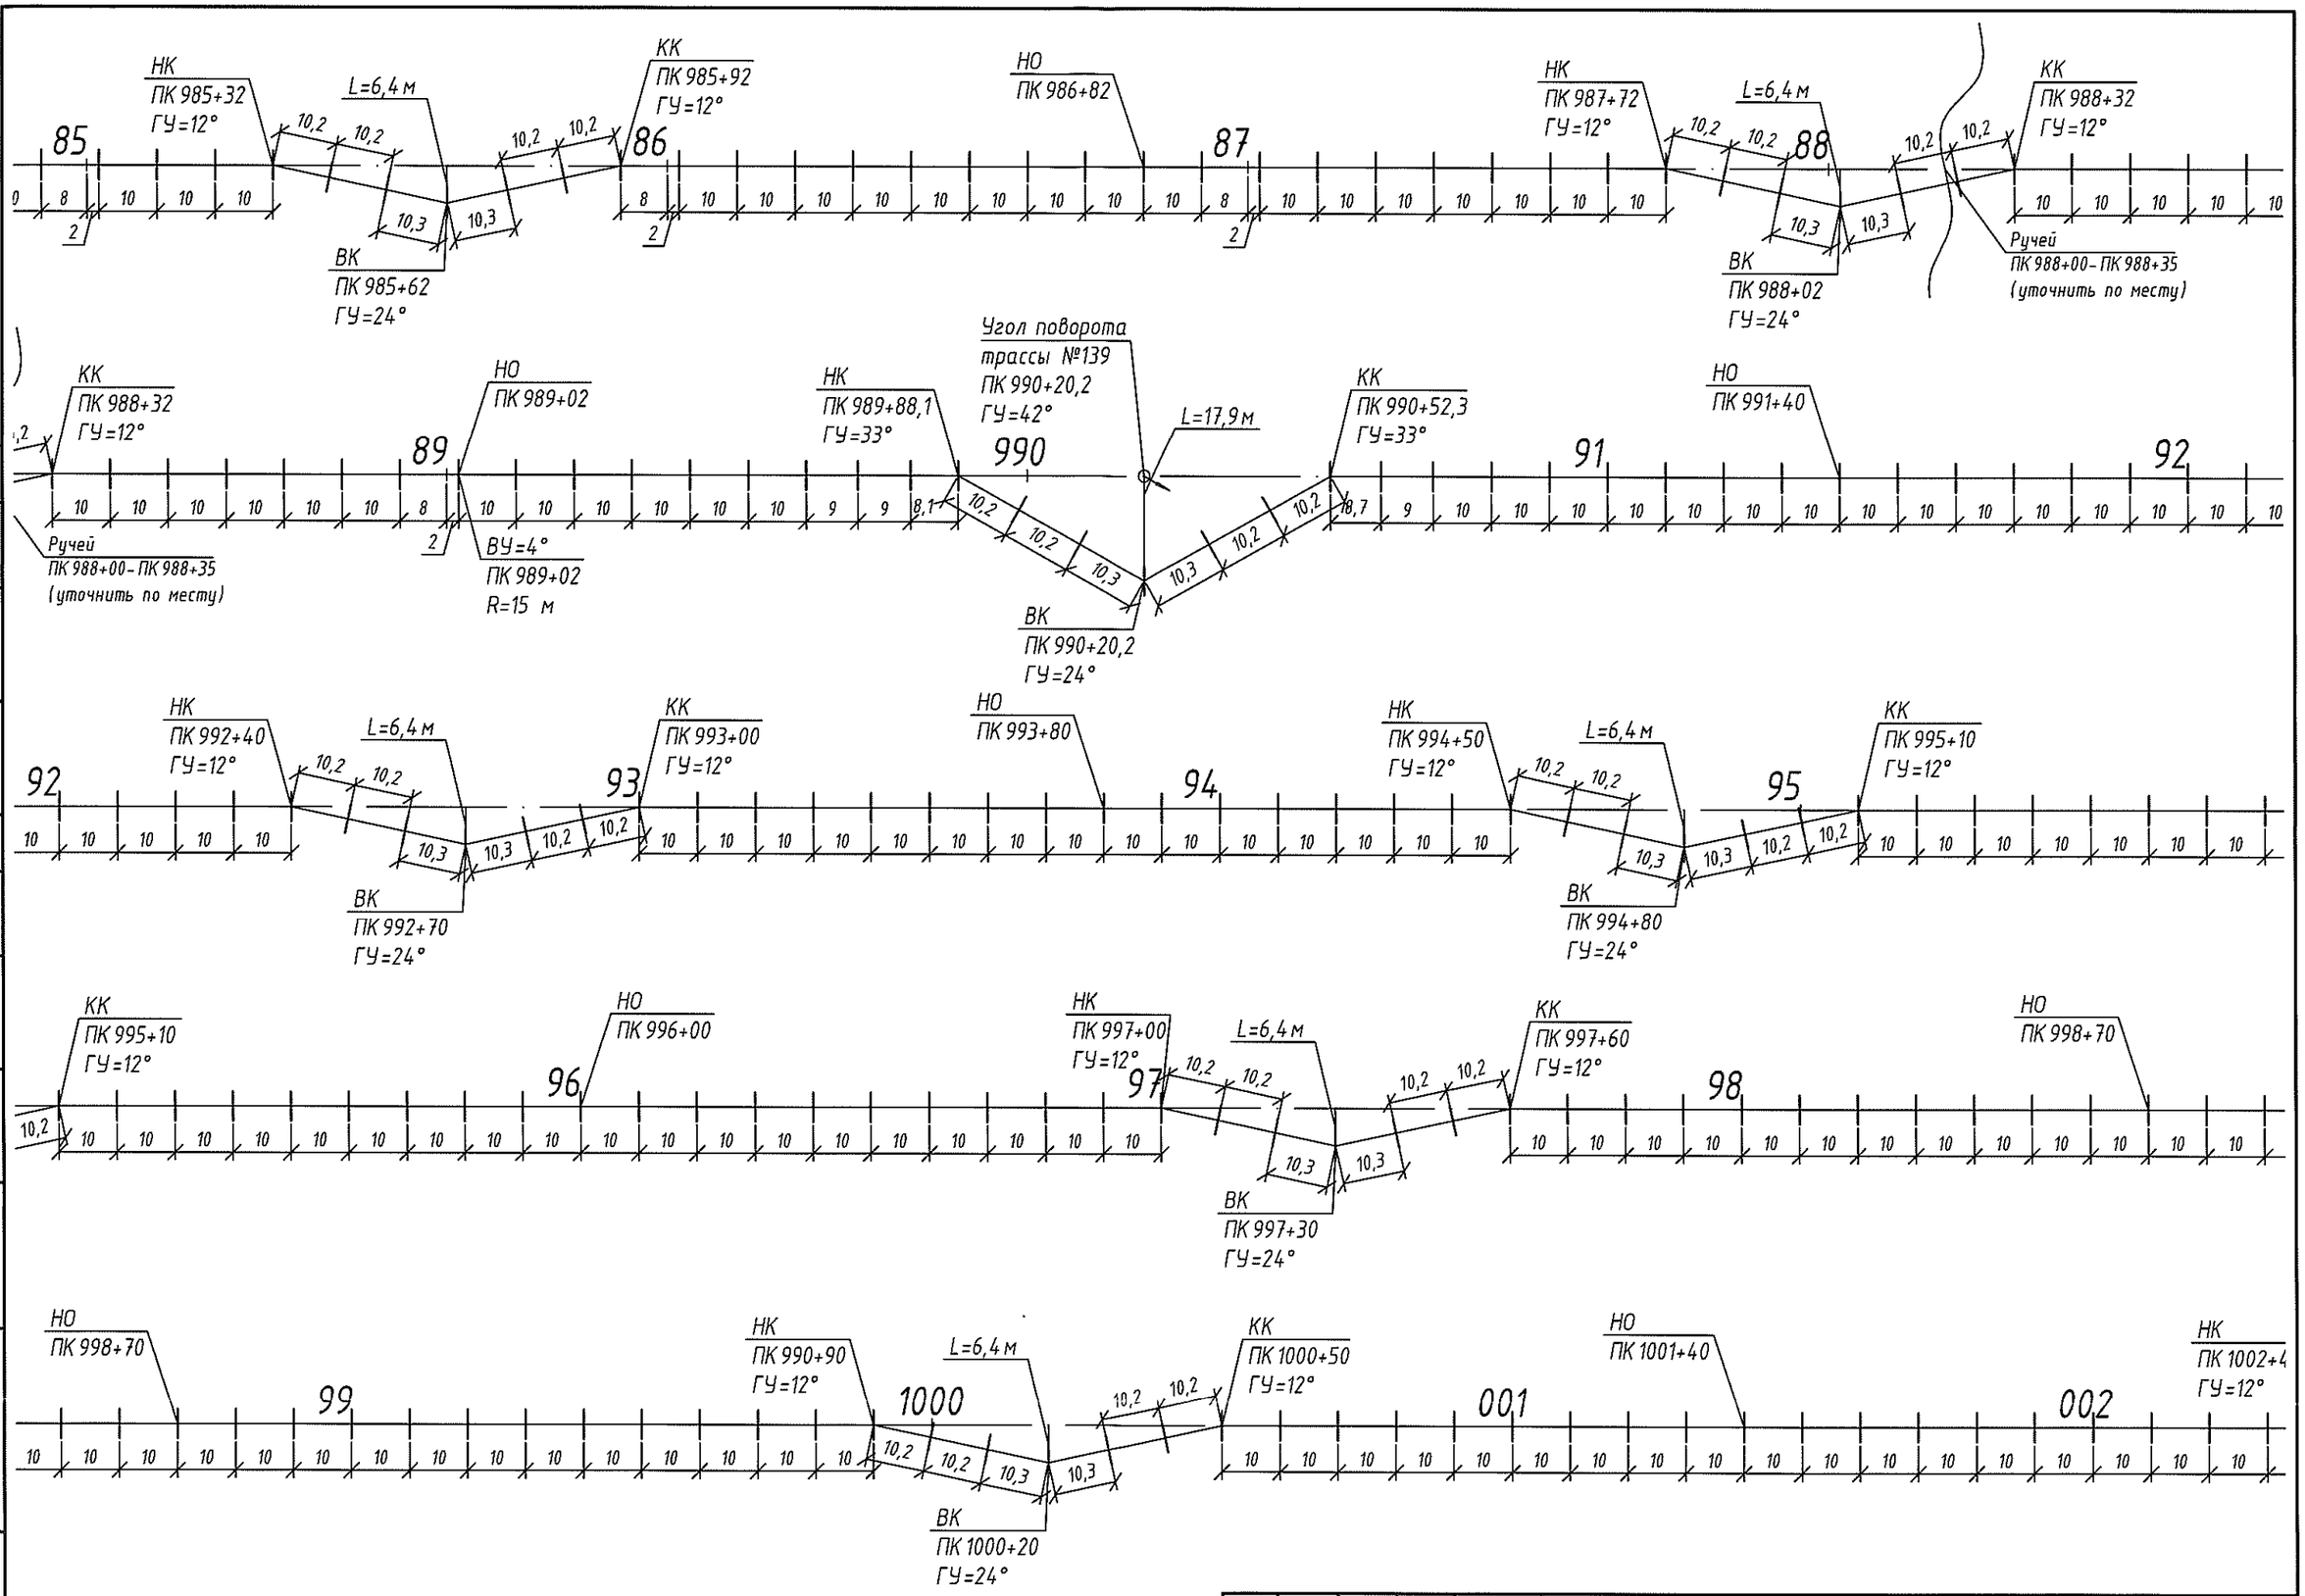

Согласовано

Взам.инв.N

Подпись и дата


Инв.N подл.

Изм.	Кол.уч.	Лист	N док.	Подпись	Дата

III–Д–101/3103–КМ.Л2

Лист 8

Формат А3

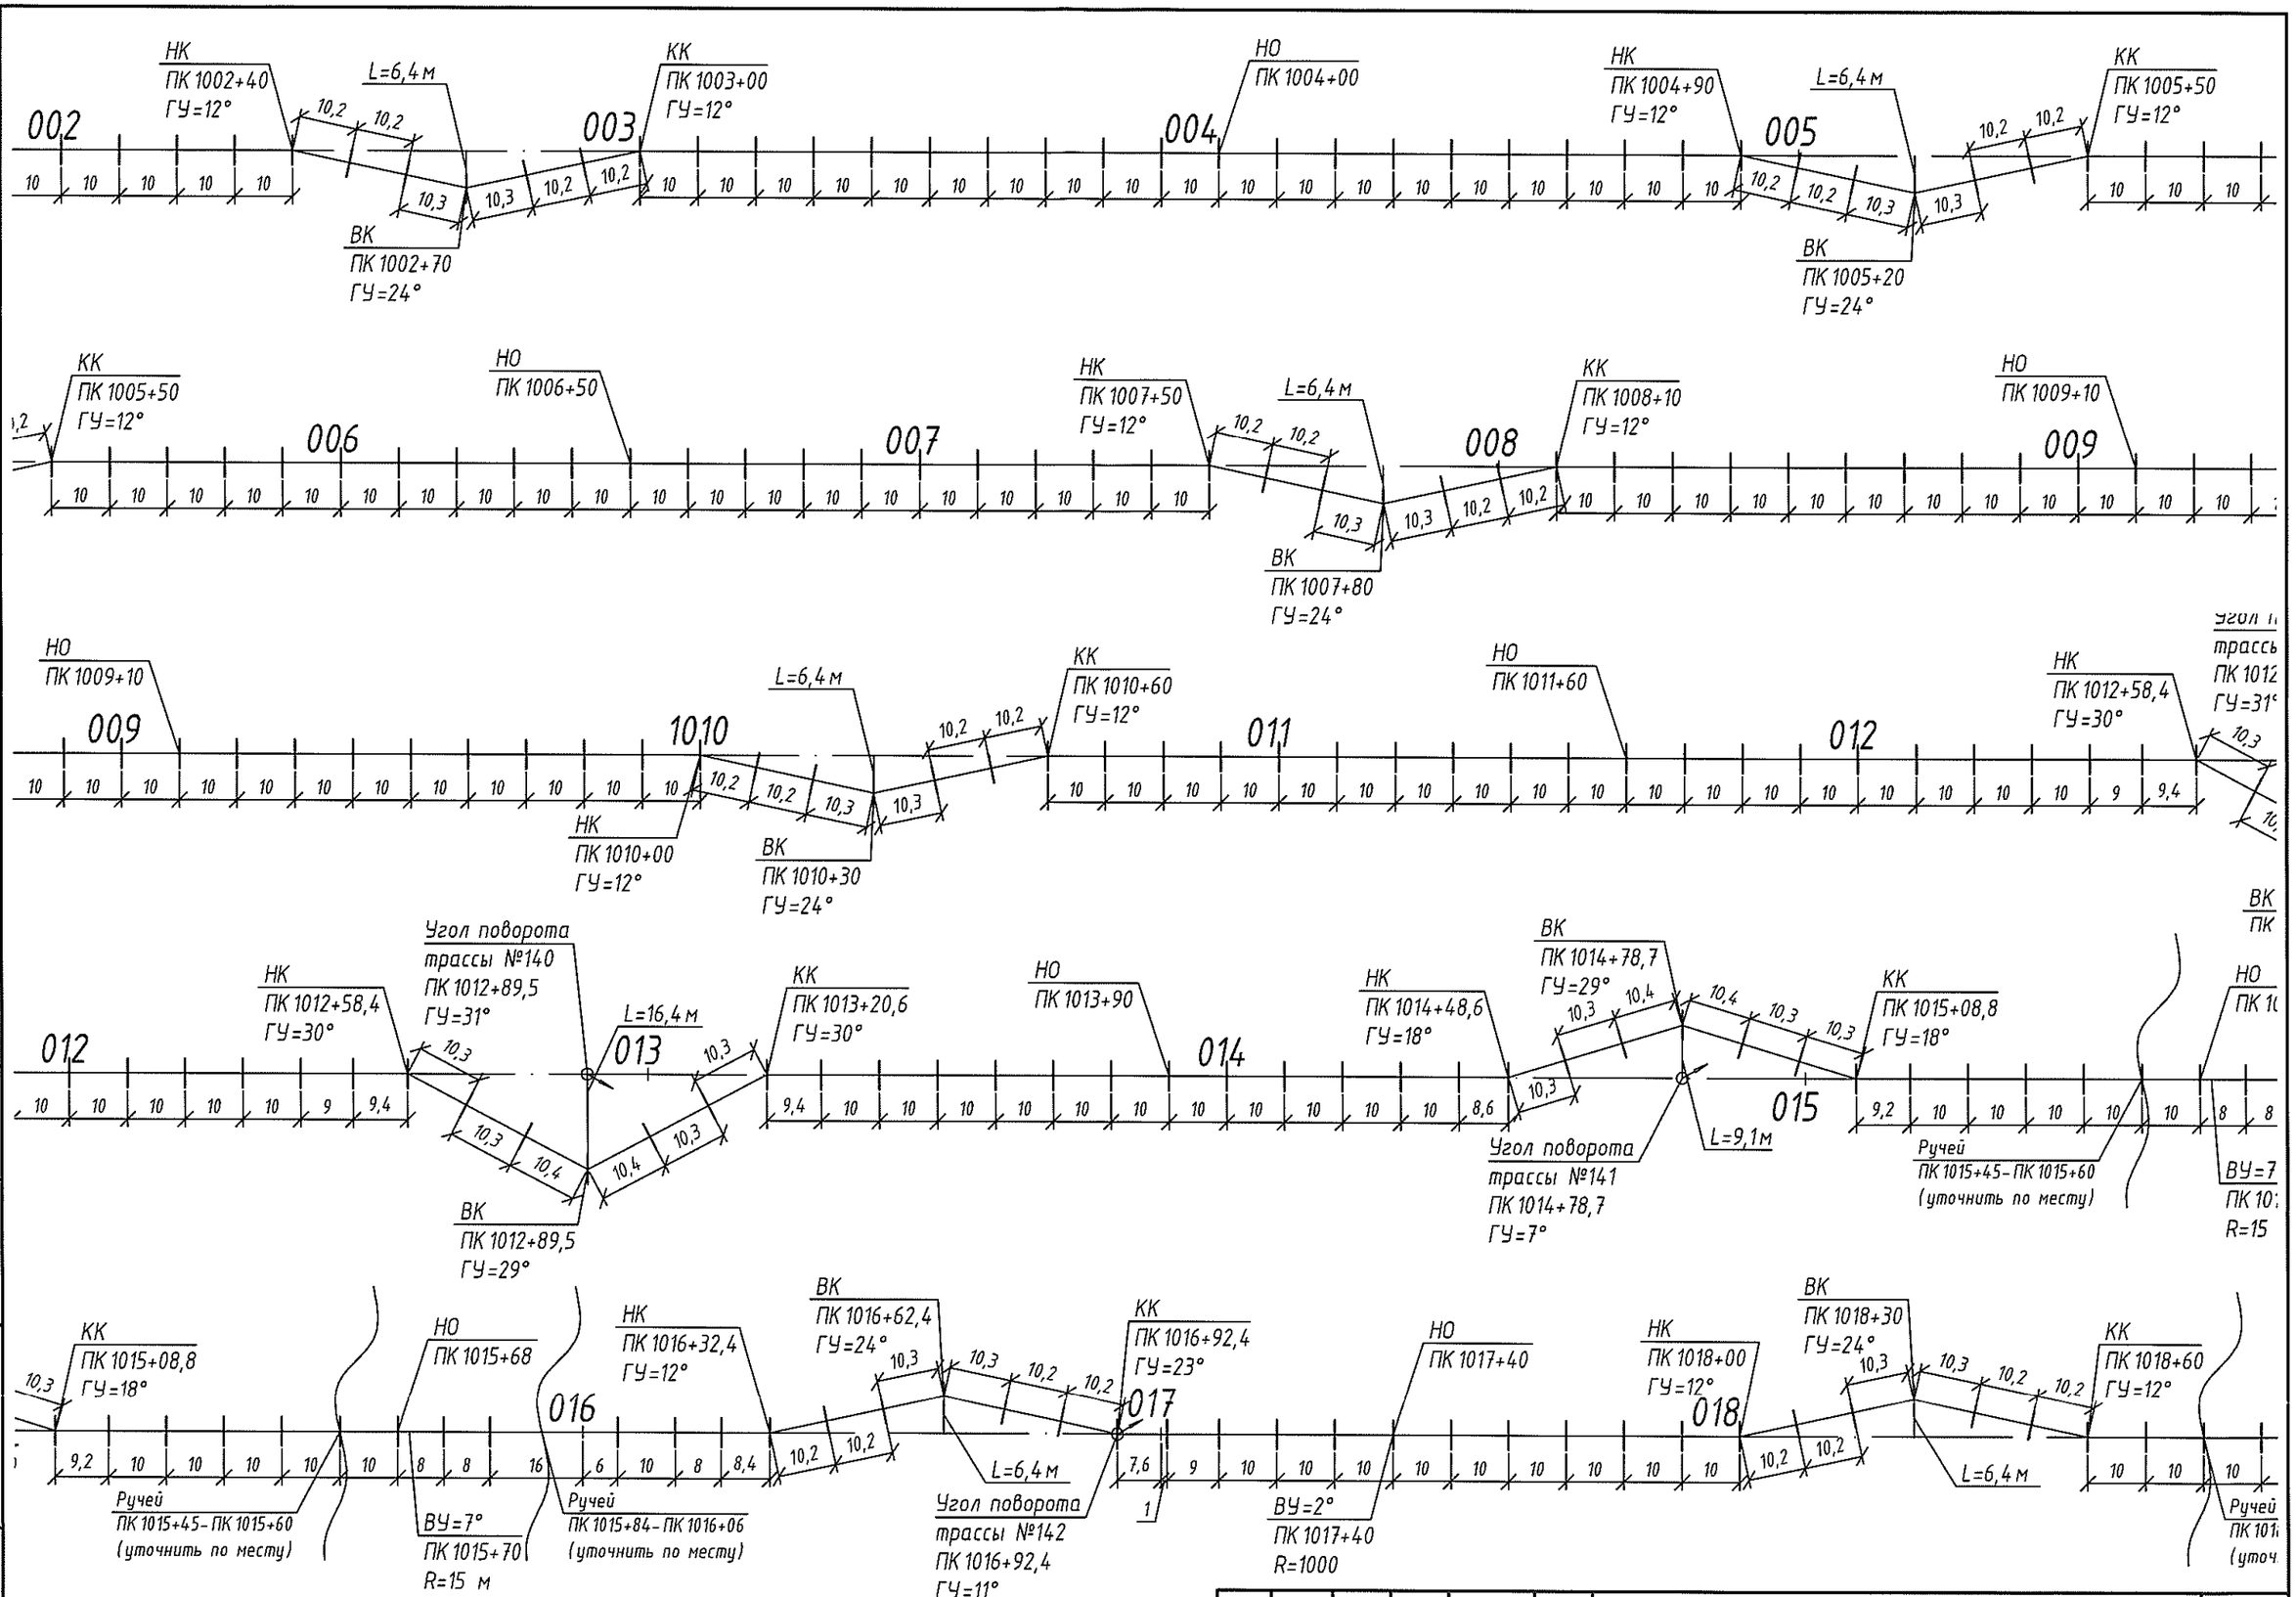

Согласовано

Взам.инв.N

Подпись и дата


Инв.N подл.

Изм.	Кол.уч.	Лист	N док.	Подпись	Дата

III-Д-101/3103-КМ.Л2

Лист 9

Формат А3

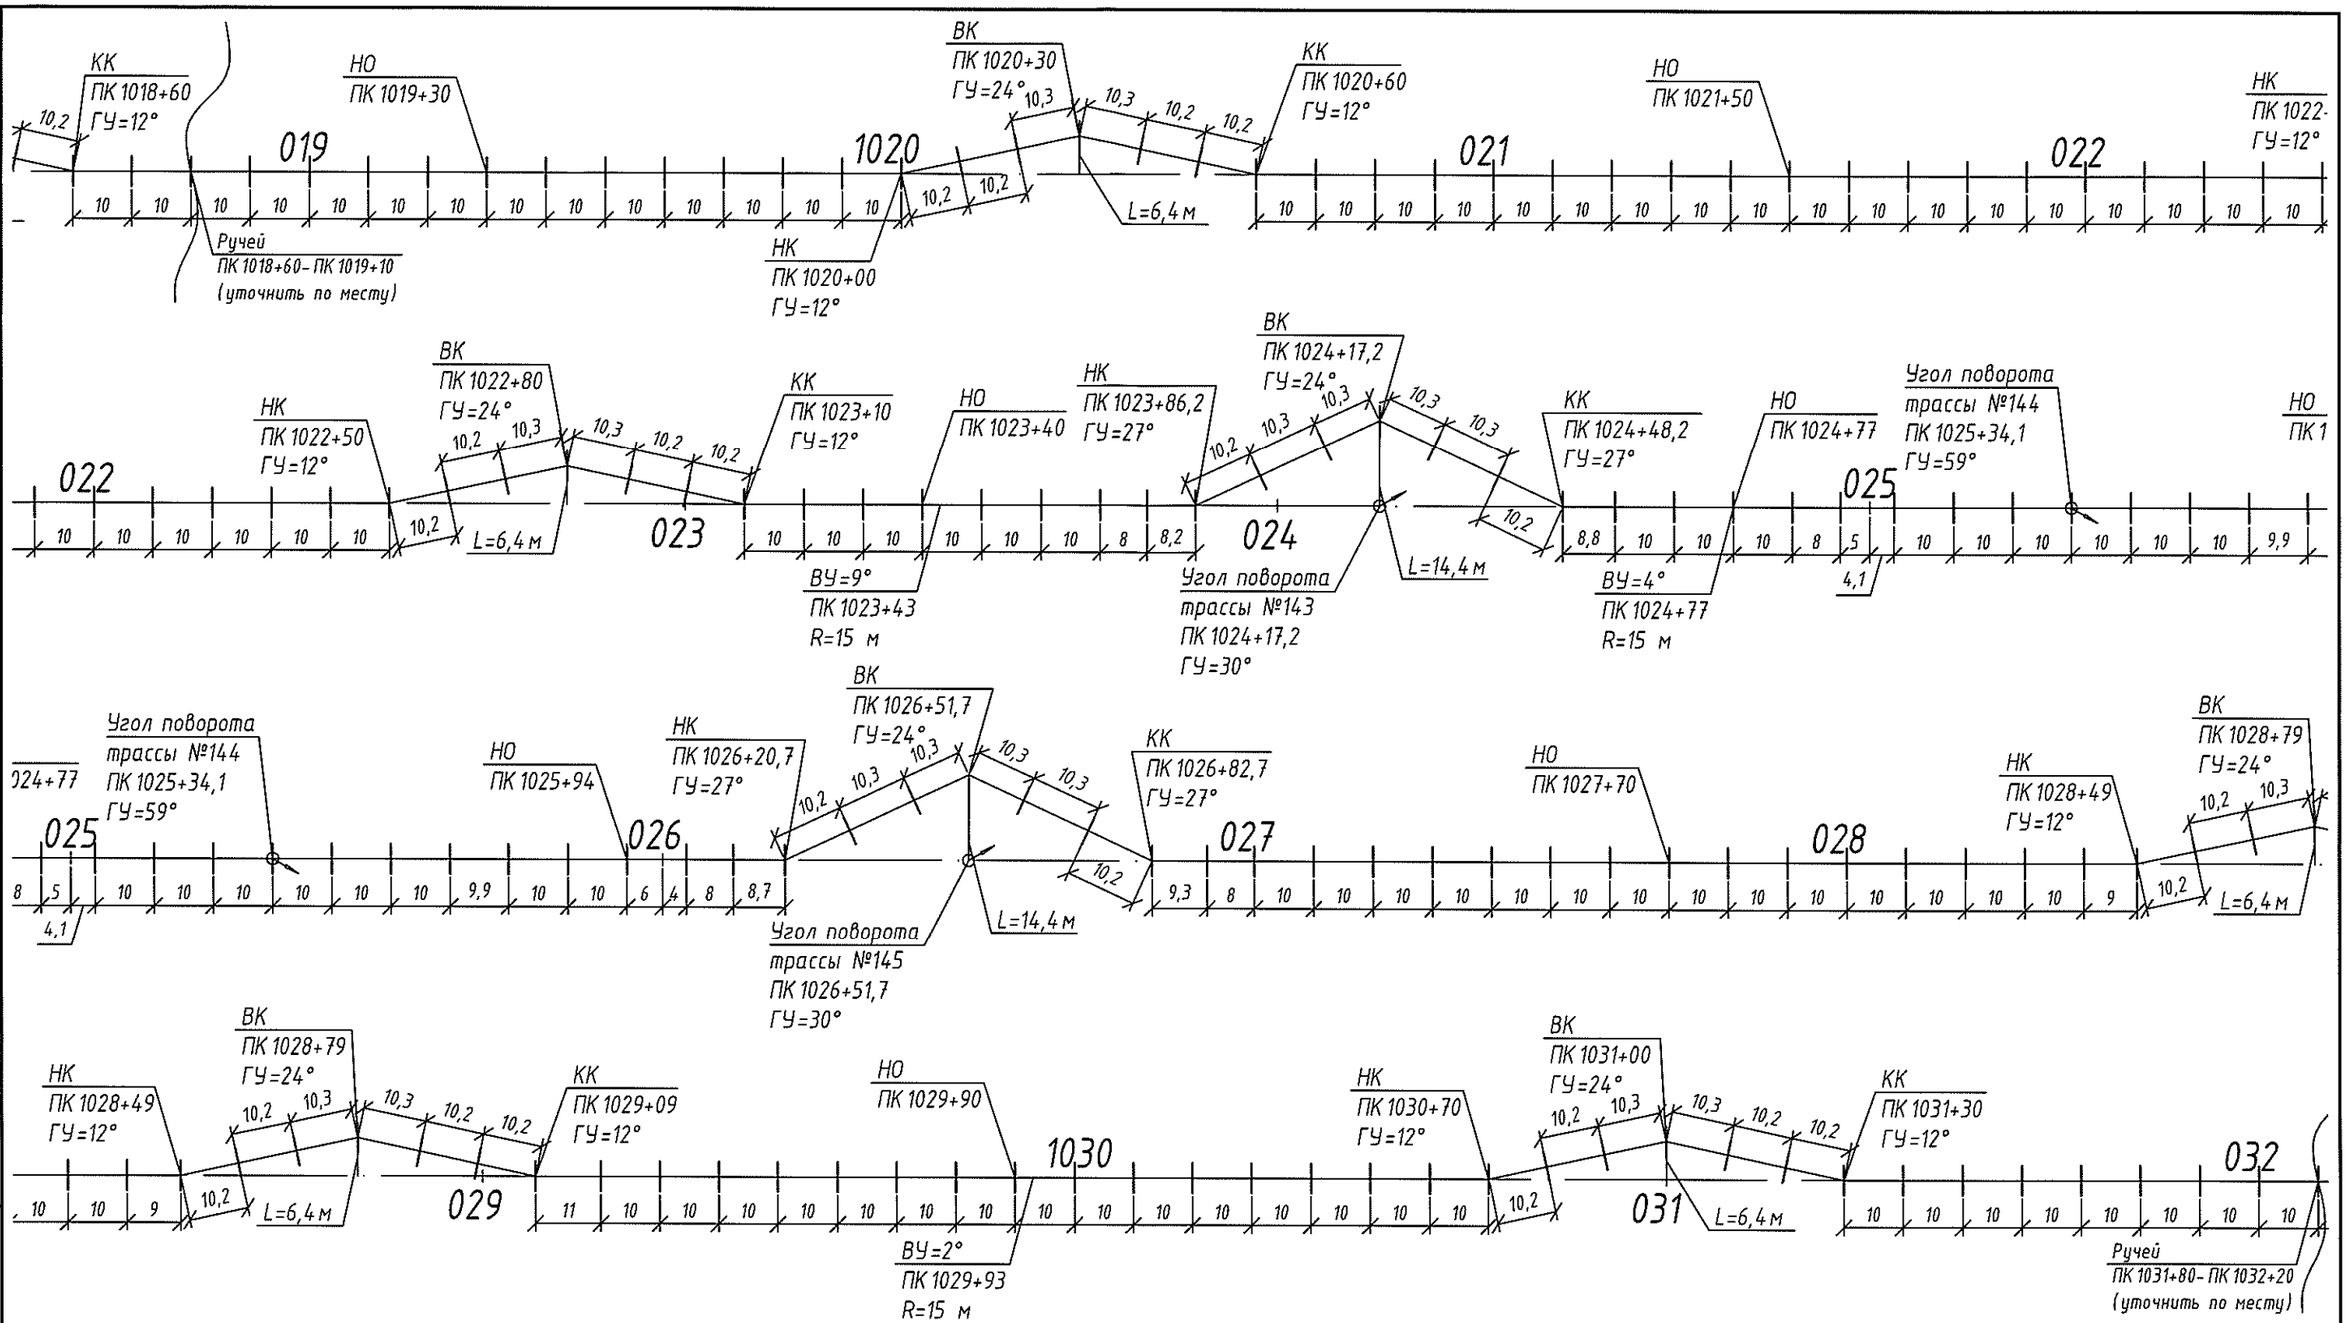

Согласовано

Взам.инв.N

Подпись и дата


Инв.N подл.

Изм.	Кол.уч.	Лист	N док.	Подпись	Дата

III–Д–101/3103–КМ.Л2

Лист 10

Формат А3

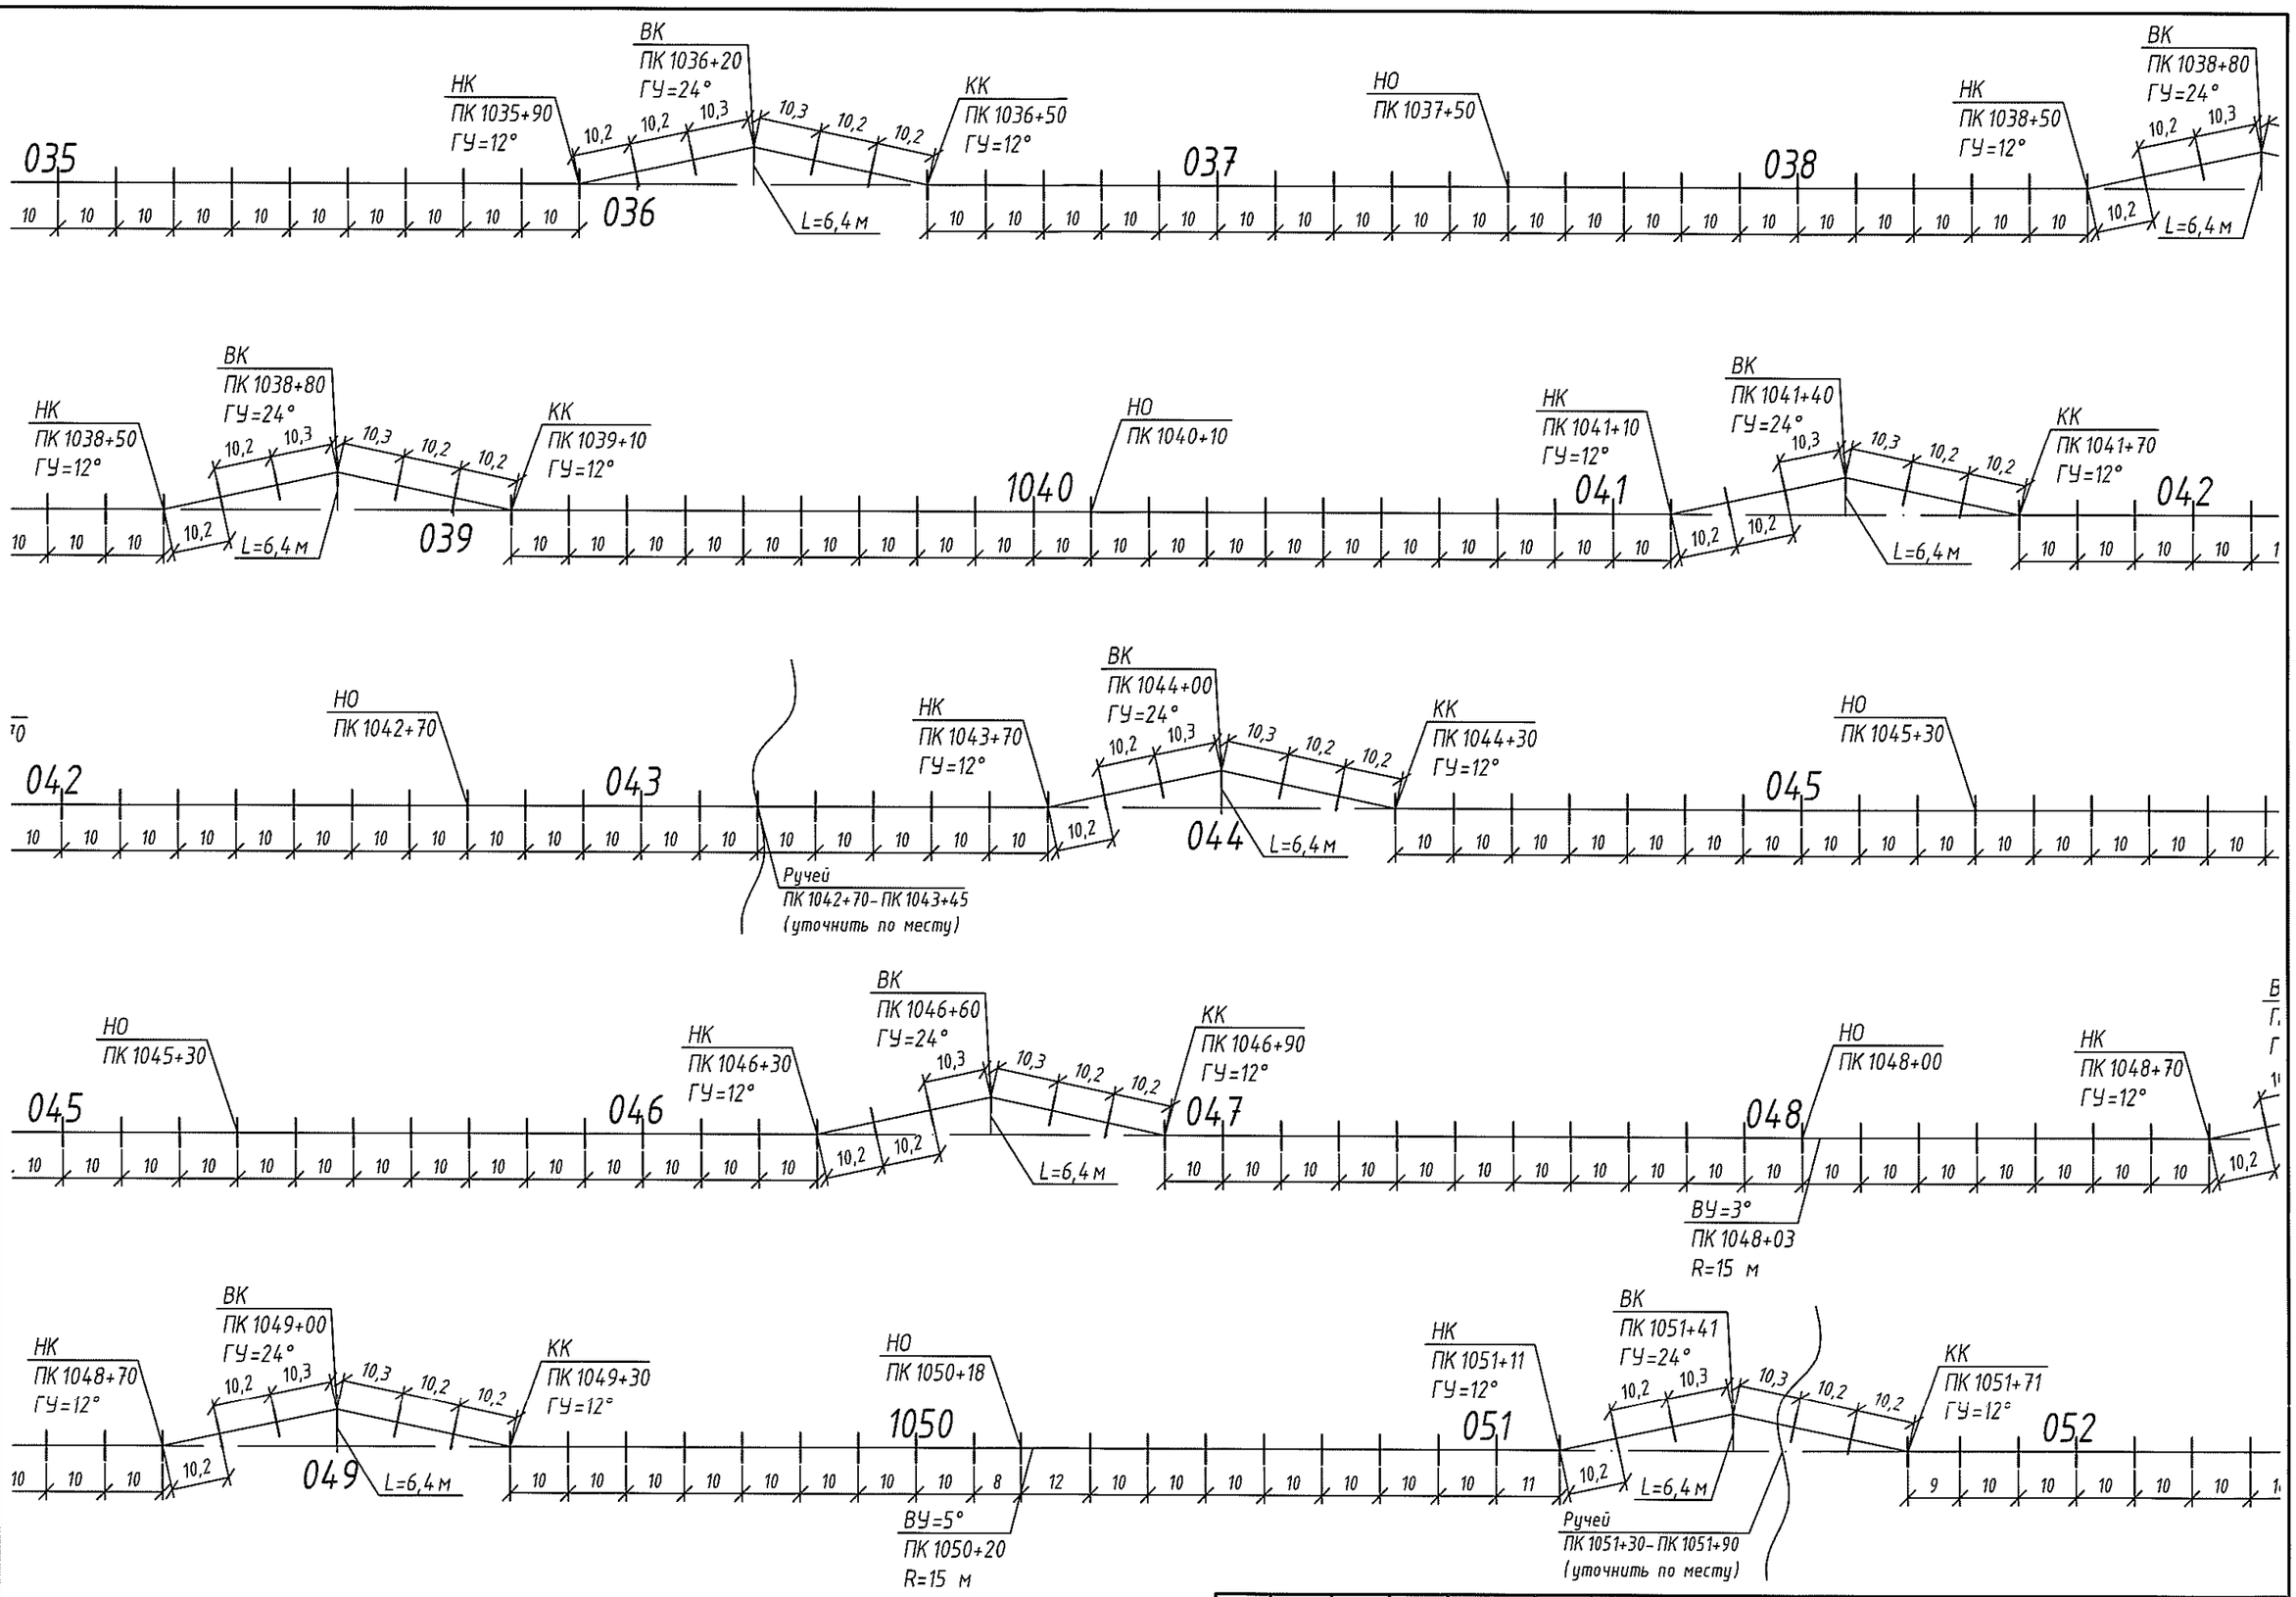

Согласовано


Взам.инв.N

Подпись и дата

Инв.N подл.

Изм.	Кол.уч.	Лист	N док.	Подпись	Дата	III-Д-101/3103-КМ.Л2	Лист 11

Формат А3

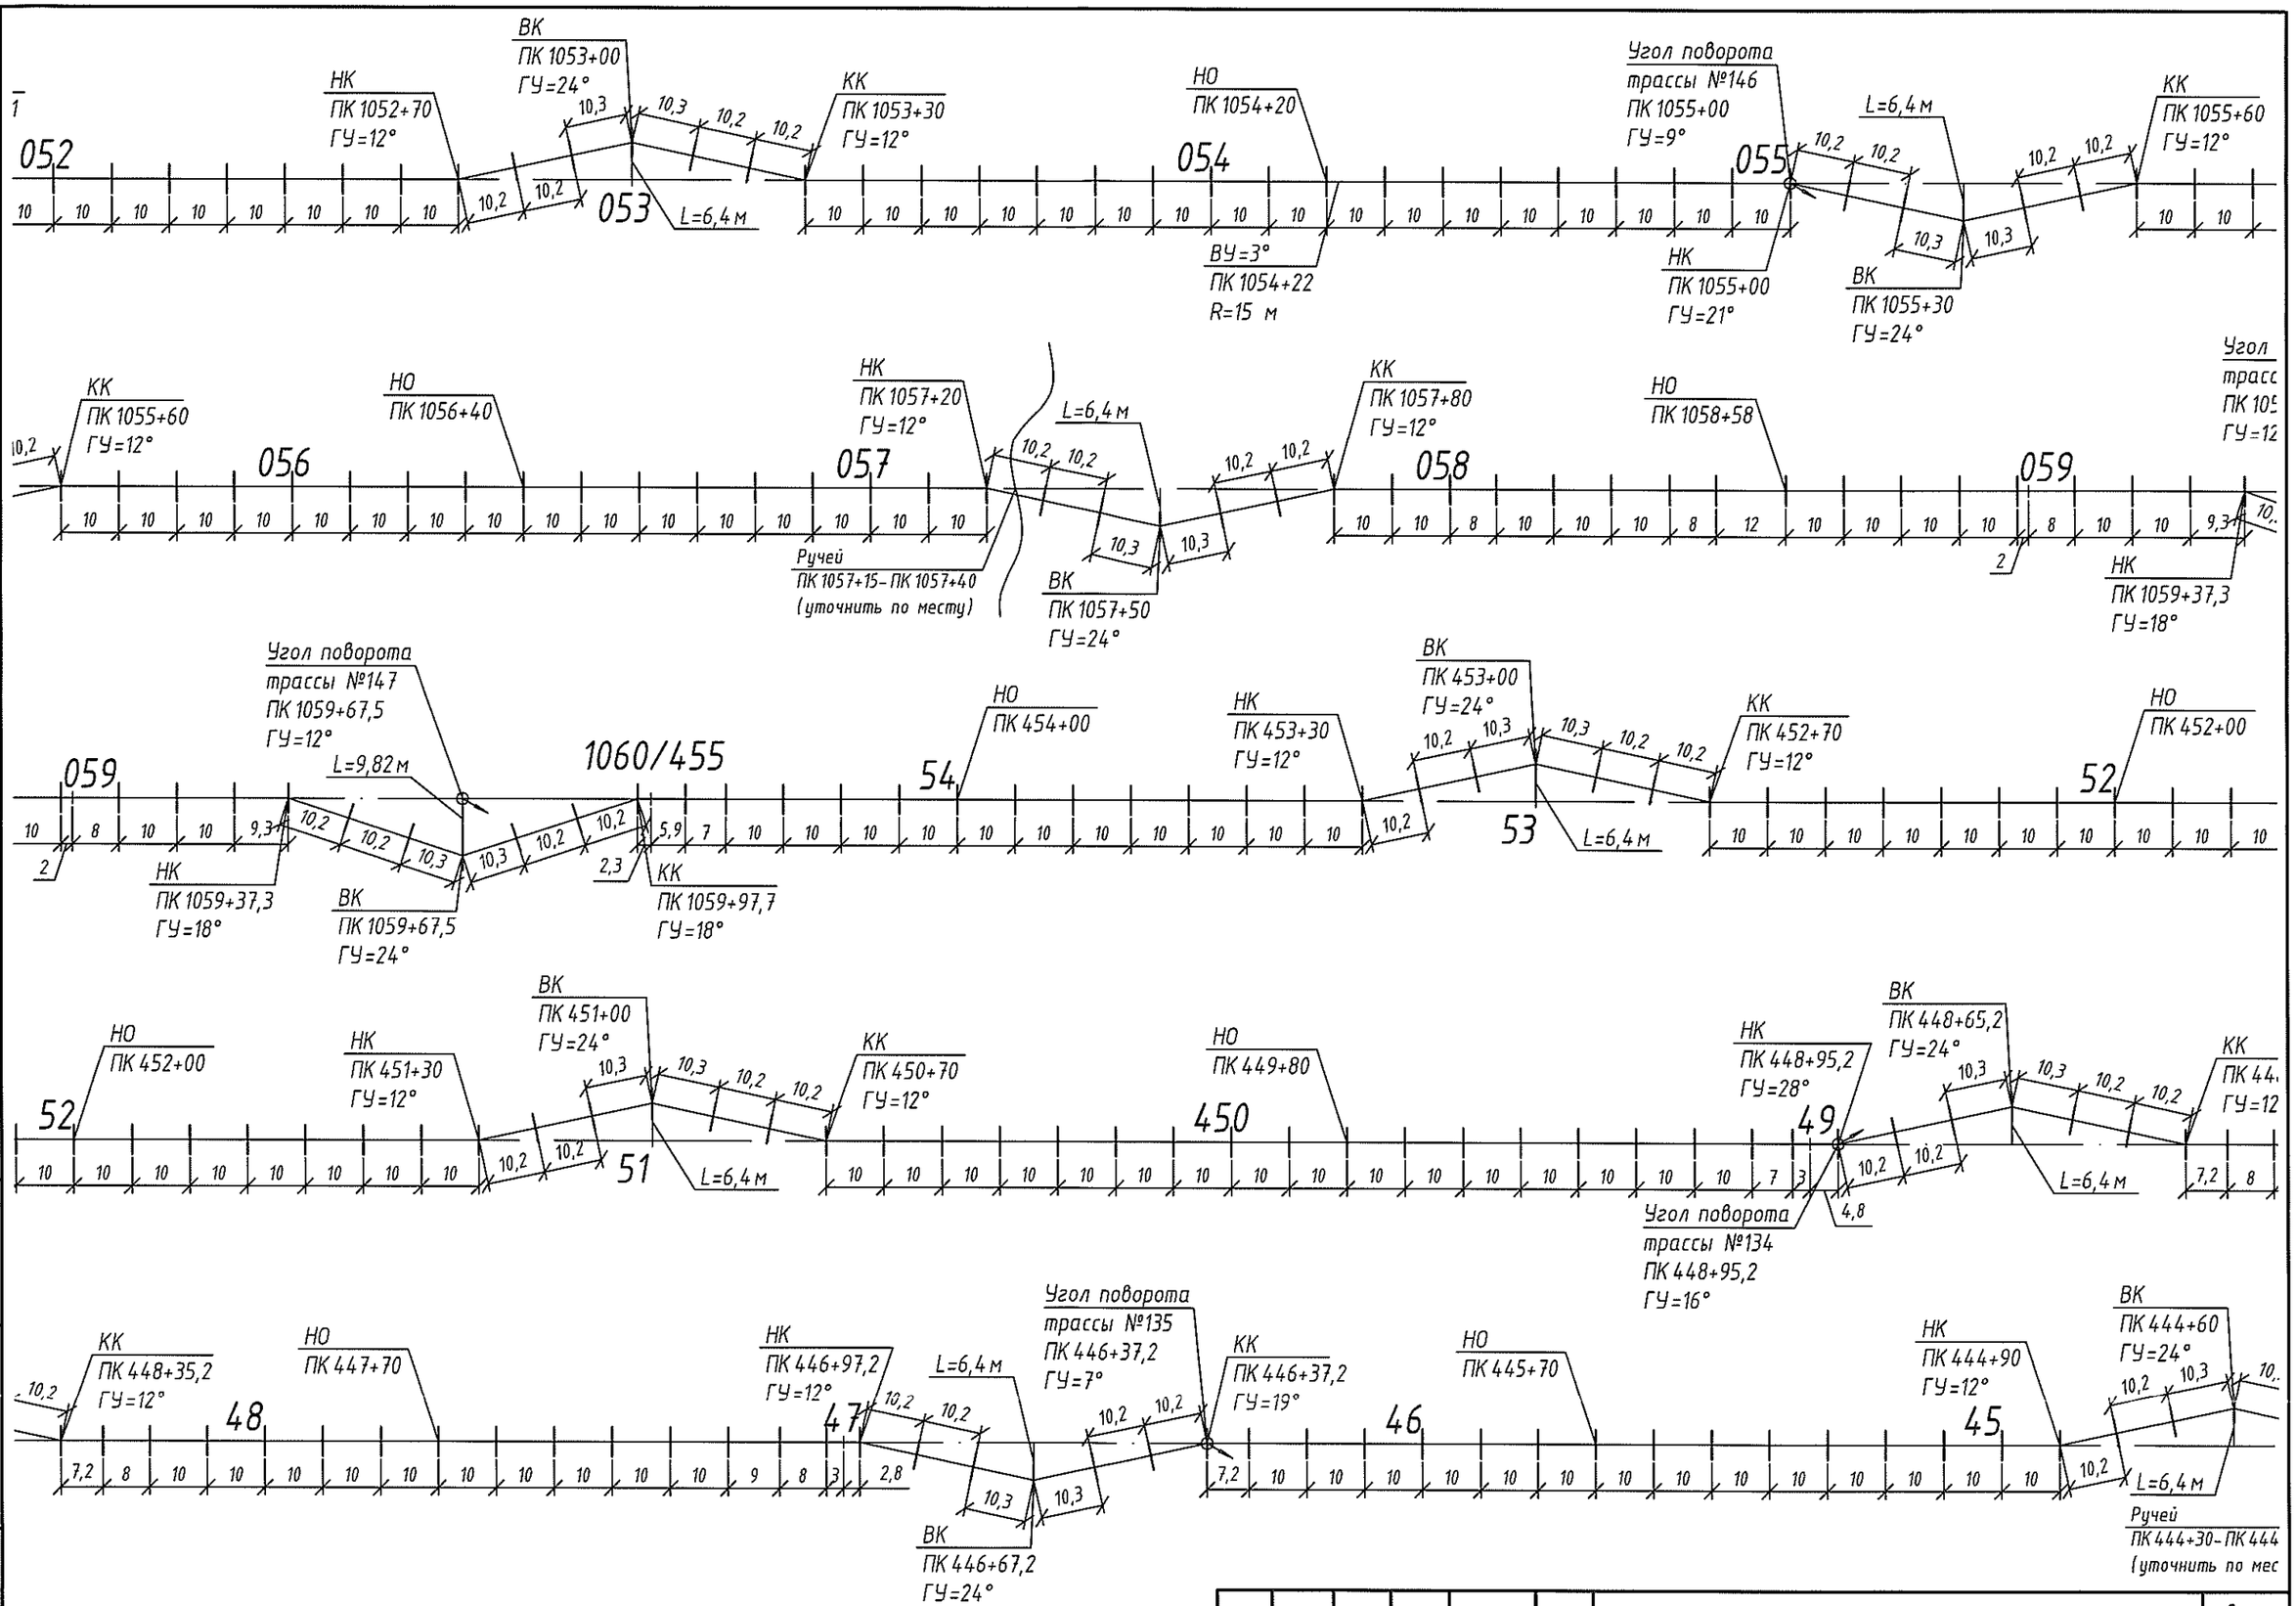

Согласовано


Взам.инв.N

Подпись и дата

Инв.N подл.

Изм.	Кол.уч.	Лист	N док.	Подпись	Дата	III-Д-101/3103-КМ.Л2	Лист 12

Формат А3

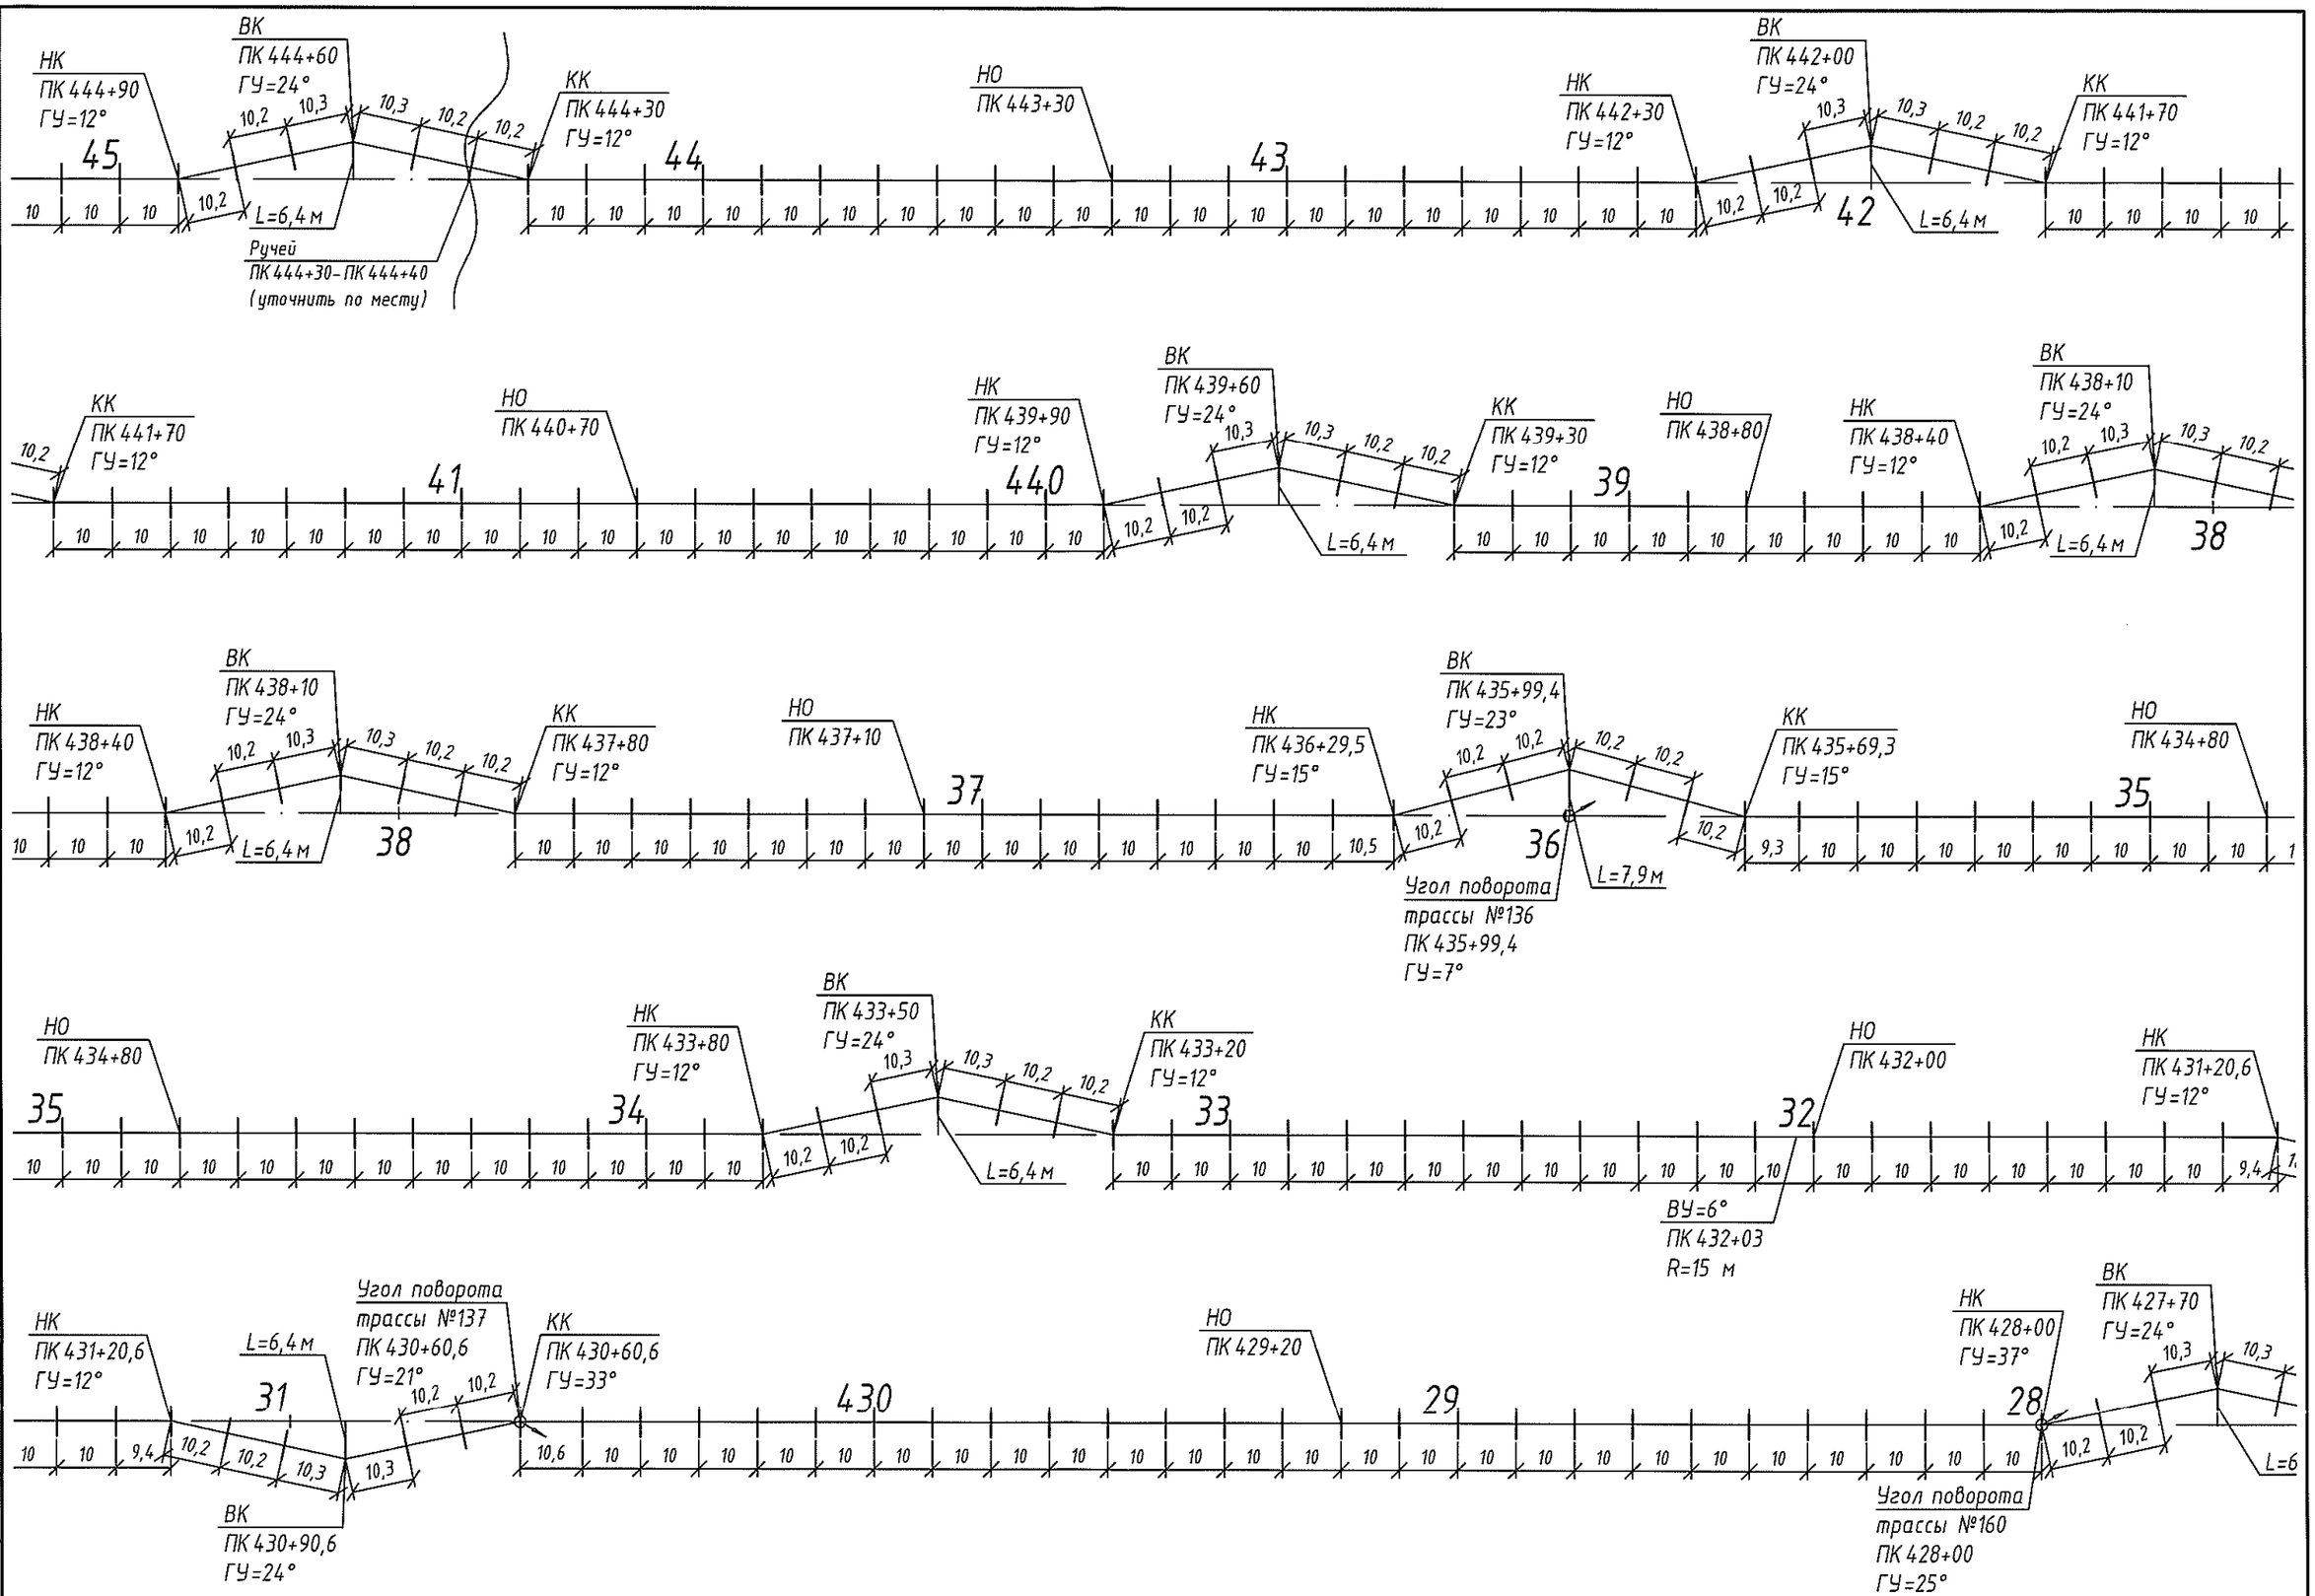

Согласовано

Взам.инв.N

Подпись и дата


Инв.N подл.

Изм.	Кол.уч.	Лист	N док.	Подпись	Дата

III-Д-101/3103-КМ.Л2

Лист 13

Формат А3

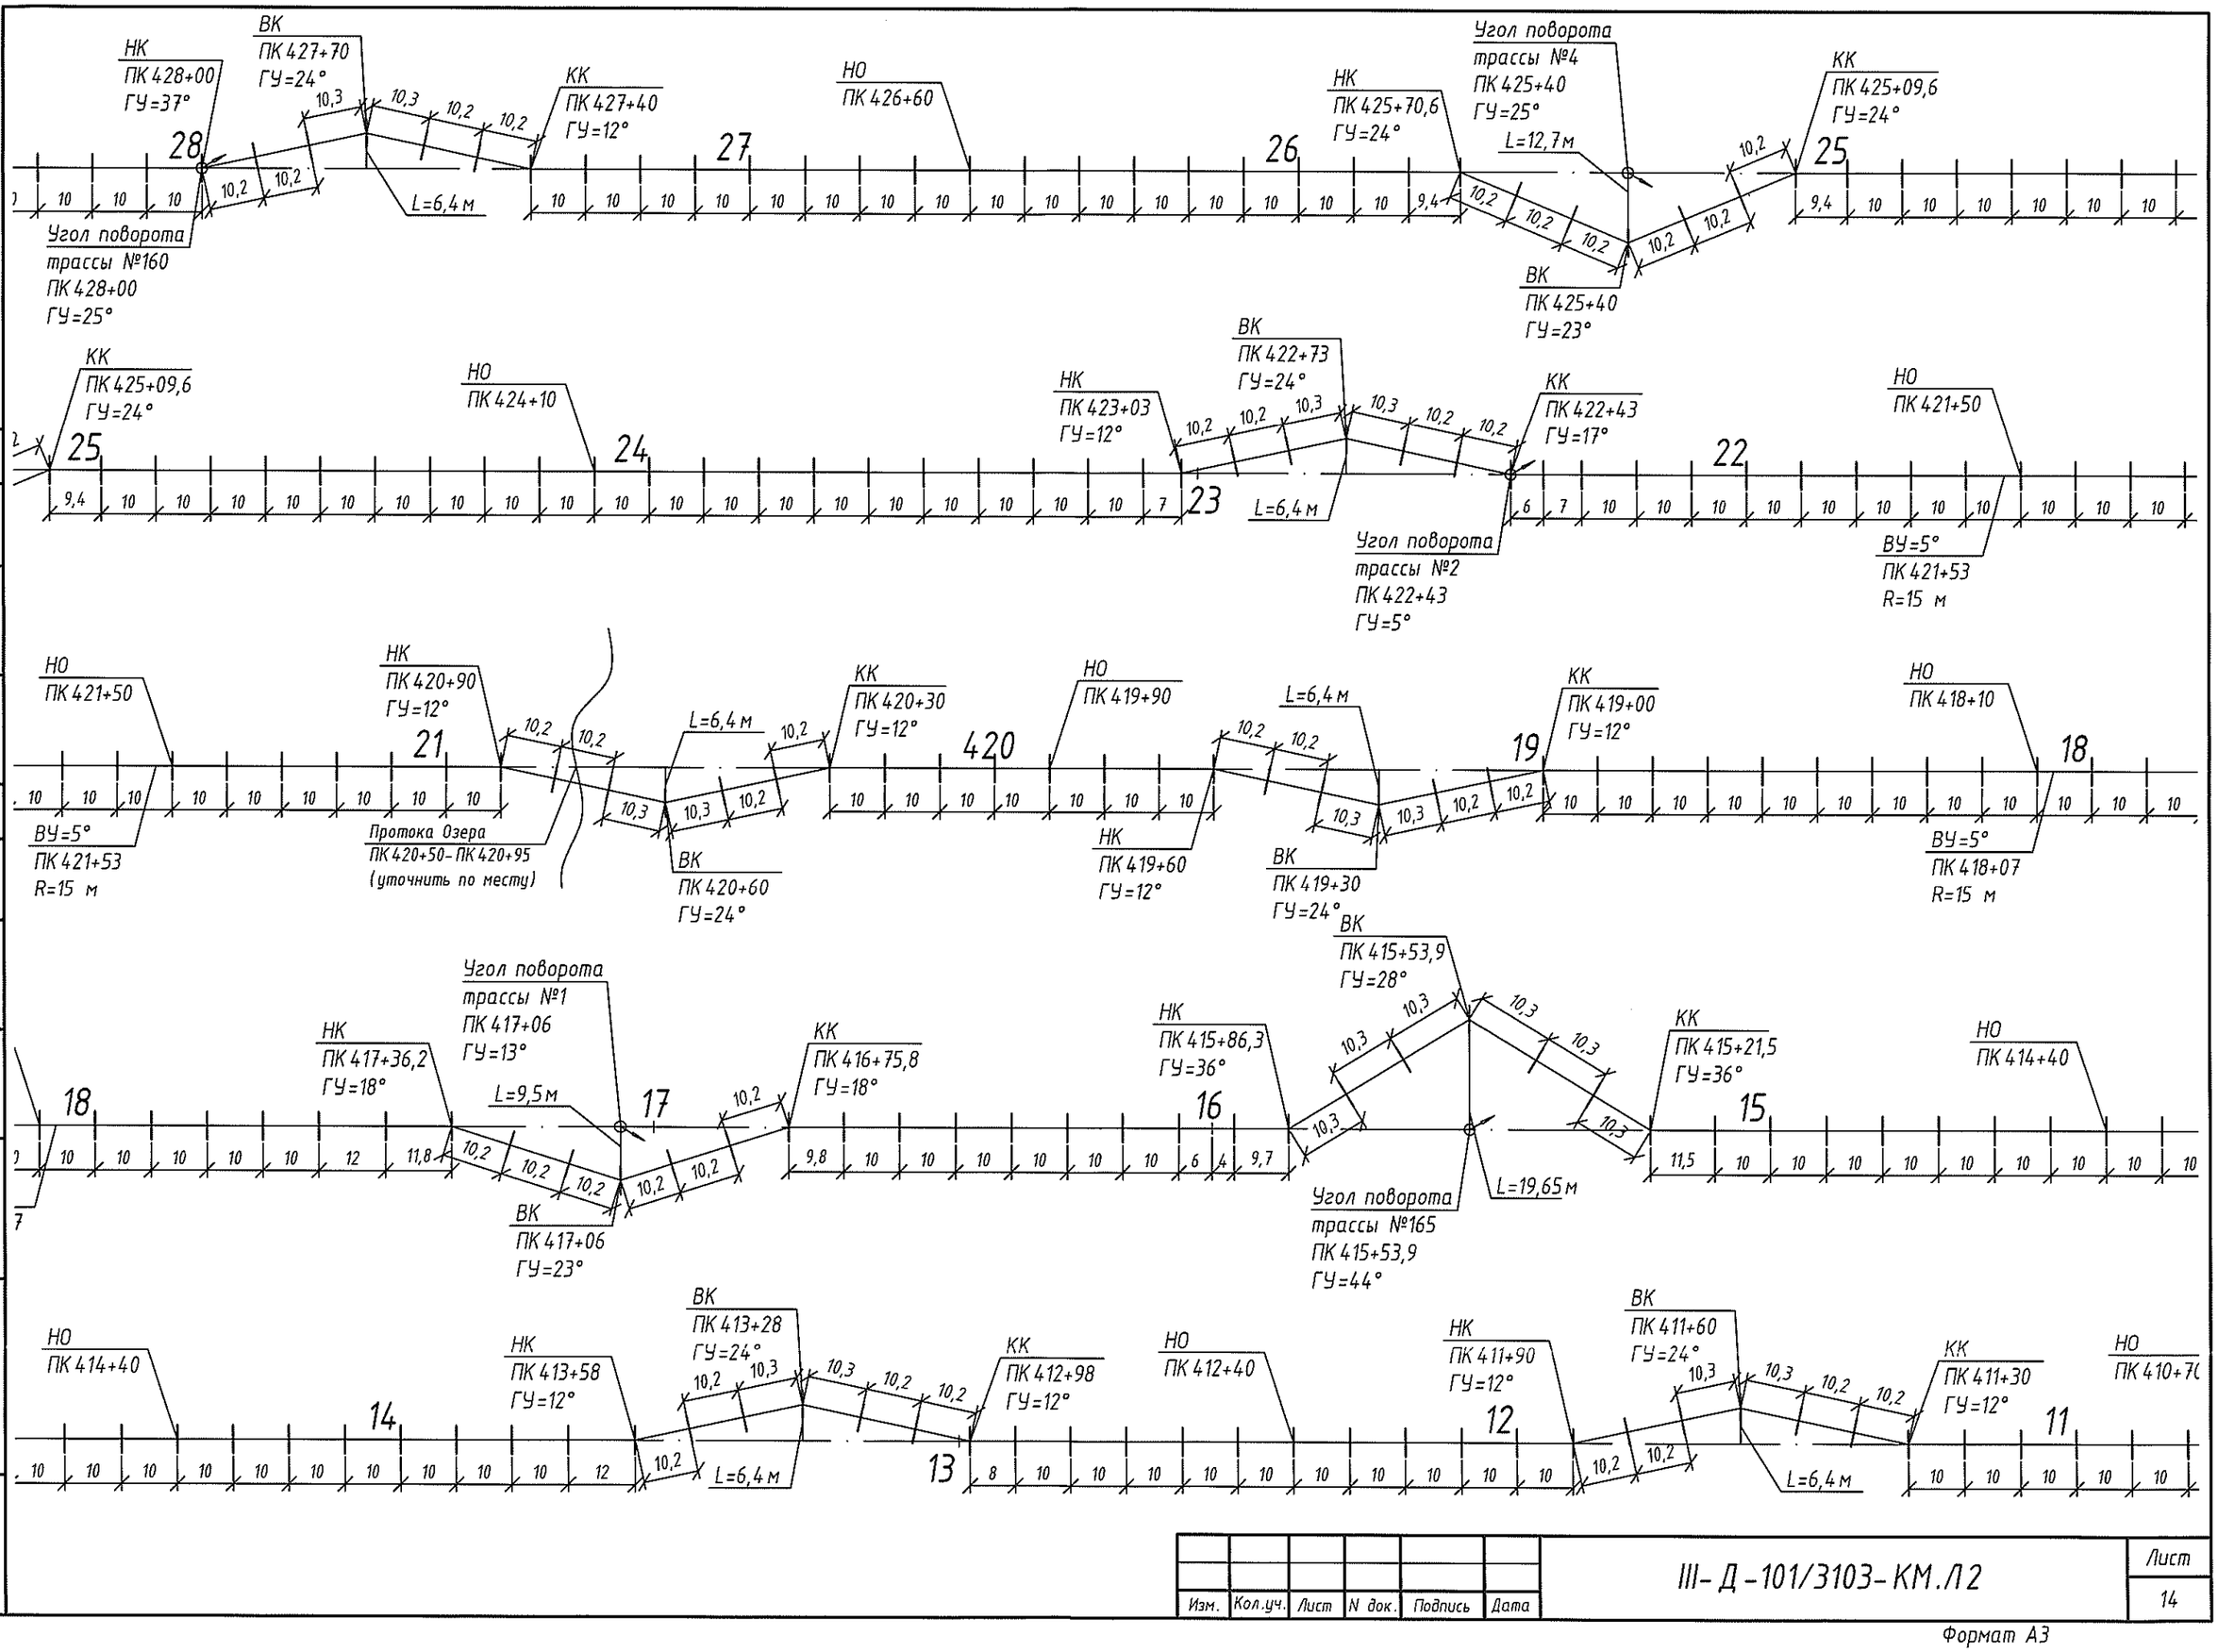

Согласовано

Взам.инв.N

Подпись и дата

Инв.N подл.

Изм.	Кол.уч.	Лист	N док.	Подпись	Дата	III-Д-101/3103-КМ.Л2	Лист 14

Формат А3

КК ПК 411+30 ГУ=12°
НО ПК 410+70
НК ПК 410+10 ГУ=12°
ВК ПК 409+80 ГУ=24°
КК ПК 409+50 ГУ=12°
НО ПК 408+50
НК ПК 407+50 ГУ=12°
11
410
09
08
L=6,4 м

НК ПК 407+50 ГУ=12°
ВК ПК 407+20 ГУ=24°
КК ПК 406+90 ГУ=12°
НО ПК 405+90
НК ПК 404+90 ГУ=12°
ВК ПК 404+60 ГУ=24°
КК ПК 404+30 ГУ=12°
07
06
05
04
L=6,4 м

КК ПК 404+30 ГУ=12°
НО ПК 403+30
НК ПК 402+36,2 ГУ=42°
Угол поворота трассы №139 ПК 402+02,2 ГУ=56°
L=23,47 м
КК ПК 401+68,2 ГУ=42°
НО ПК 401+20
НК ПК 400+57,3 ГУ=30°
ПК 4 ГУ=.
04
03
02
01
ВК ПК 402+02,2 ГУ=28°
Угол по трассы ПК 400+ ГУ=35°

НК ПК 400+57,3 ГУ=30°
ВК ПК 400+26,6 ГУ=25°
КК ПК 399+95,9 ГУ=30°
НО ПК 399+20
НК ПК 398+50 ГУ=12°
L=6,4 м
КК ПК 397+90 ГУ=12°
НО ПК 397+30
Угол поворота трассы №140 ПК 400+26,6 ГУ=35°
L=16,07 м
Ограждение скотопрогона ПК 399+70
400
99
98
97
ВК ПК 398+20 ГУ=24°

НО ПК 396+10
НК ПК 395+61,4 ГУ=24°
Угол поворота трассы №141 ПК 395+30,8 ГУ=23°
L=6,66 м
КК ПК 395+0,2 ГУ=24°
НО ПК 394+00
Скотопрогон ПК 397+21- ПК 396+21 4∠90°
ВК ПК 395+30,8 ГУ=25°
Ограждение скотопрогона ПК 394+00
97
96
95
94

Согласовано

Взам.инв.N

Подпись и дата


Инв.N подл.

Изм.	Кол.уч.	Лист	N док.	Подпись	Дата

III-Д-101/3103-КМ.Л2

Лист 15

Формат А3

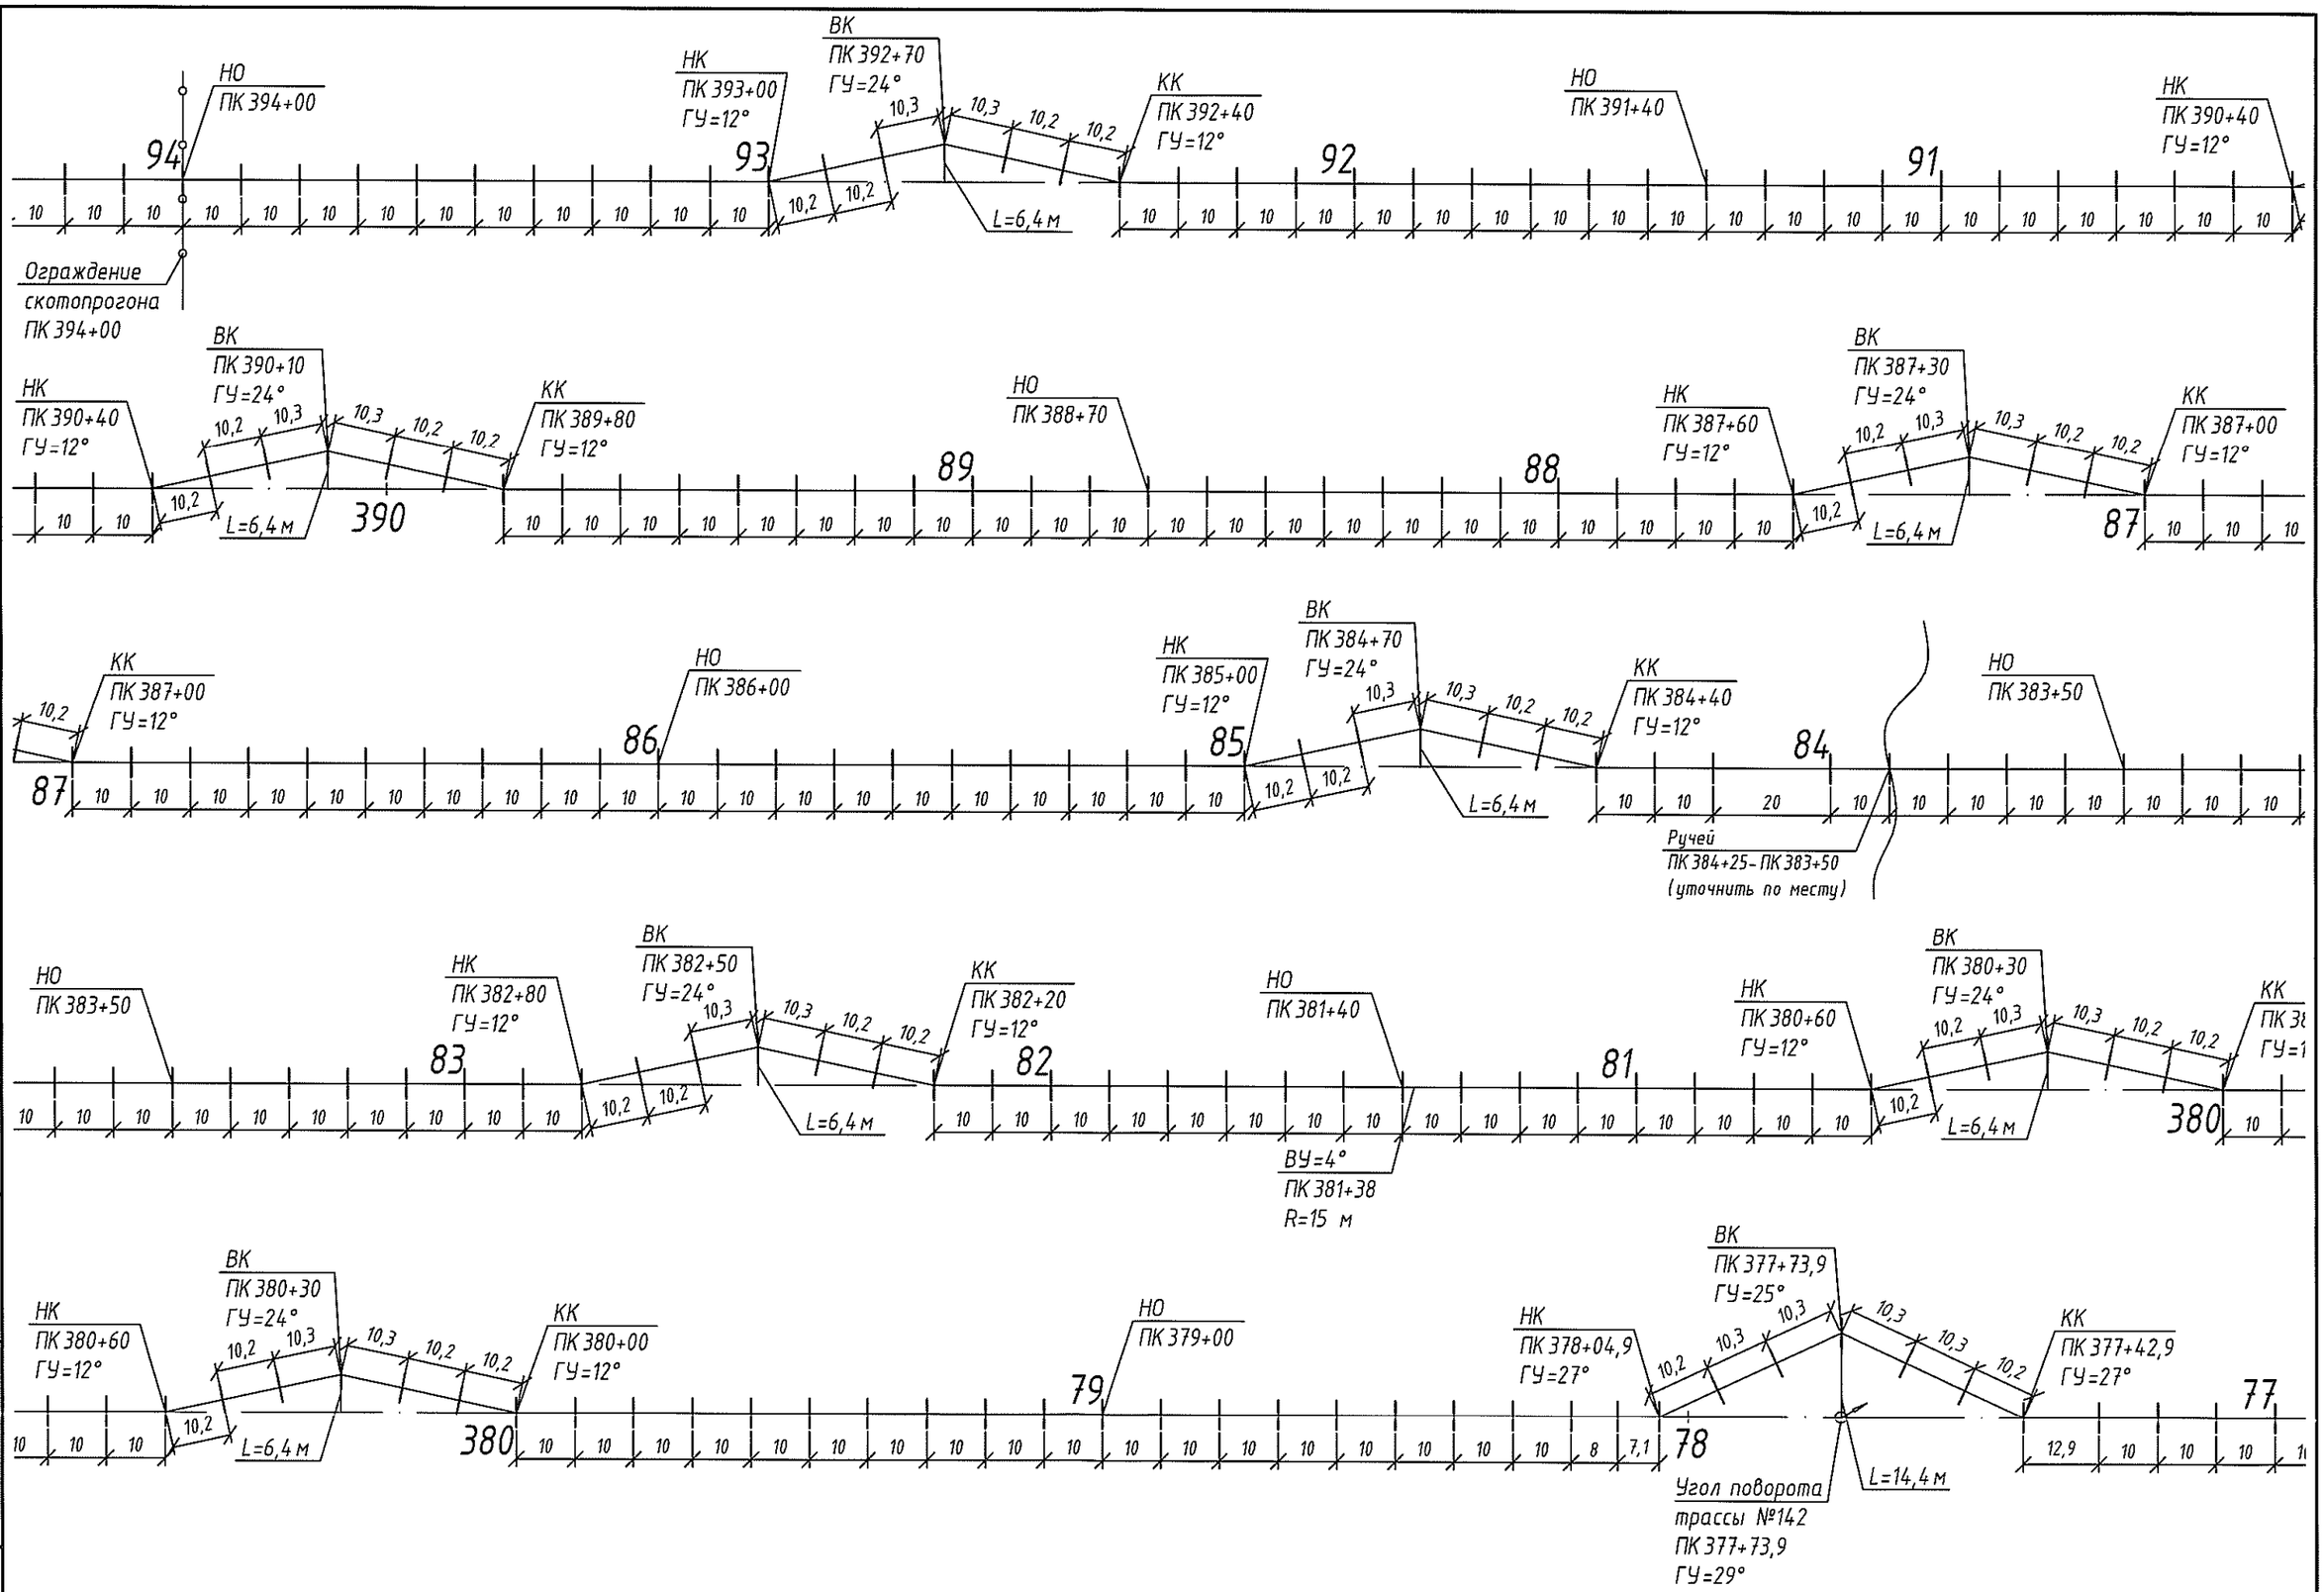

Согласовано

Взам.инв.N

Подпись и дата


Инв.N подл.

Изм.	Кол.уч.	Лист	N док.	Подпись	Дата

III-Д-101/3103-КМ.Л2

Лист 16

Формат А3

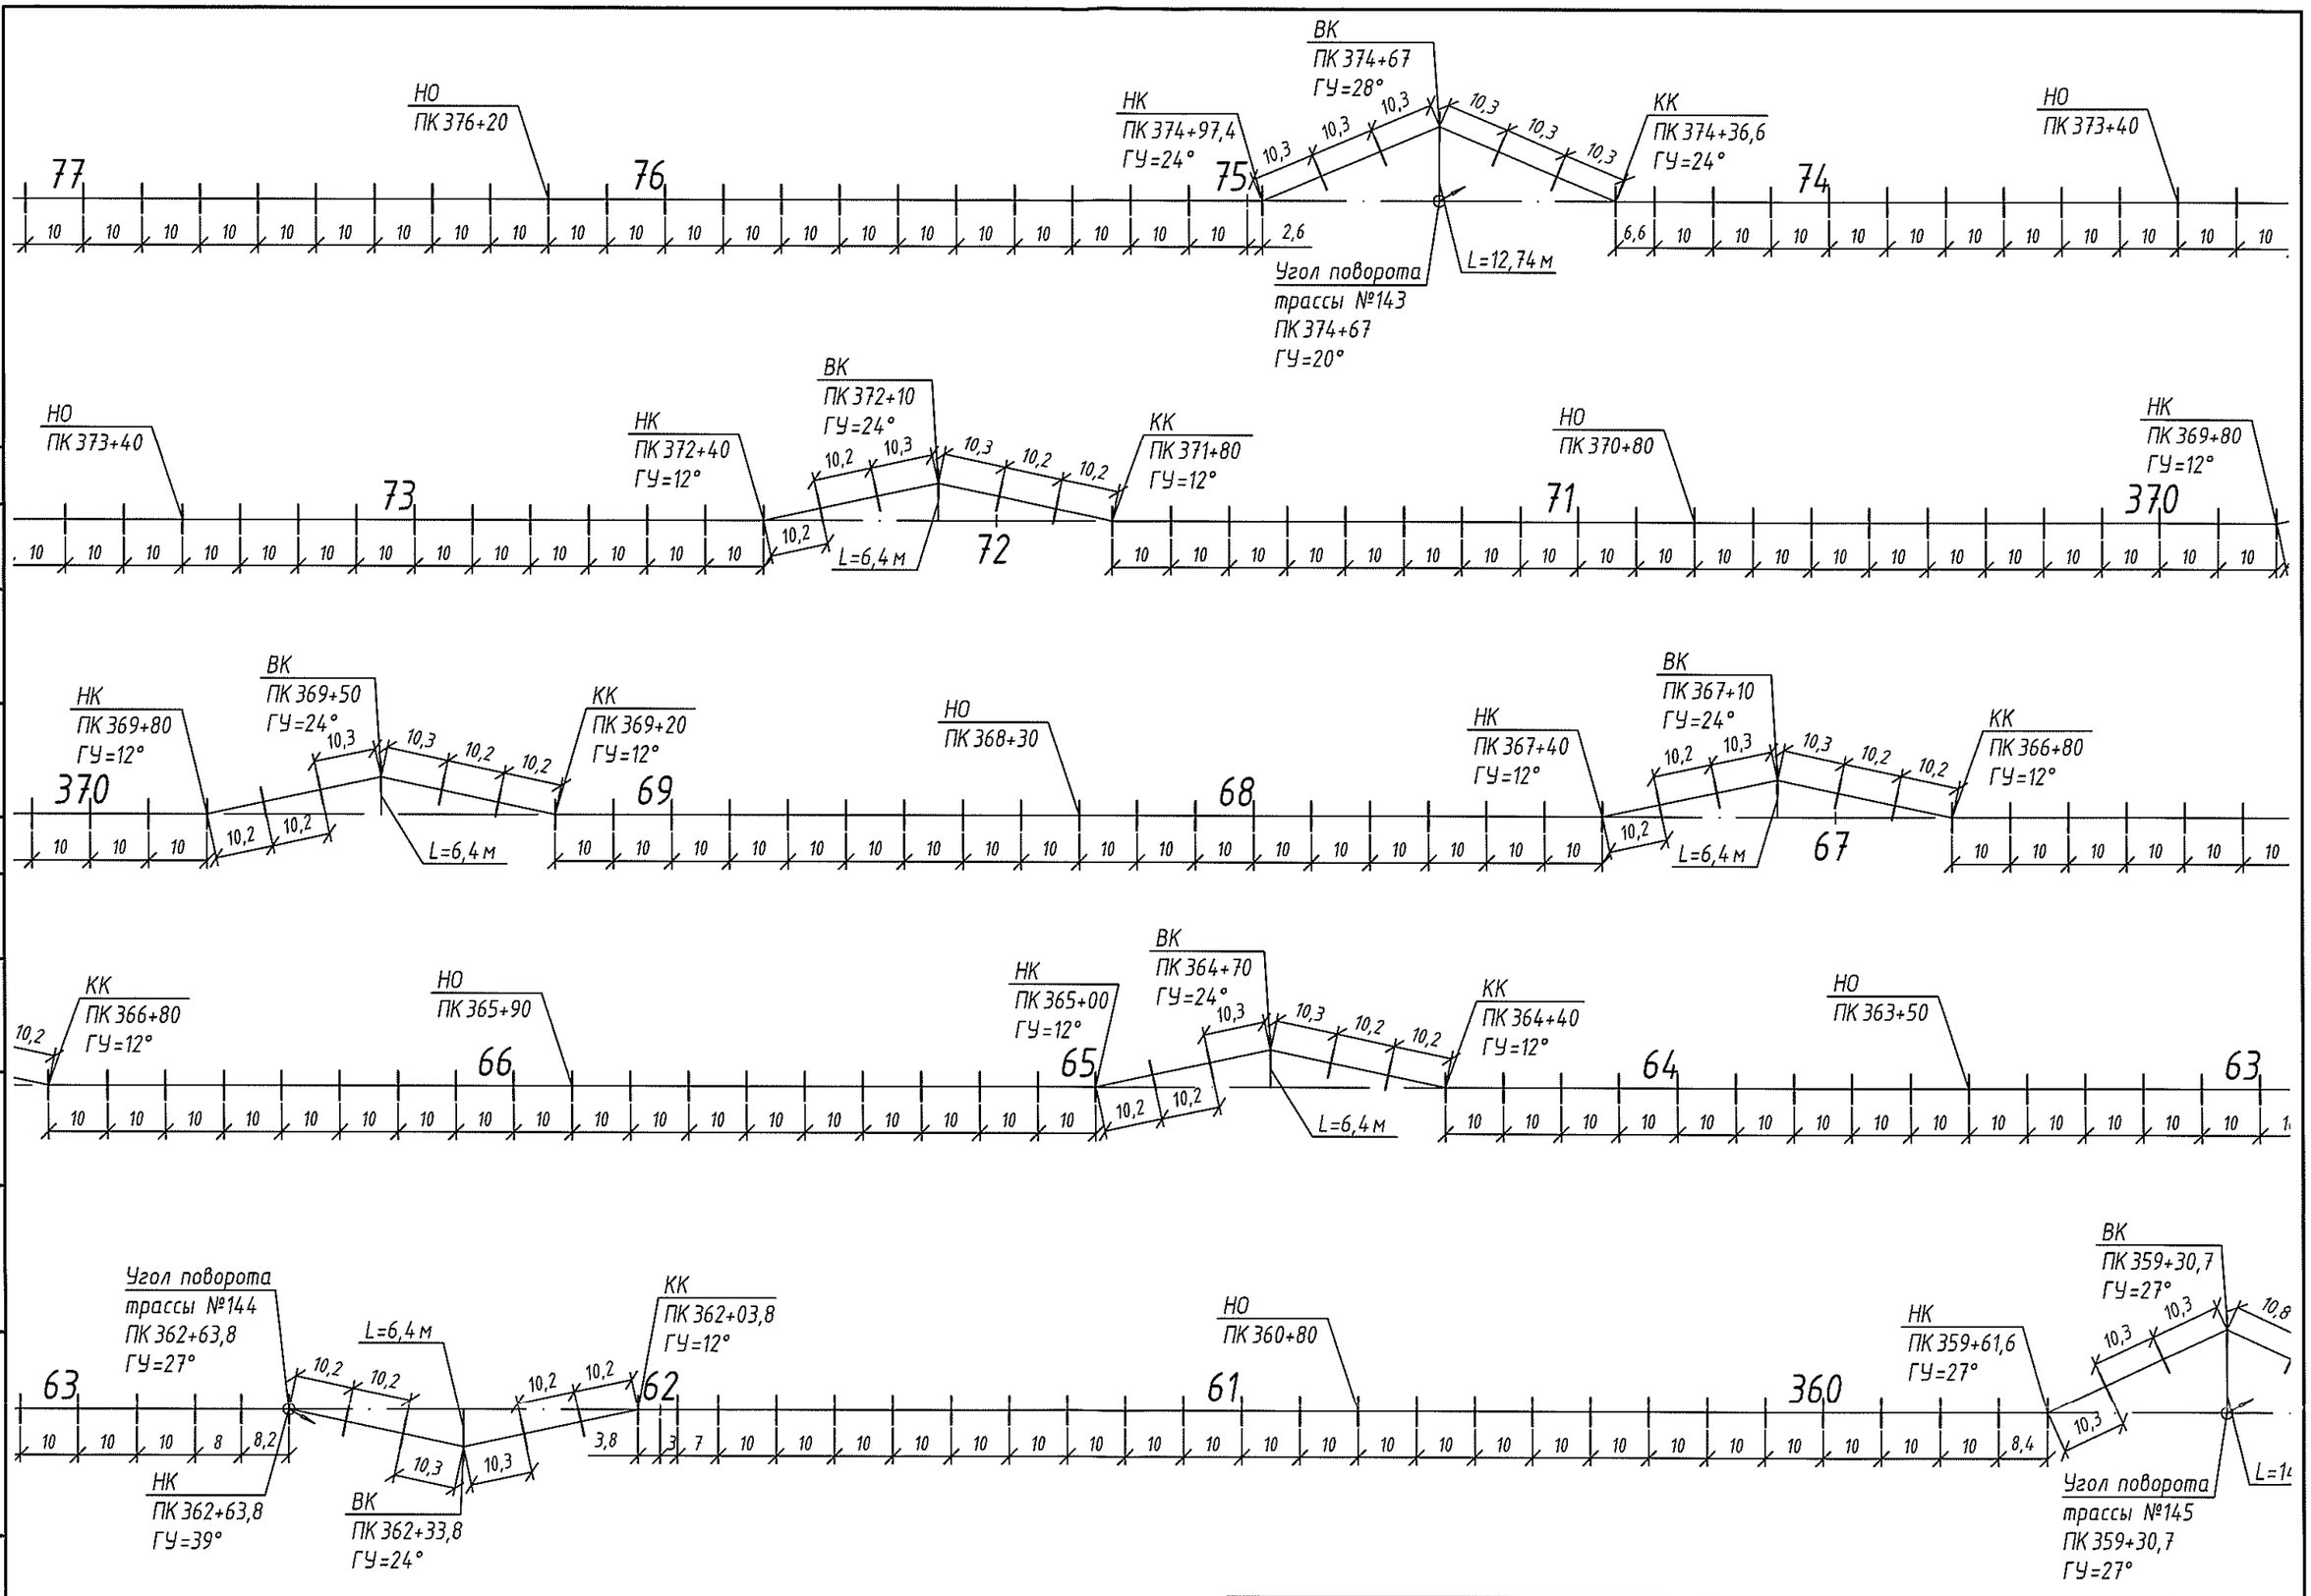

Согласовано

Взам.инв.N

Подпись и дата


Инв.N подл.

Изм.	Кол.уч.	Лист	N док.	Подпись	Дата

III-Д-101/3103-КМ.Л2

Лист 17

Формат А3

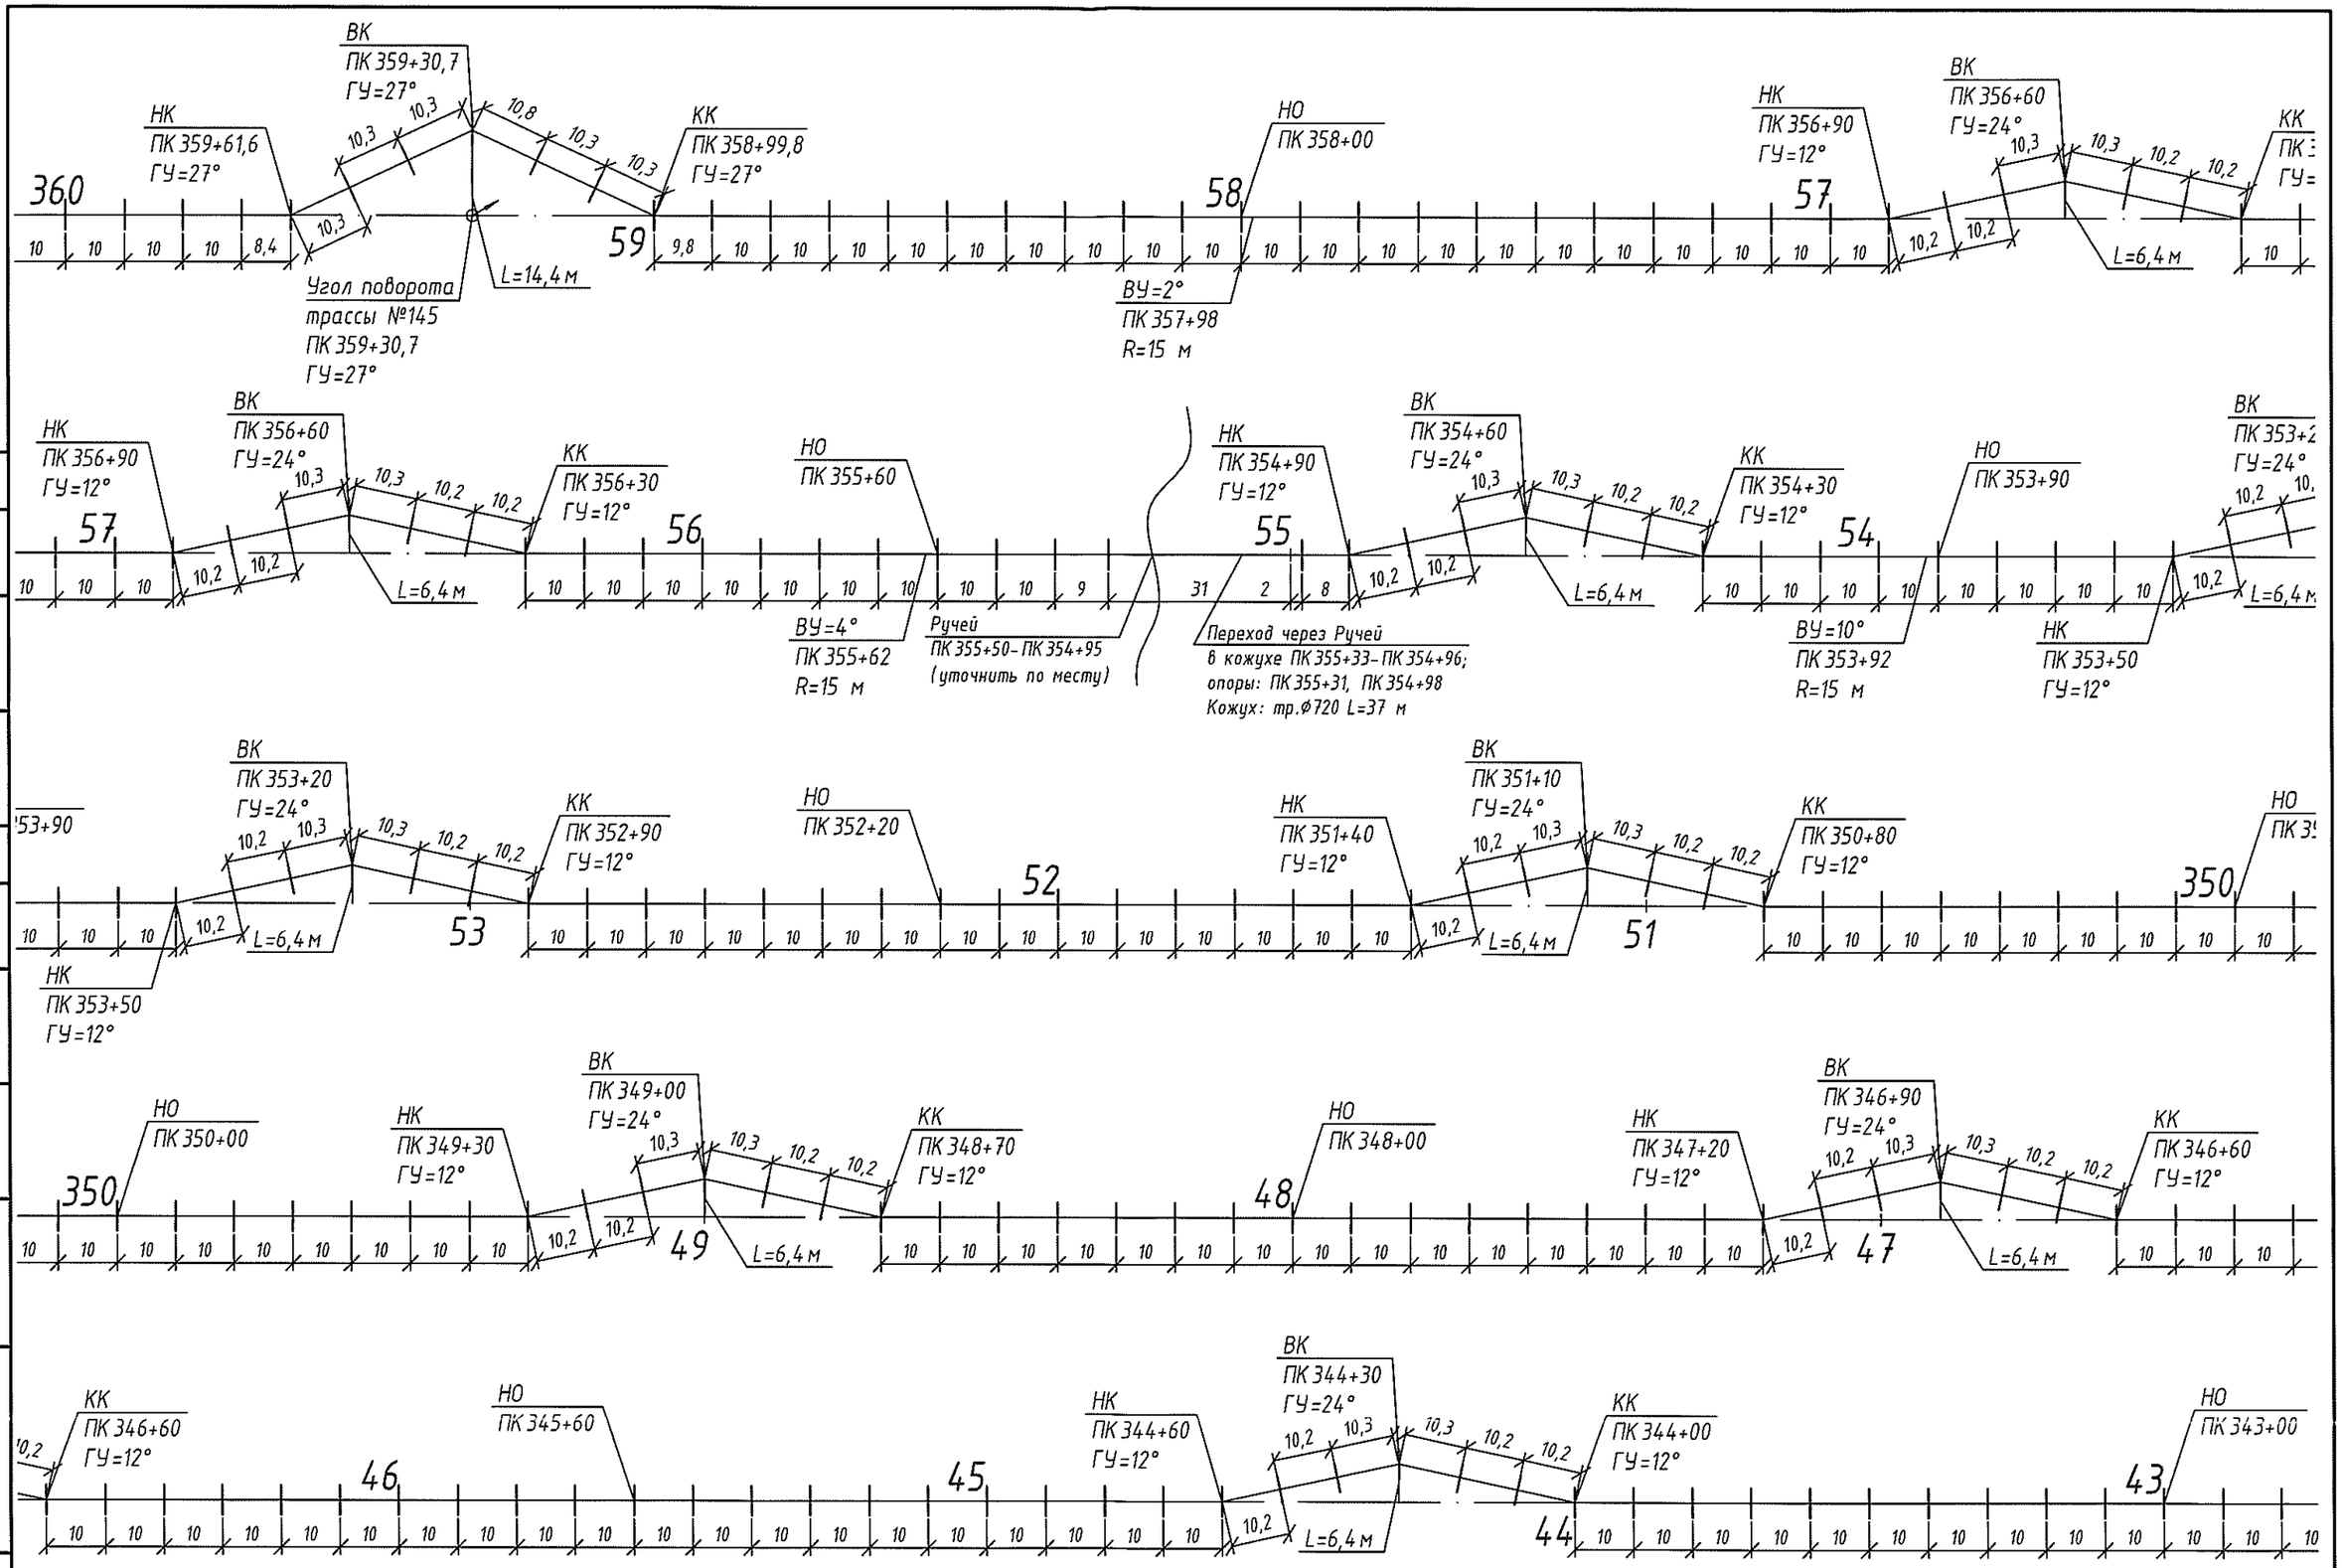

Согласовано

Взам.инв.N

Подпись и дата


Инв.N подл.

Изм.	Кол.уч.	Лист	N док.	Подпись	Дата

III–Д–101/3103–КМ.Л2

Лист 18

Формат А3

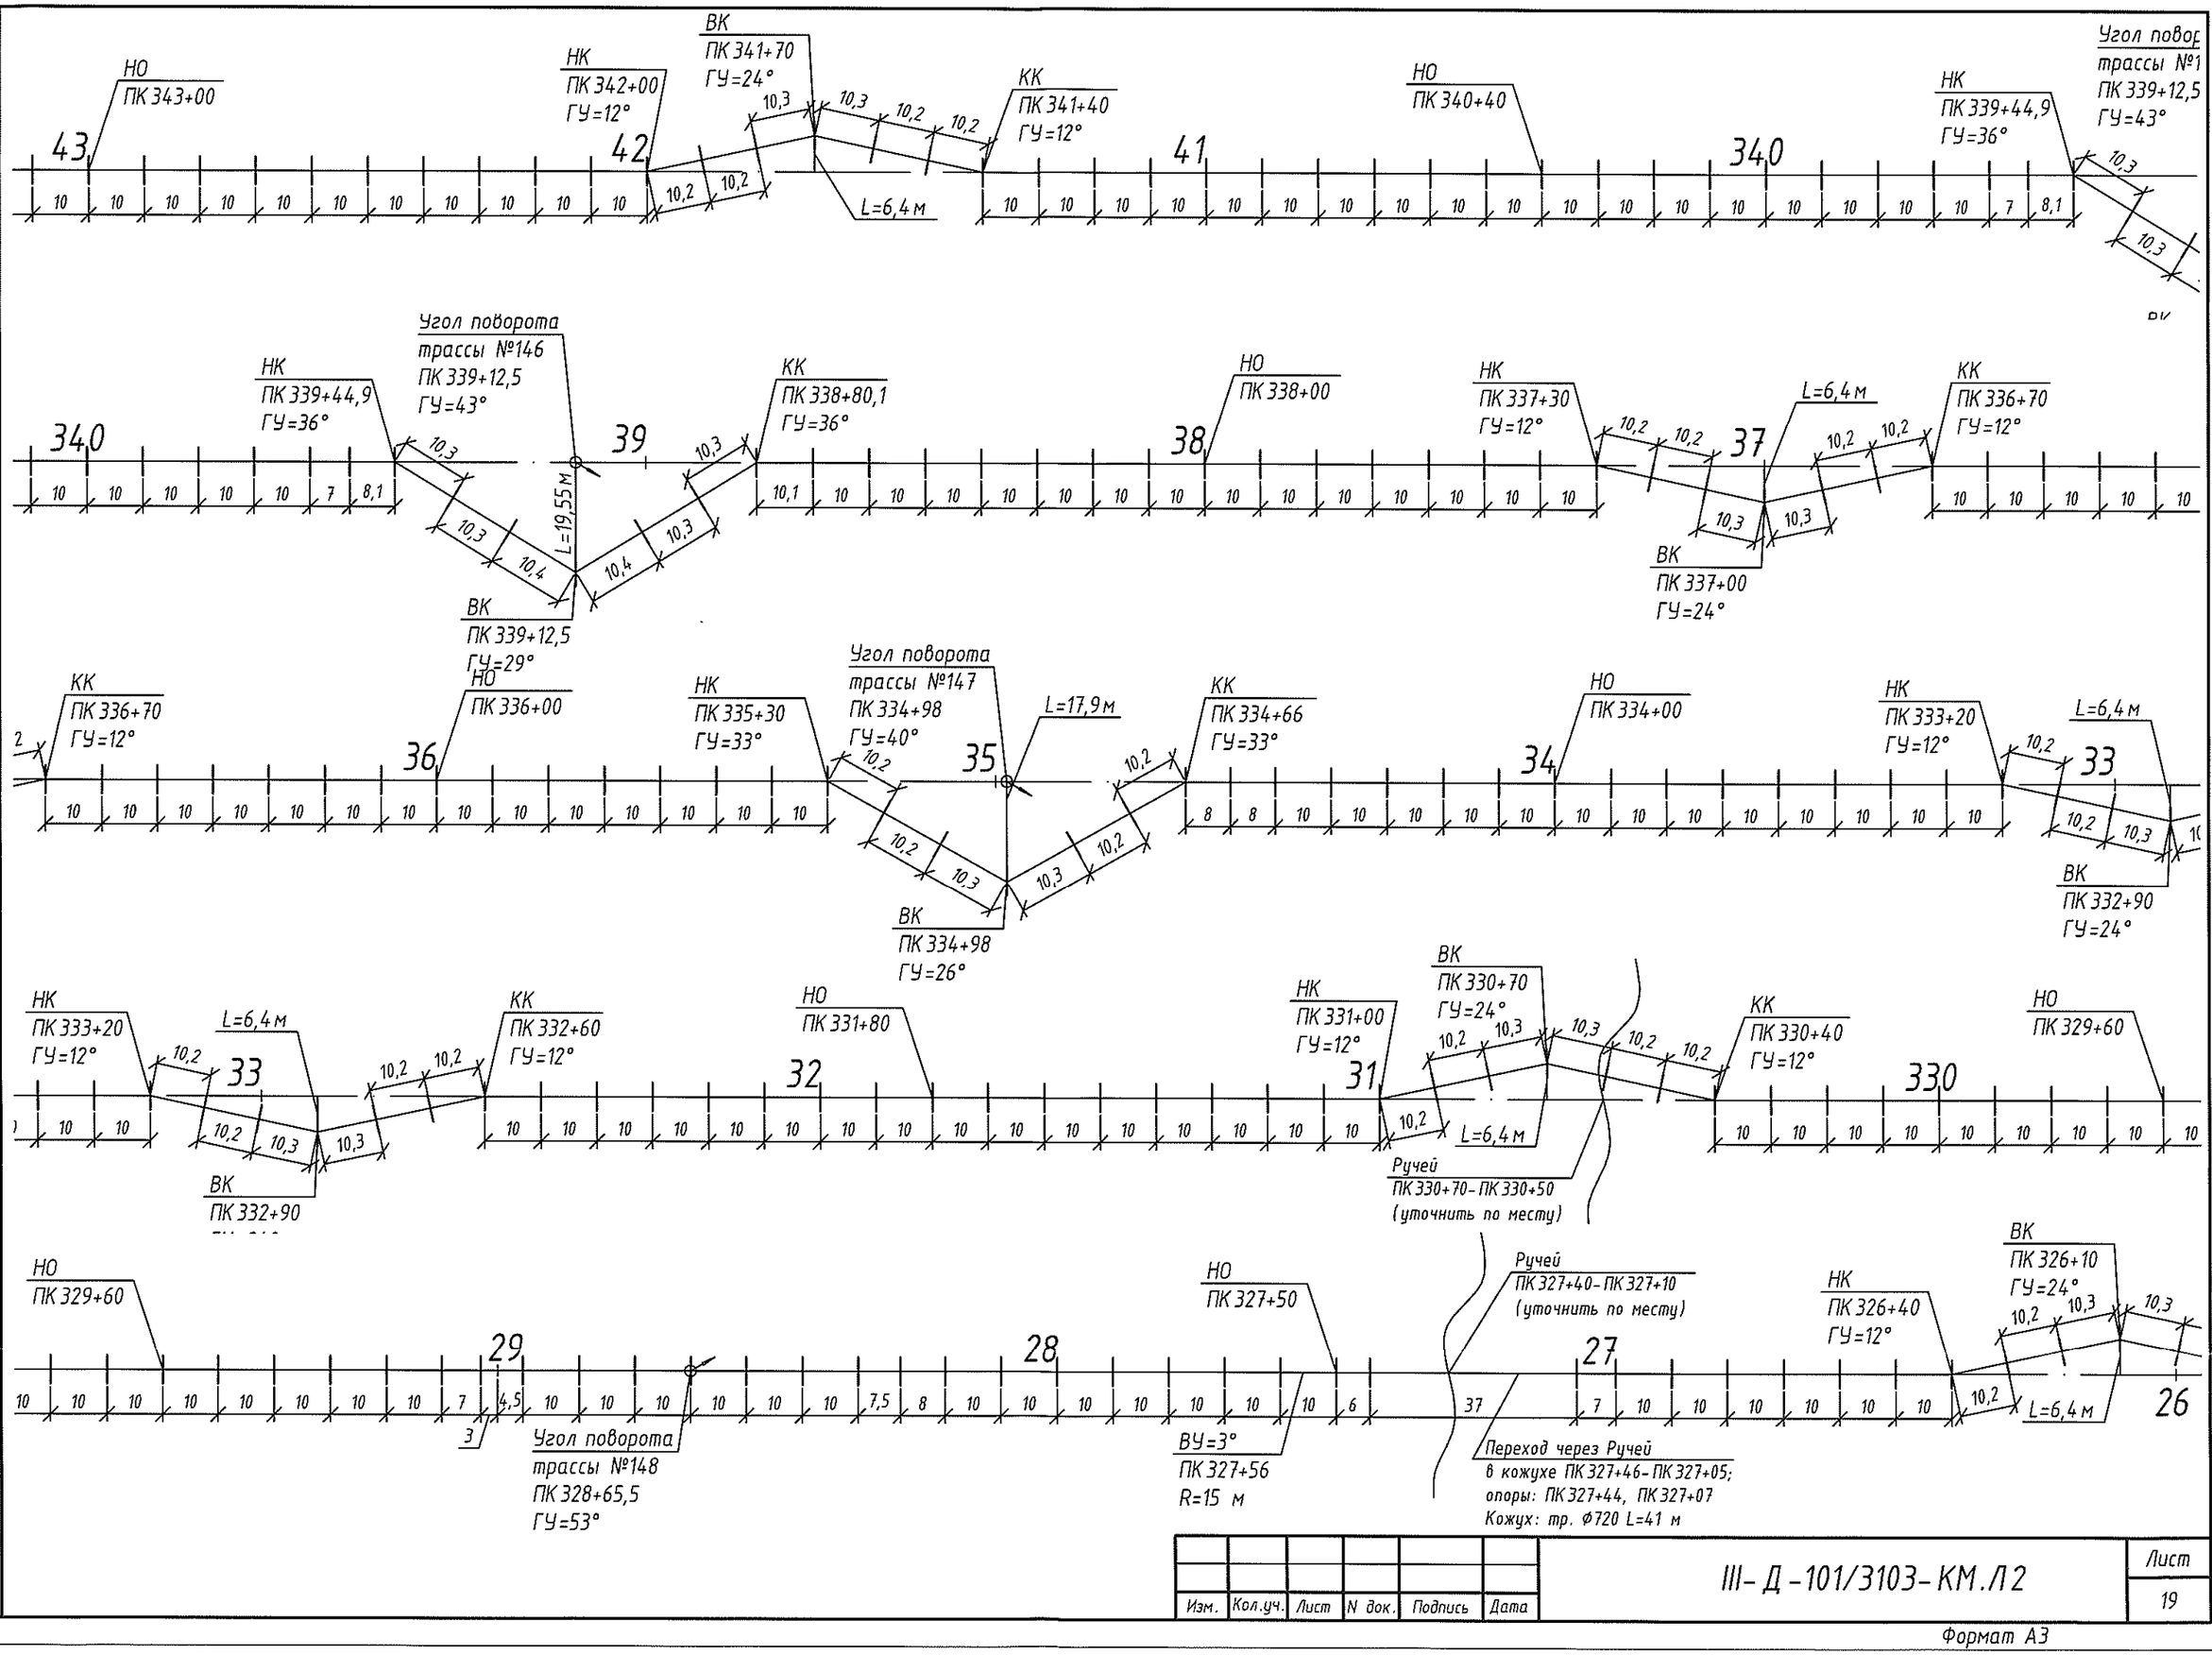

Согласовано

Взам.инв.N

Подпись и дата


Инв.N подл.

Изм.	Кол.уч.	Лист	N док.	Подпись	Дата

III-Д-101/3103-КМ.Л2

Лист 19

Формат А3

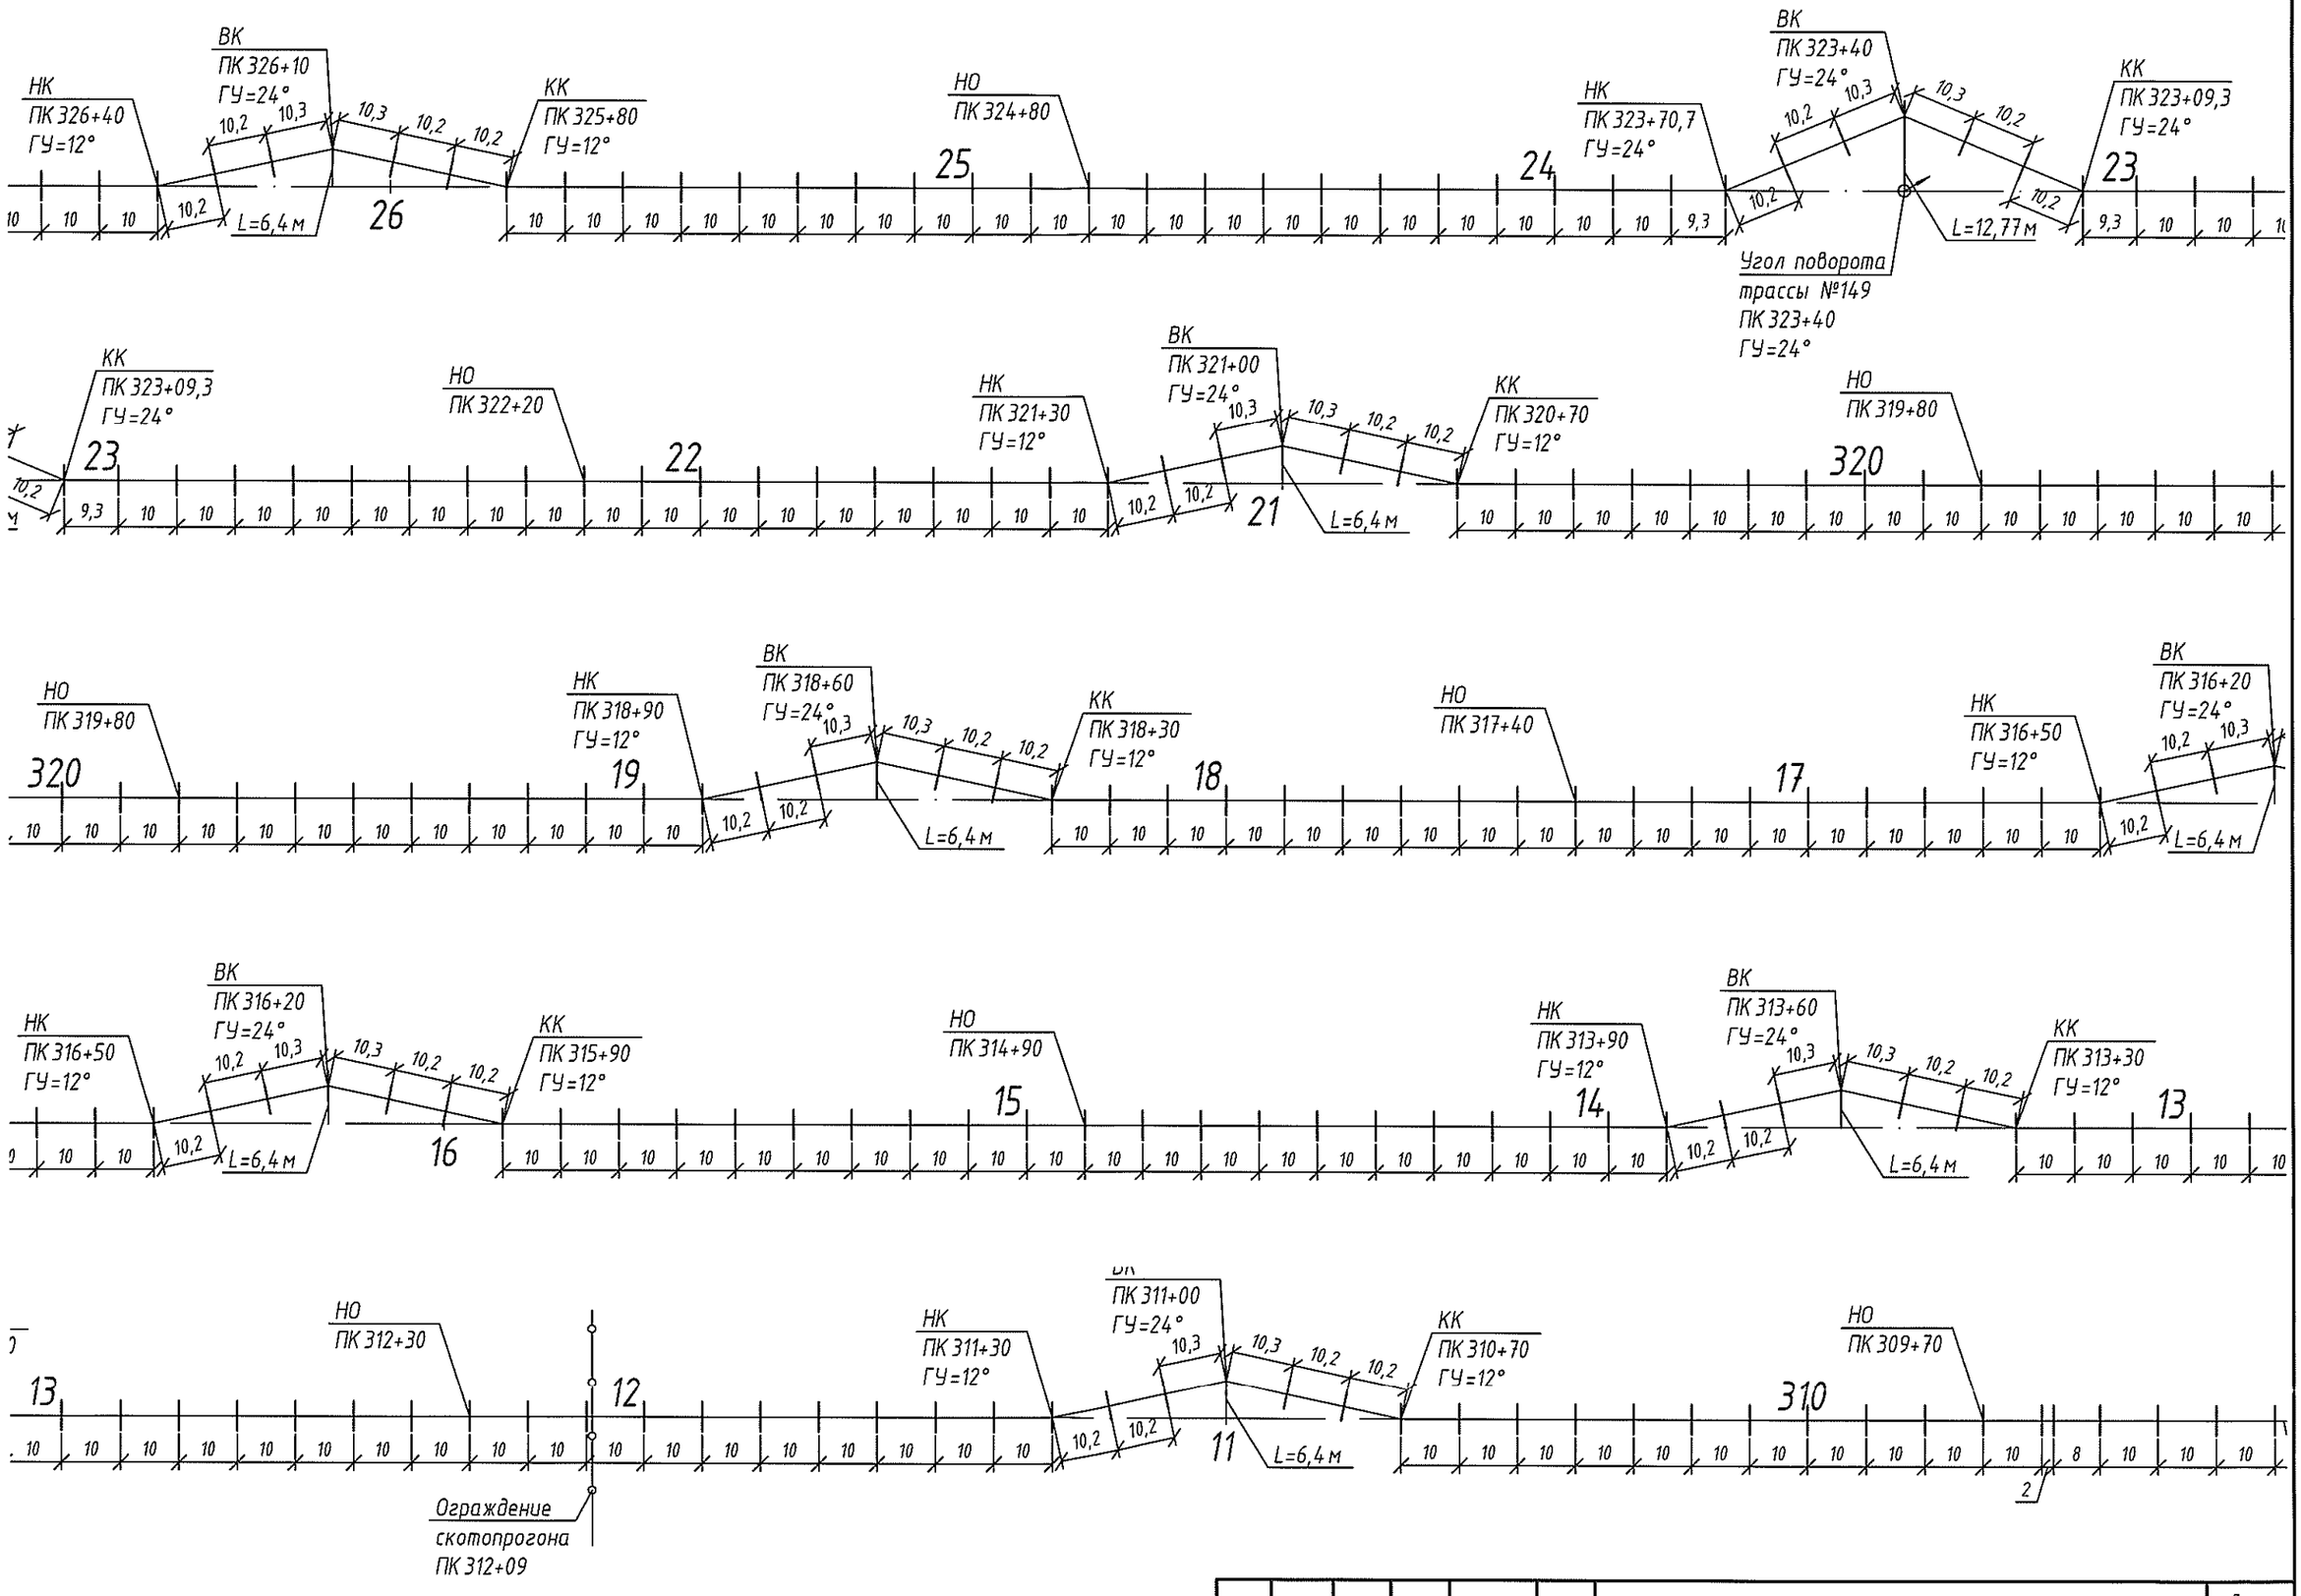

Согласовано

Взам.инв.N

Подпись и дата


Инв.N подл.


Изм.	Кол.уч.	Лист	N док.	Подпись	Дата

III-Д-101/3103-КМ.Л2

Лист 20

Формат А3

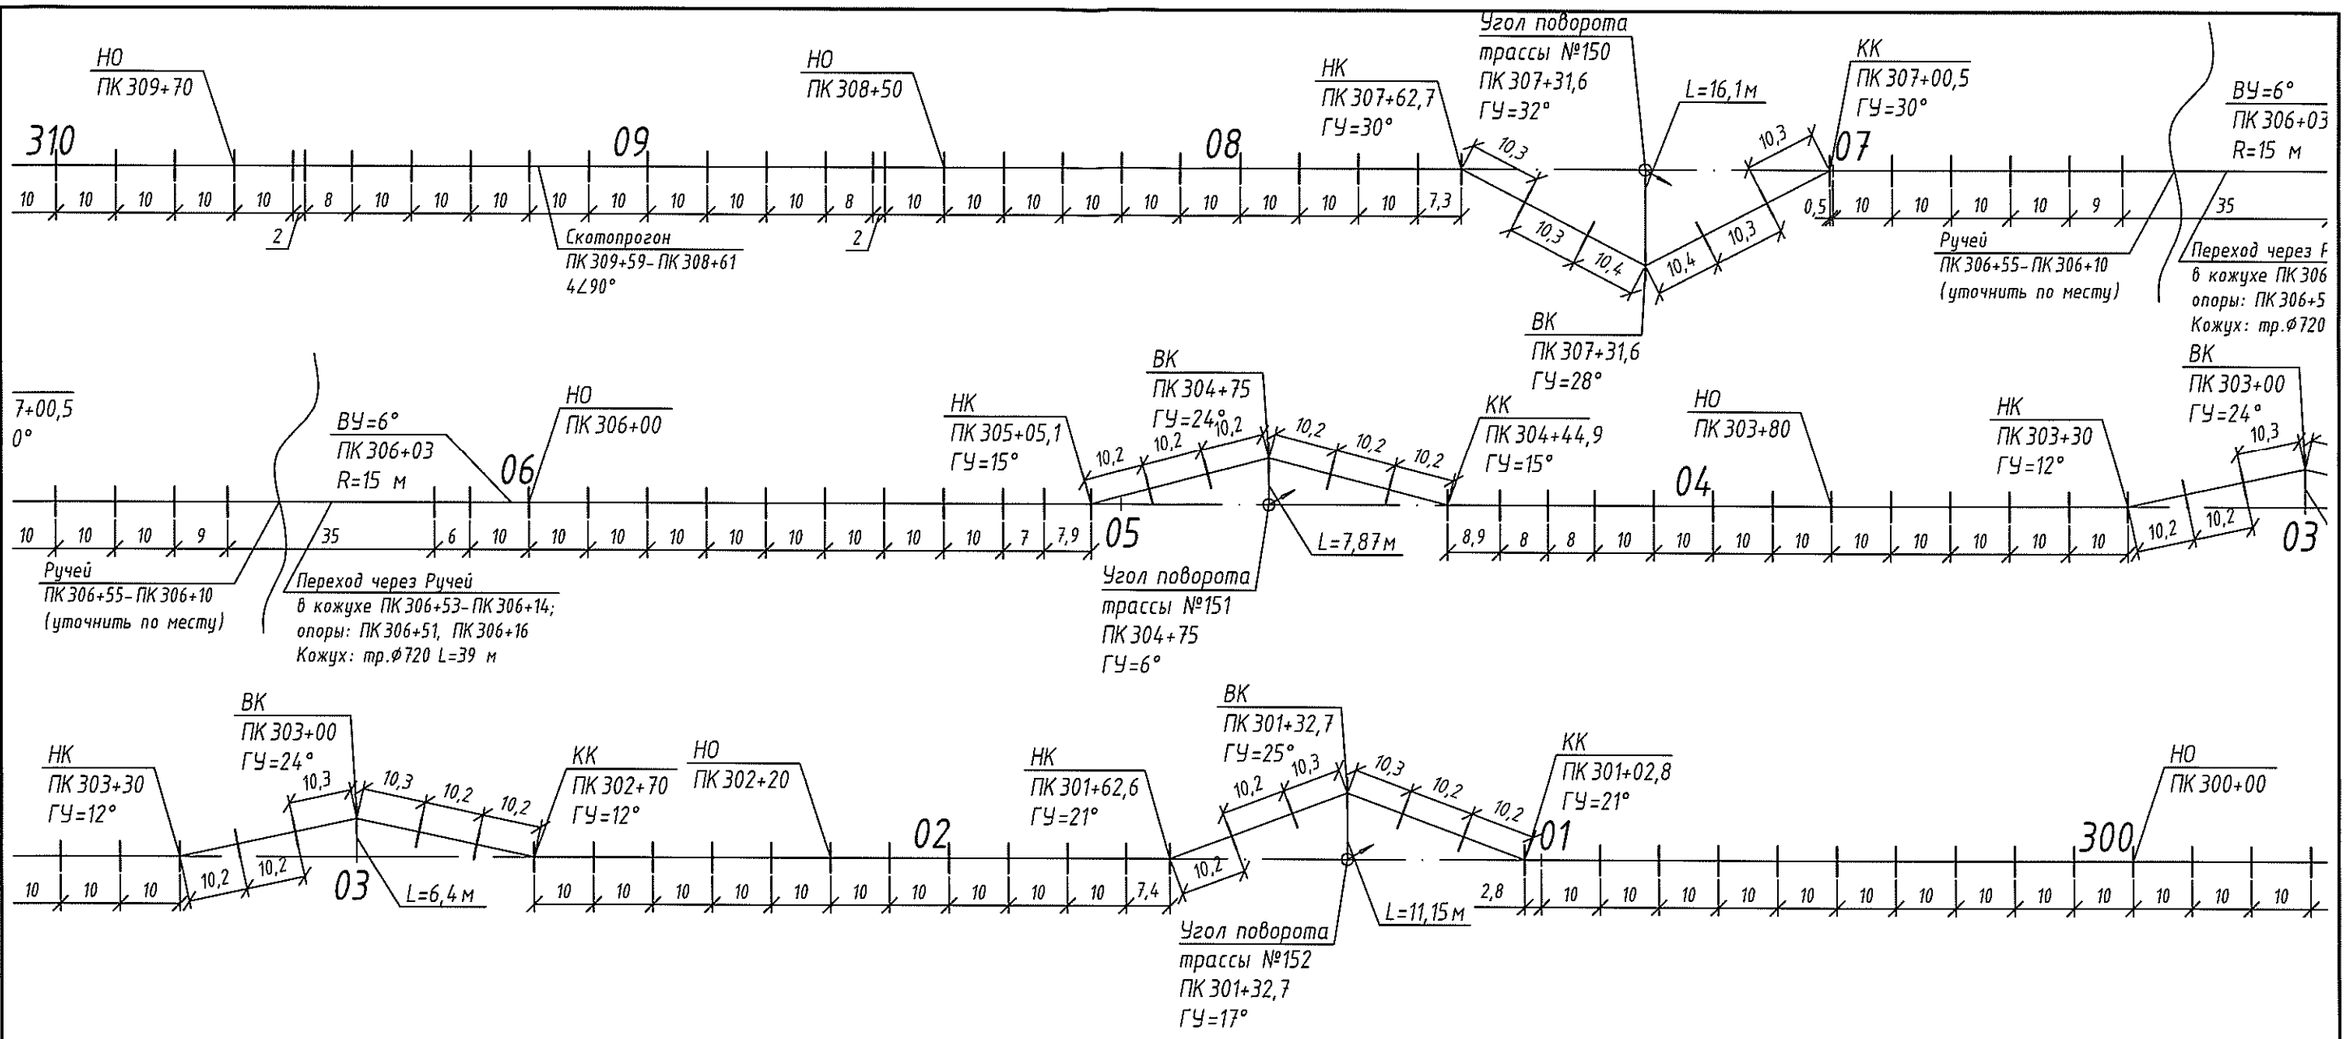
НО
ПК 309+70
310
10 10 10 10 10 2 8 10 10 10 10
Скотопрогон
ПК 309+59 – ПК 308+61
4∠90°
НО
ПК 308+50
09
2 10 10 10 10 10 10 10 10 10 8 2
НК
ПК 307+62,7
ГУ=30°
08
10 10 10 10 10 10 10 10 10 10 7,3
Угол поворота
трассы №150
ПК 307+31,6
ГУ=32°
L=16,1м
10,3 10,3 10,3 10,4 10,4 10,3
ВК
ПК 307+31,6
ГУ=28°
КК
ПК 307+00,5
ГУ=30°
07
0,5 10 10 10 10 9
ВУ=6°
ПК 306+03
R=15 м
35
Ручей
ПК 306+55 – ПК 306+10
(уточнить по месту)
Переход через Р
в кожухе ПК 306
опоры: ПК 306+5
Кожух: тр.Ø720
7+00,5
0°
10 10 10 9
Ручей
ПК 306+55 – ПК 306+10
(уточнить по месту)
ВУ=6°
ПК 306+03
R=15 м
35
Переход через Ручей
в кожухе ПК 306+53 – ПК 306+14;
опоры: ПК 306+51, ПК 306+16
Кожух: тр.Ø720 L=39 м
НО
ПК 306+00
06
6 10 10 10 10 10 10 10 10 10 10 7 7,9
НК
ПК 305+05,1
ГУ=15°
ВК
ПК 304+75
ГУ=24°
10,2 10,2 10,2 10,2 10,2 10,2
05
L=7,87м
Угол поворота
трассы №151
ПК 304+75
ГУ=6°
КК
ПК 304+44,9
ГУ=15°
8,9 8 8 10 10 10 10 10 10 10 10 10
НО
ПК 303+80
04
НК
ПК 303+30
ГУ=12°
ВК
ПК 303+00
ГУ=24°
10,3
10,2 10,2
03
НК
ПК 303+30
ГУ=12°
ВК
ПК 303+00
ГУ=24°
10,3 10,3 10,2 10,2
10,2 10,2
03
L=6,4м
КК
ПК 302+70
ГУ=12°
НО
ПК 302+20
02
10 10 10 10 10 10 10 10 10 10 7,4
НК
ПК 301+62,6
ГУ=21°
ВК
ПК 301+32,7
ГУ=25°
10,2 10,3 10,3 10,2 10,2
10,2
Угол поворота
трассы №152
ПК 301+32,7
ГУ=17°
L=11,15м
КК
ПК 301+02,8
ГУ=21°
01
2,8 10 10 10 10 10 10 10 10 10 10 10 10
НО
ПК 300+00
300
НО
ПК 300+00
300
10 10 10 10 10 10 10 10 10 10 10
НК
ПК 299+00
ГУ=12°
ВК
ПК 298+70
ГУ=24°
10,3 10,3 10,2 10,2
10,2 10,2
99
L=6,4м
КК
ПК 298+40
ГУ=12°
98
10 10 10 10 10 10 10 10 10 10
НО
ПК 297+40
ВУ=3°
ПК 297+37
R=15 м
97
НК
ПК 296+40
ГУ=12°
ВК
ПК 2
ГУ=
10,2
L=
НК
ПК 296+40
ГУ=12°
ВК
ПК 296+10
ГУ=24°
10,2 10,3 10,3 10,2 10,2
10,2
96
L=6,4м
КК
ПК 295+80
ГУ=12°
НО
ПК 294+80
95
10 10 10 10 10 10 10 10 10 10 10

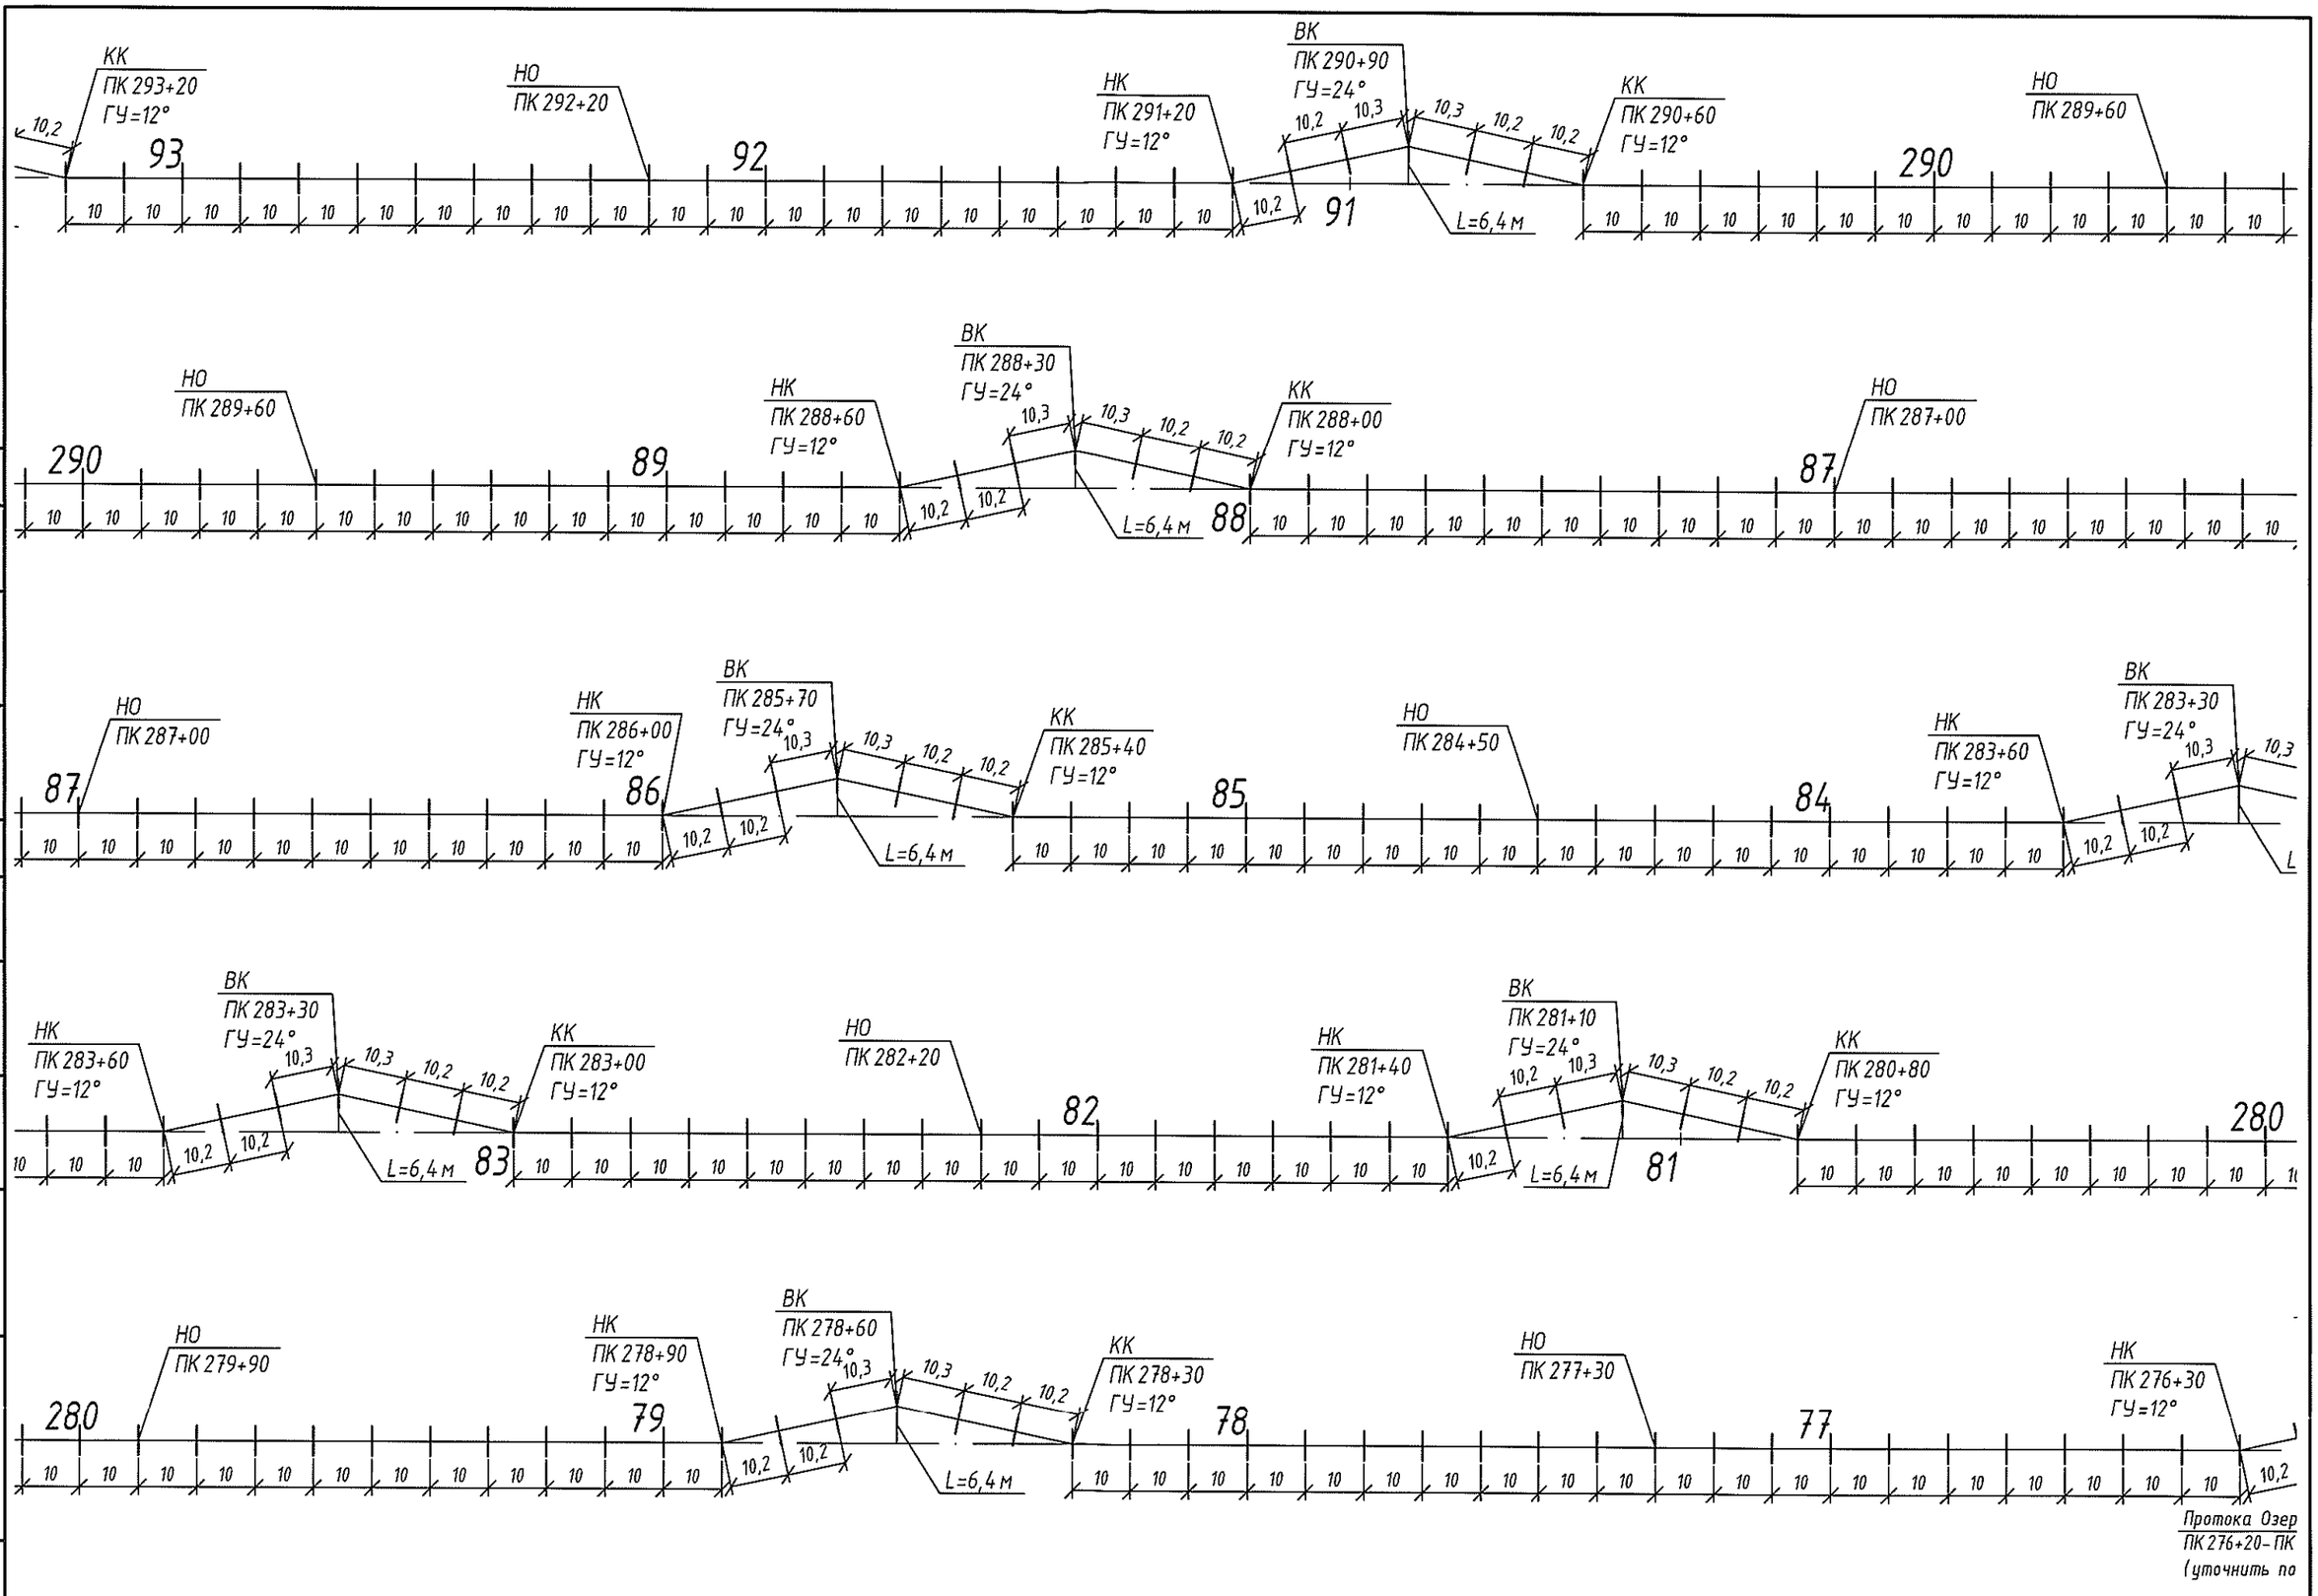

Согласовано


Взам.инв.N

Подпись и дата

Инв.N подл.

Изм.	Кол.уч.	Лист	N док.	Подпись	Дата	III-Д-101/3103-КМ.Л2	Лист 22

Формат А3

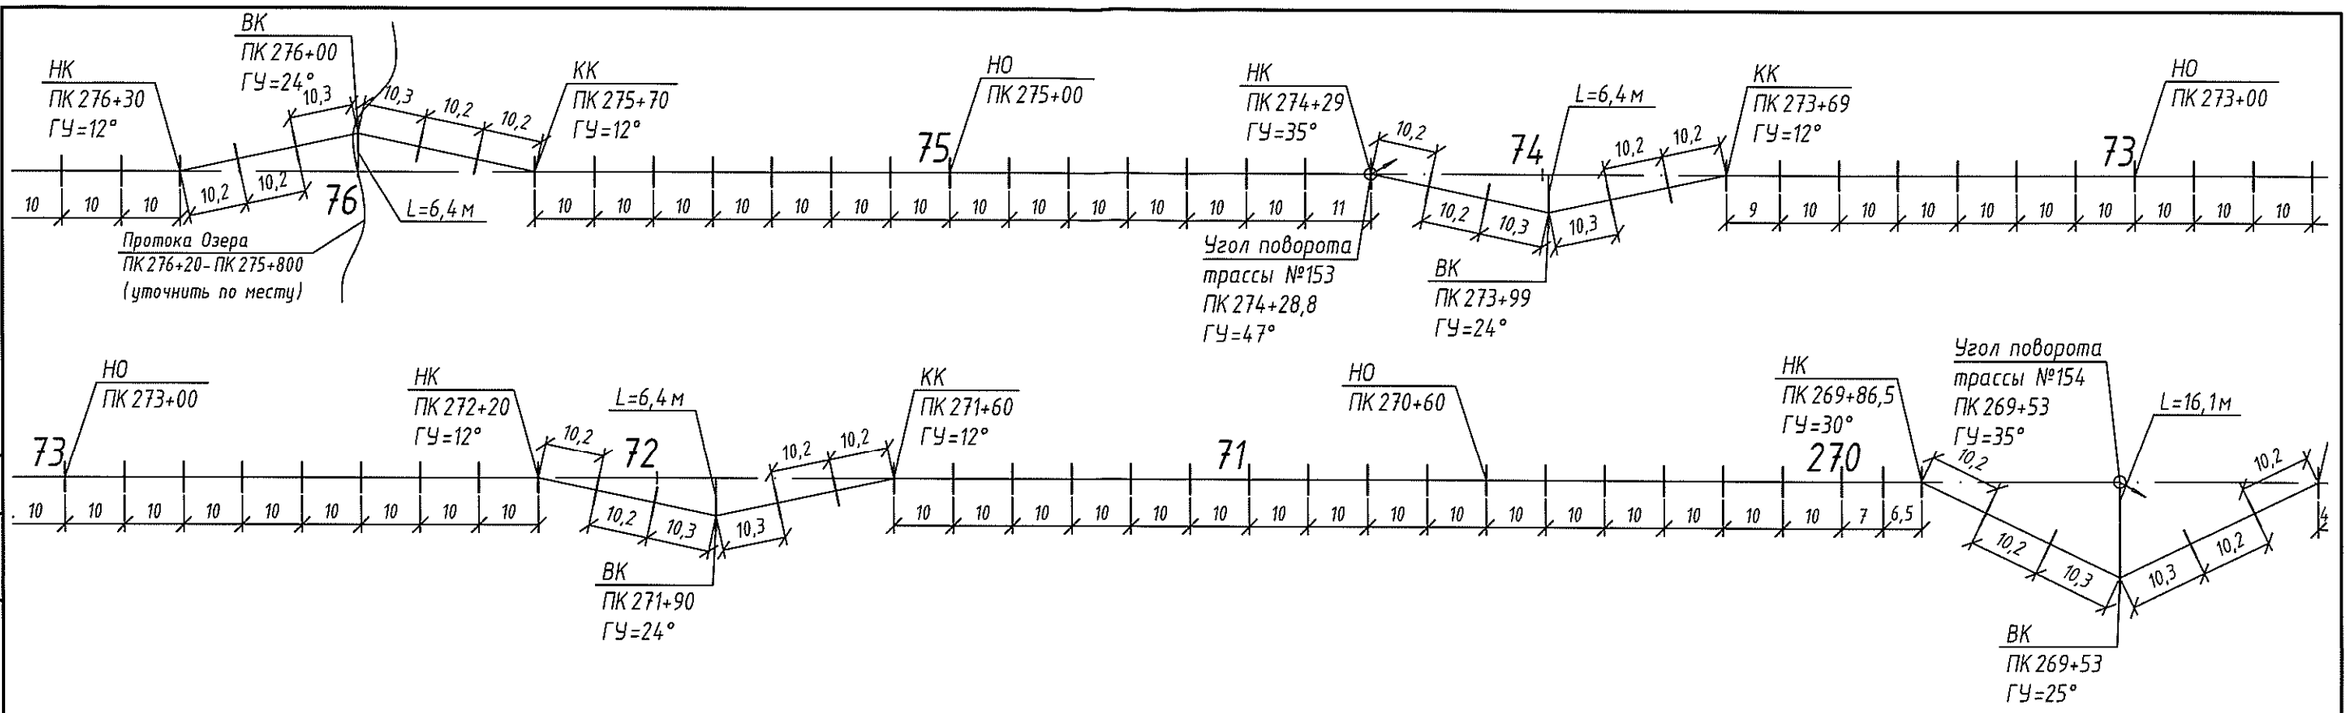

Согласовано

Взам.инв.N

Подпись и дата


Инв.N подл.


Изм.	Кол.уч.	Лист	N док.	Подпись	Дата


III-Д-101/3103-КМ.Л2

Лист 23

Формат А3

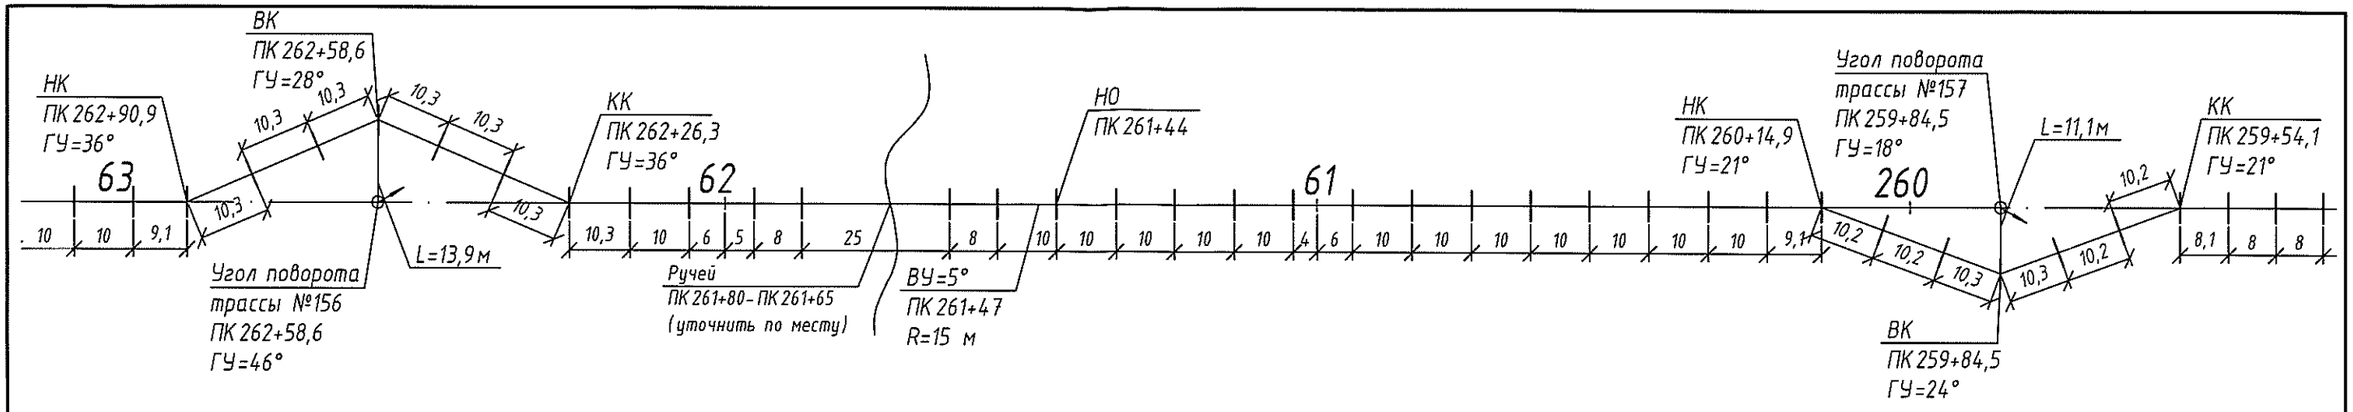

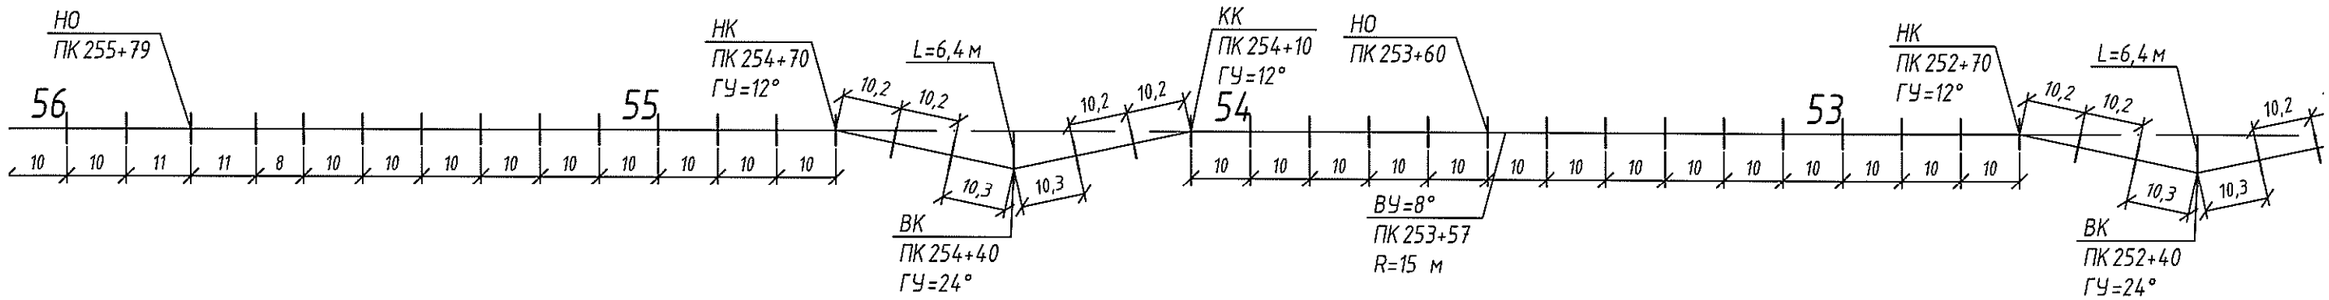

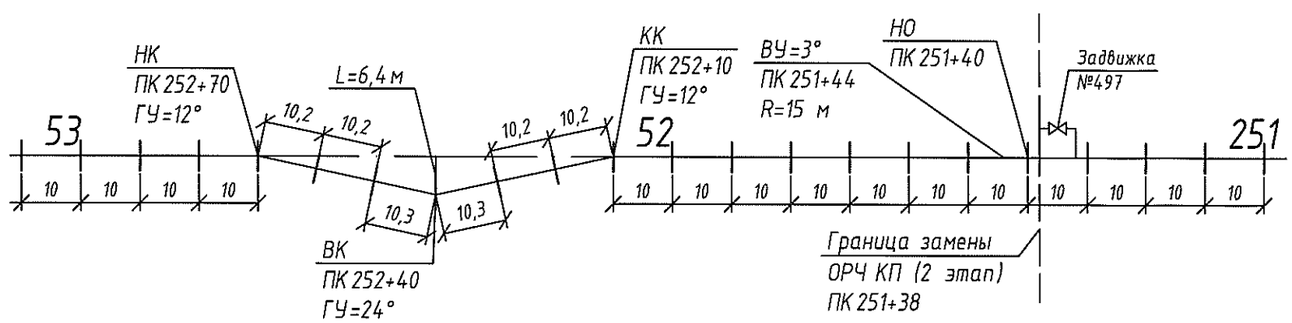

Согласовано

Взам.инв.N

Подпись и дата

Инв.N подл.

Изм.	Кол.уч.	Лист	N док.	Подпись	Дата

III-Д-101/3103-КМ.Л2

Лист 24

Формат А3